


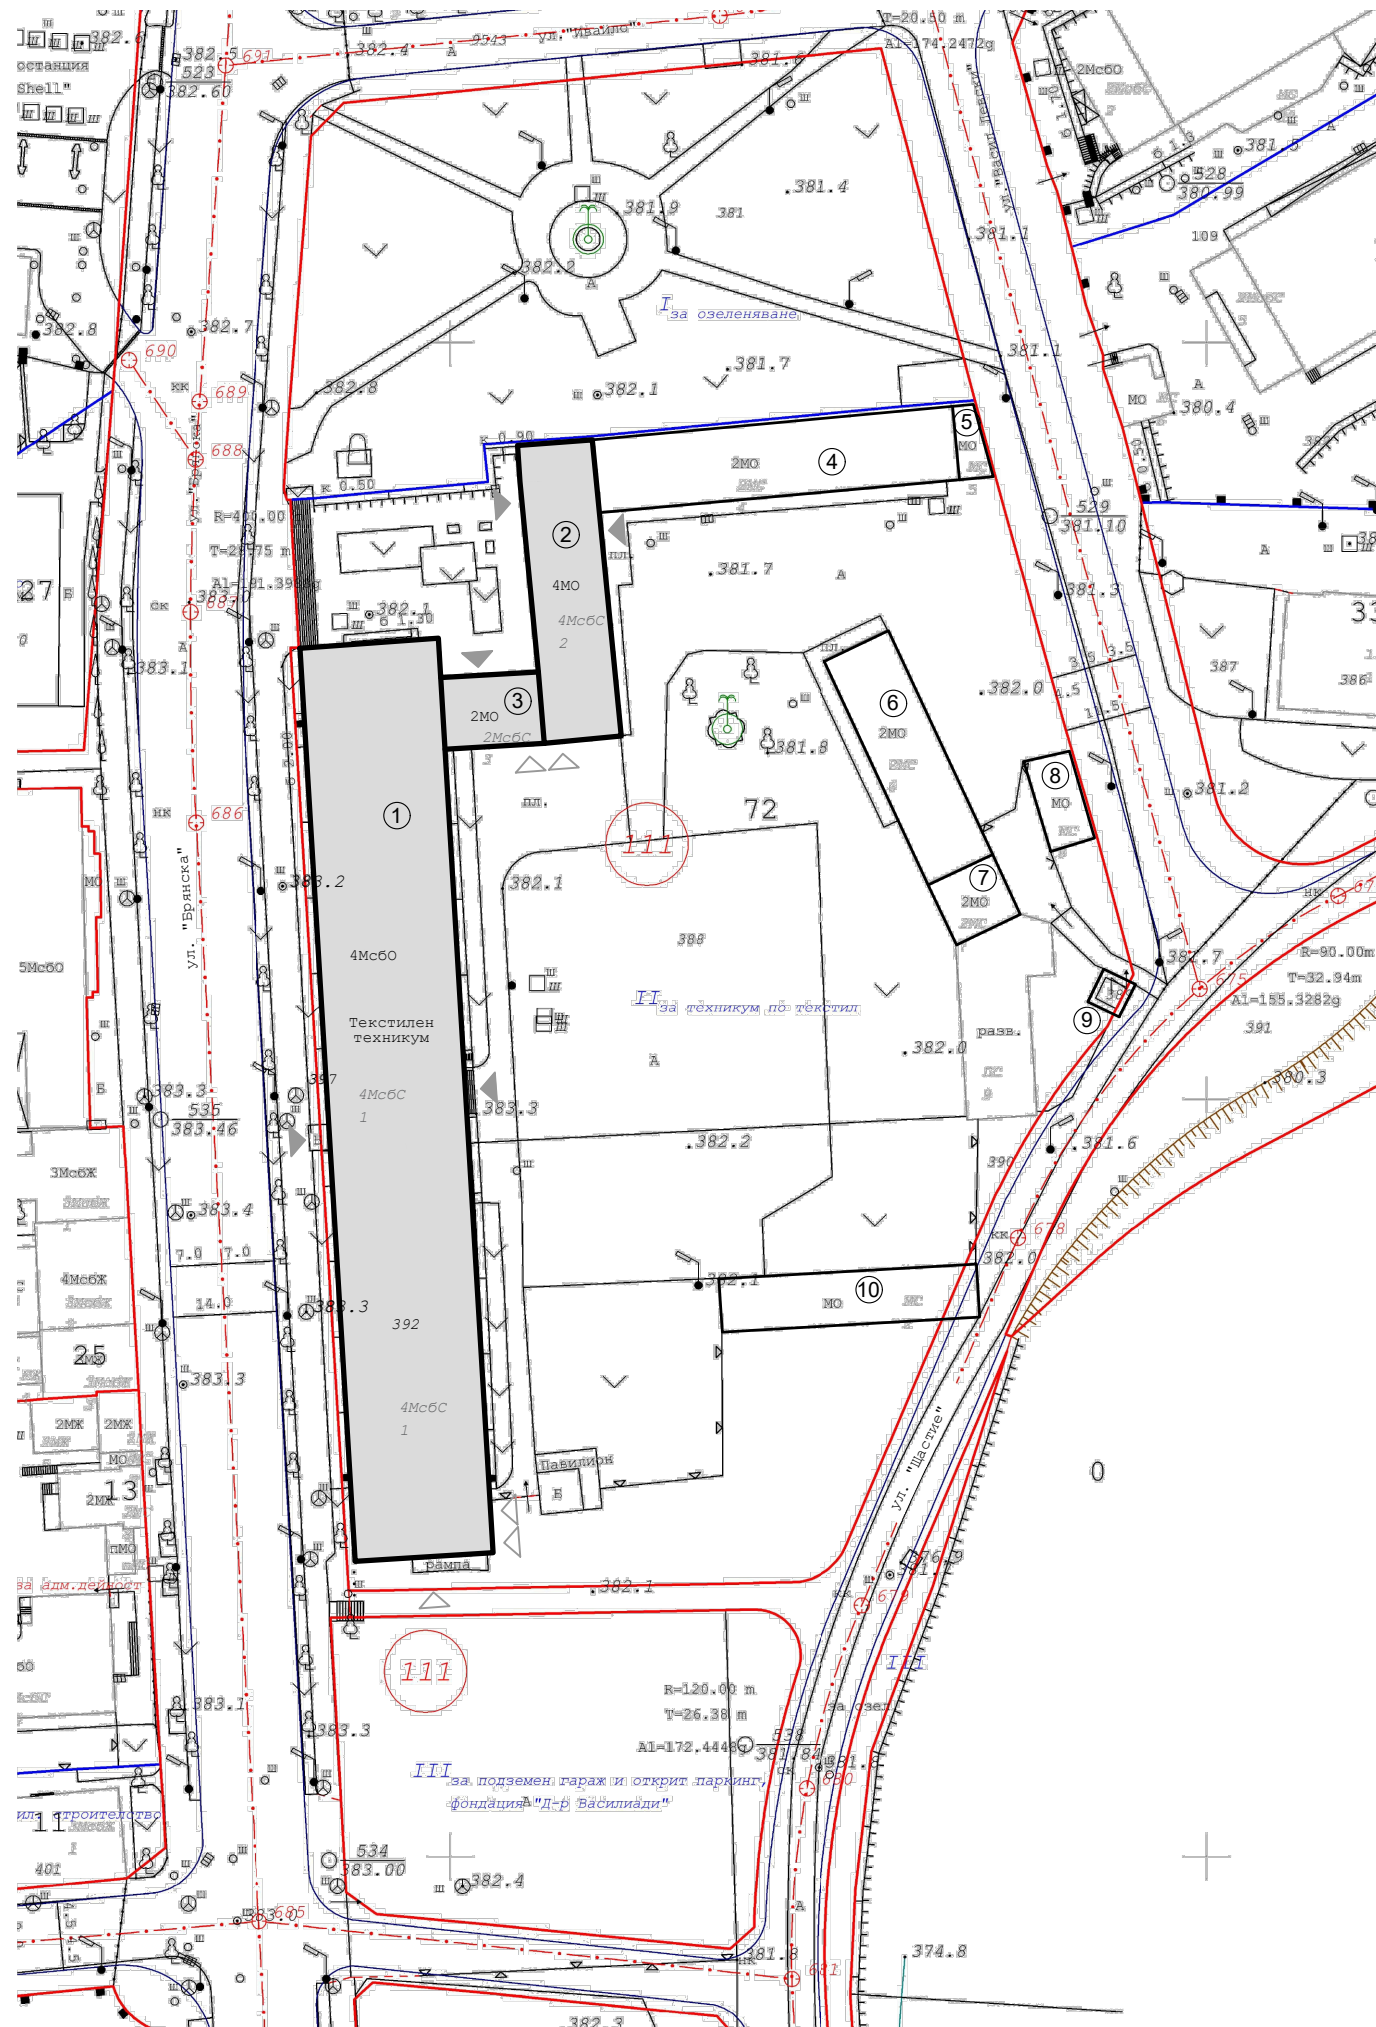

ЛЕГЕНДА:			
Улична мрежа			
Тротоари, пешеходни площи и паркова алейна мрежа			
Жилищни сгради (съществуващи)			
Жилищни сгради (нови)			
Обществено-обслужващи сгради (съществуващи)			
Подземни гаражи			
ПЕЧАТ НА ГЛАВНИЯ ПРОЕКТАНТ:			
ВЪЗЛОЖИТЕЛ:		ПОДПИС:	
ОБЩИНА ГАБРОВО			
ОБЕКТ:			
Архитектурно заснемане на сградата на бившата Професионална гимназия по текстил и моден дизайн			
Разположение съгласно ПУП: УПИ II-за техникум по текстил, квартал 111 по ПУП на ЦГЧ на гр. Габрово; Разположение съгласно КККР: поземлен имот с идентификатор 14218.504.402 по КККР на гр. Габрово; Идентификатор на сграда: 14218.504.402.3			
ЧЕРТЕЖ:		ПОДРОБЕН УСТРОЙСТВЕН ПЛАН- ПЛАН ЗА ЗАСТРОЯВАНЕ НА ЦЕНТРАЛНА ГРАДСКА ЧАСТ- ГАБРОВО	
ФАЗА: АРХИТЕКТУРНО ЗАСНЕМАНЕ			
ГЛАВЕН ПРОЕКТАНТ:		арх. Я. ПАНЕВ	
СПЕЦИАЛНОСТ:		СЪГЛАСУВАЛ:	ПОДПИС:
Архитектура		арх. Я. ПАНЕВ	
ЧАСТ:		Архитектура	ДАТА: 2023г.
МАЩАБ:		1:1000	ЛИСТ № : 2/25




ГРАДОУСТРОЙСТВЕНИ
ПАРАМЕТРИ ЗА
УПИ II-за техникум по текстил
(състоящо се от ПИ: 14218.504.401,
14218.504.402, 14218.504.403
по КККР на гр. Габрово)

Площ на УПИ: 13856 кв.м.


ПАРАМЕТРИ ПО ПУП:
П застрояване % 40
Кинт 1.2
MIN озел. площ % 20

ПОСТИГНАТИ ПАРАМЕТРИ:
П застрояване % 28.7
Кинт 0.9
Озел. площ % 20.5


ЛЕГЕНДА:		
УЛИЧНА РЕГУЛАЦИОННА ЛИНИЯ		
ГРАНИЦА НА ИМОТ		
СГРАДИ ЗА ПРОФЕСИОНАЛНА ГИМНАЗИЯ ПО ТЕКСТИЛ И МОДЕН ДИЗАЙН:		
① ТЯЛО 1 - ЗП 2217 кв.м.		
② ТЯЛО 2 - ЗП 398 кв.м.		
③ ТОПЛА ВРЪЗКА - ЗП 122 кв.м.		
ДРУГИ СГРАДИ В УПИ:		
④ ПРОИЗВОДСТВЕНО-СКЛАДОВА СГРАДА - ЗП 486 кв.м.		
⑤ ПРОИЗВОДСТВЕНО-СКЛАДОВА СГРАДА - ЗП 40 кв.м.		
⑥ ПРОИЗВОДСТВЕНО-СКЛАДОВА СГРАДА - ЗП 305 кв.м.		
⑦ ПРОИЗВОДСТВЕНО-СКЛАДОВА СГРАДА - ЗП 81 кв.м.		
⑧ ПРОИЗВОДСТВЕНО-СКЛАДОВА СГРАДА - ЗП 80 кв.м.		
⑨ СГРАДА ЗА ЕНЕРГОПРОИЗВОДСТВО - ЗП 9 кв.м.		
⑩ ПРОИЗВОДСТВЕНО-СКЛАДОВА СГРАДА - ЗП 243 кв.м. (ЗА ПРЕМАХВАНЕ)		
111 НОМЕР НА КВАРТАЛ		
II 63 НОМЕР НА УПИ		
63 НОМЕР НА ПИ		
ГЛАВЕН ВХОД		
ВТОРОСТЕПЕНЕН ВХОД		
ПЕЧАТ НА ГЛАВНИЯ ПРОЕКТАНТ:		
ВЪЗЛОЖИТЕЛ:		ПОДПИС:
ОБЩИНА ГАБРОВО		
ОБЕКТ: Архитектурно заснемане на сградата на бившата Професионална гимназия по текстил и моден дизайн		
Разположение съгласно ПУП: УПИ II-за техникум по текстил, квартал 111 по ПУП на ЦГЧ на гр. Габрово; Разположение съгласно КККР: поземлен имот с идентификатор 14218.504.402 по КККР на гр. Габрово; Идентификатор на сграда: 14218.504.402.3		
ЧЕРТЕЖ: СИТУАЦИЯ		
ФАЗА: АРХИТЕКТУРНО ЗАСНЕМАНЕ		
ГЛАВЕН ПРОЕКТАНТ:		арх. Я. ПАНЕВ
СПЕЦИАЛНОСТ:	СЪГЛАСУВАЛ:	ПОДПИС:
Архитектура	арх. Я. ПАНЕВ	
ЧАСТ:	Архитектура	ДАТА: 2023г.
МАЩАБ:	1:1000	ЛИСТ № : 3/25

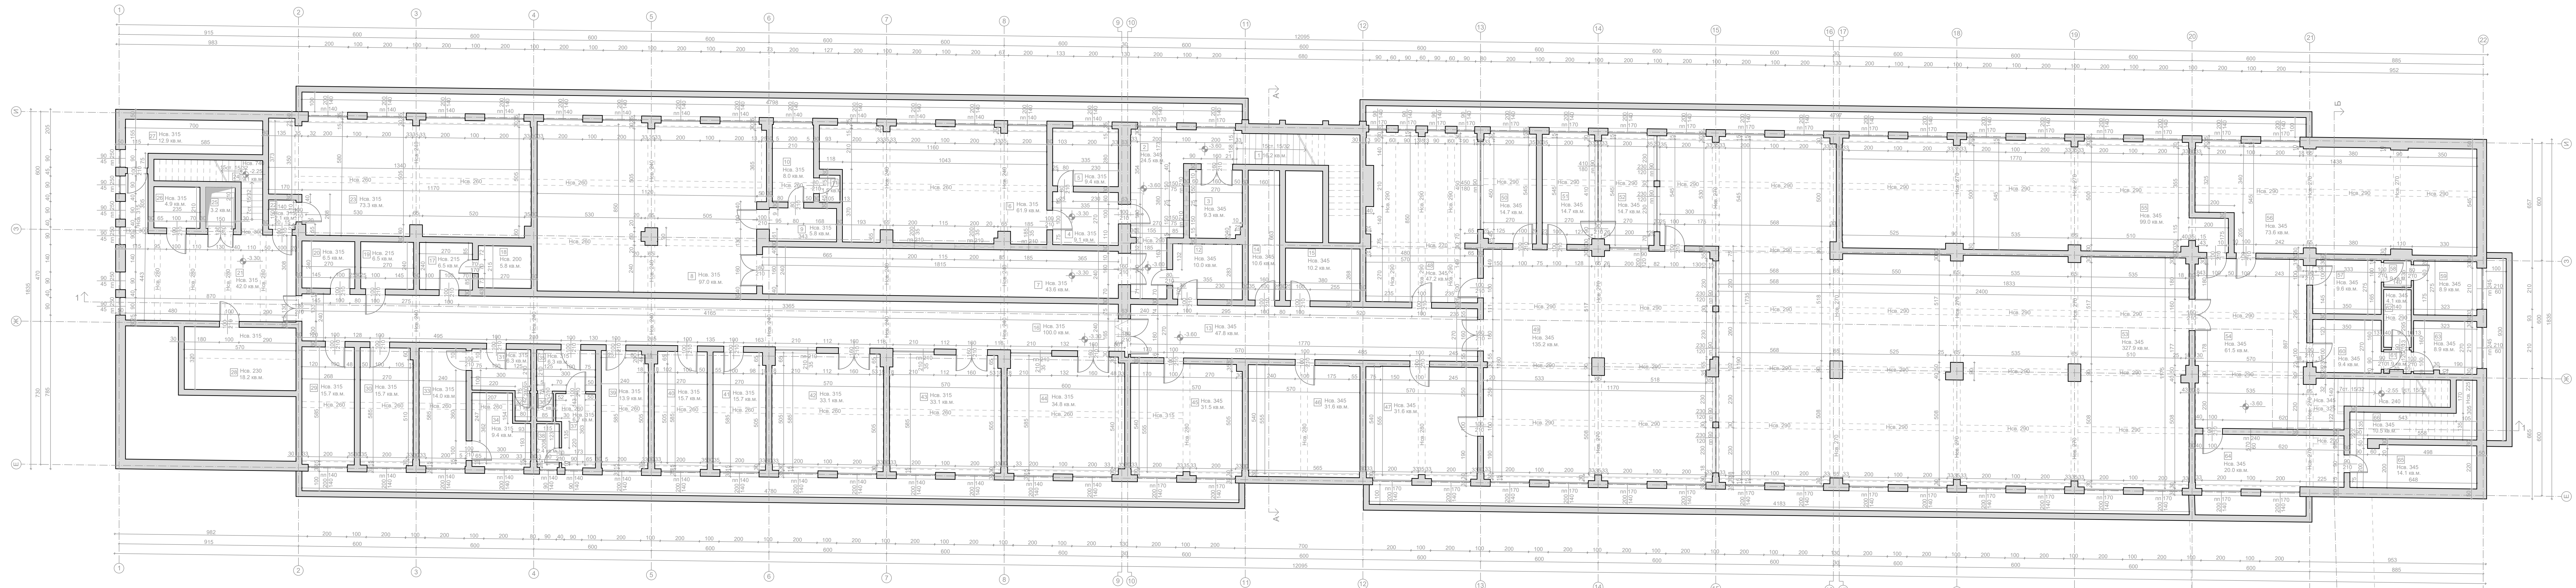

Тяло 1
План етаж -1
Кота -3.60

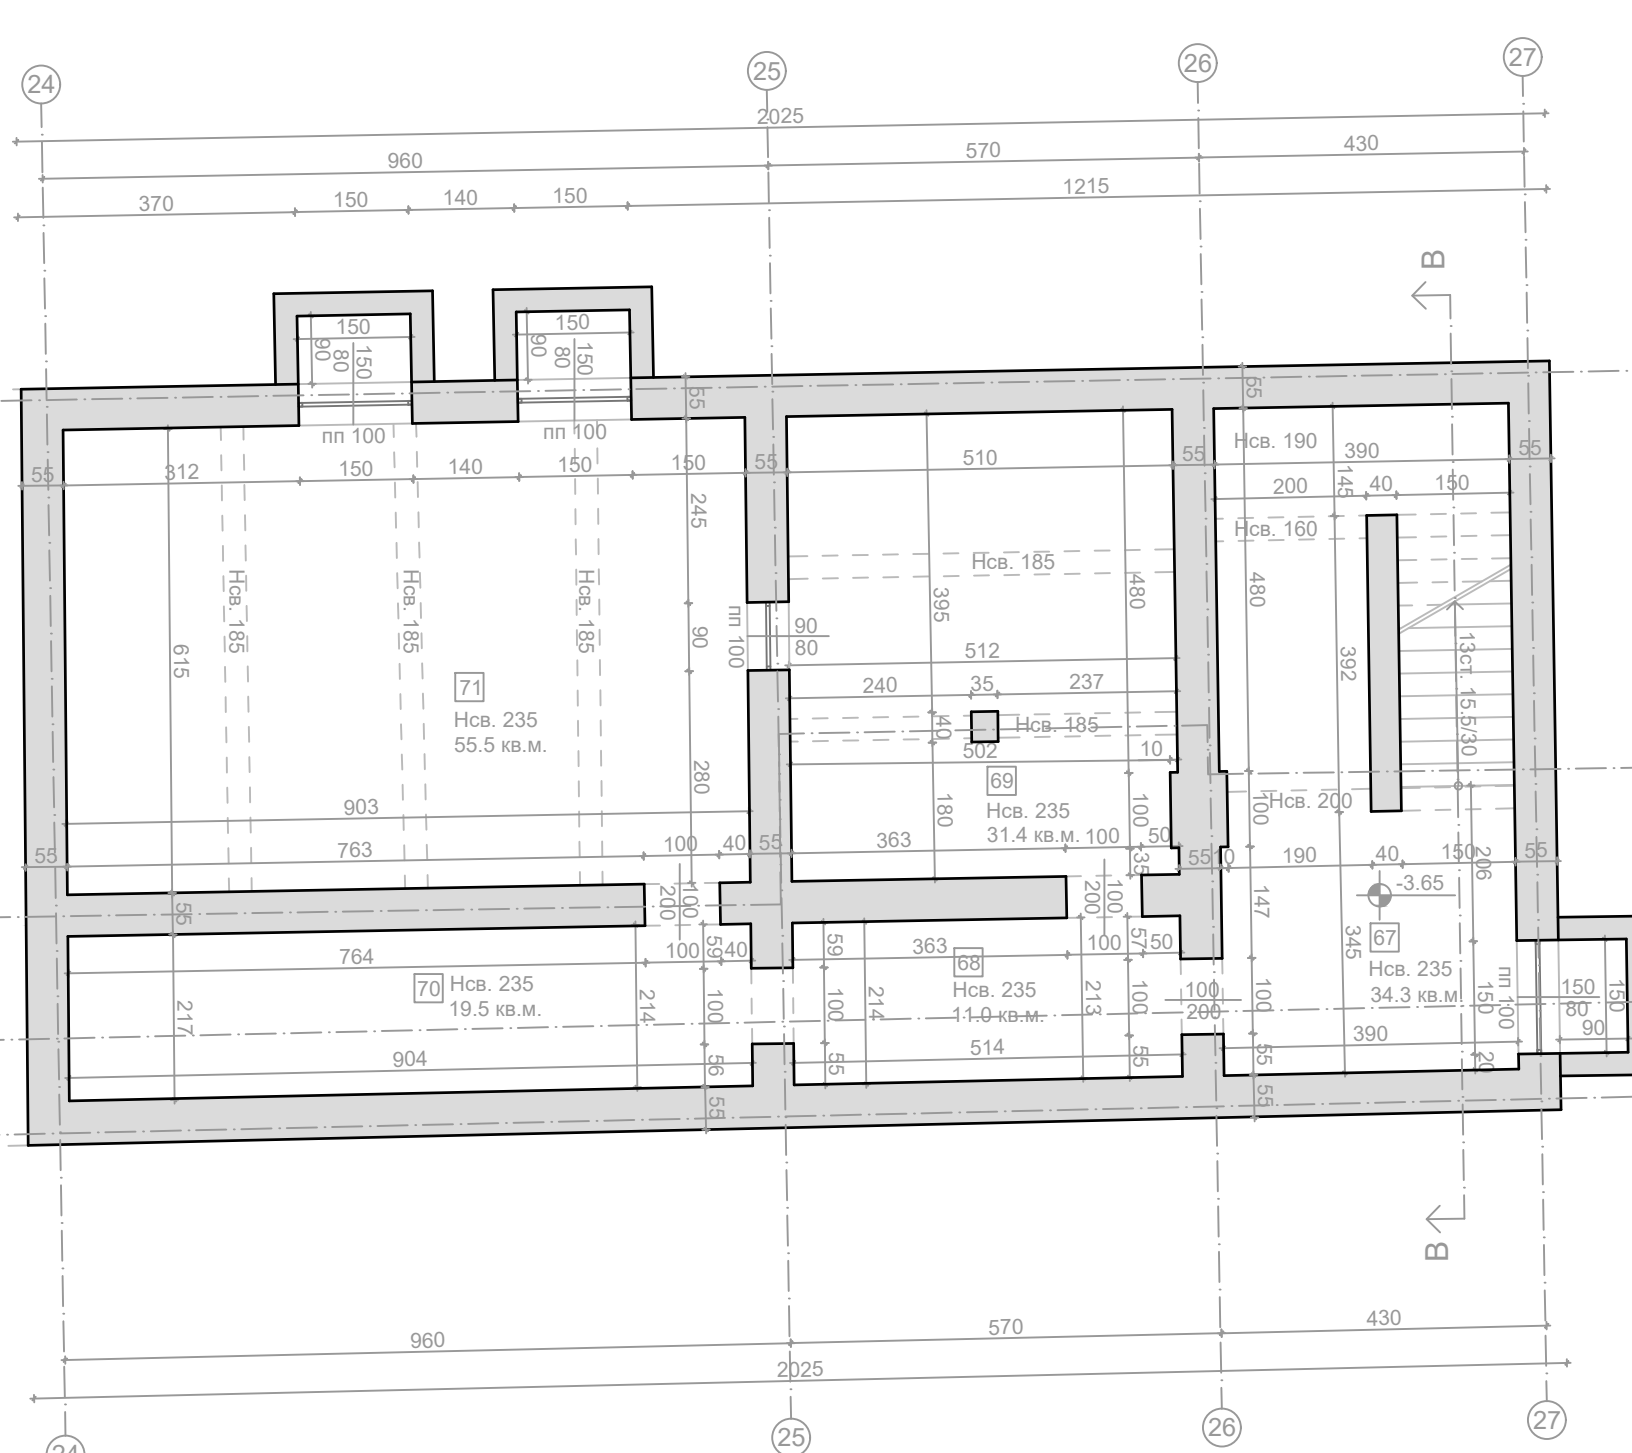

Тяло 2
План етаж -1
Кота -3.65

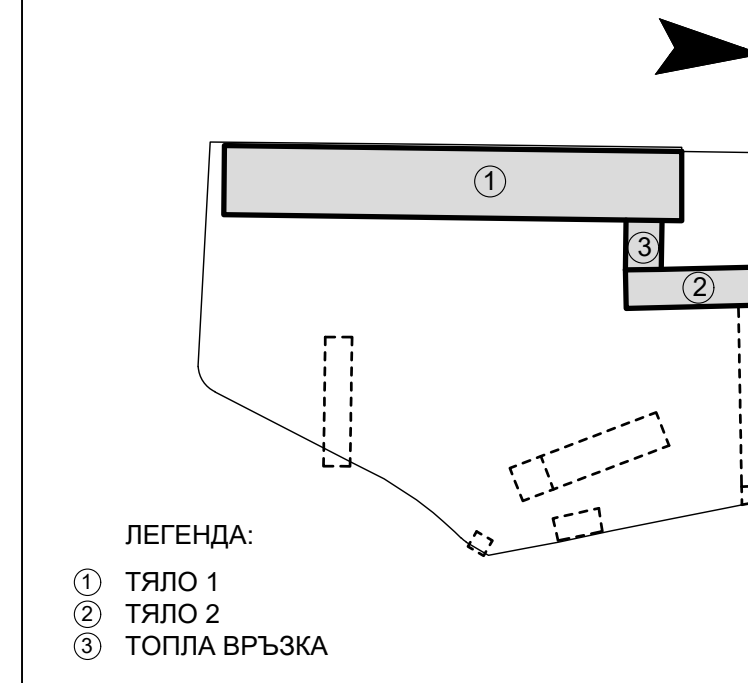

ЛЕГЕНДА:
1 ТЯЛО 1
2 ТЯЛО 2
3 ТОПЛА ВЪРЪКА

СИТУАЦИОННА СХЕМА

МАЩАБ: 1:2000

№	Помещение	Площ, кв.м.	Стен	Покр.	Покр.
1	службена китка	16.2	мащаб	мащаб	мащаб
2	кухня	24.5	мащаб	мащаб	мащаб
3	посещение	2.5	мащаб	мащаб	мащаб
4	посещение	3.1	-	-	-
5	посещение	3.1	-	-	-
6	посещение	3.1	-	-	-
7	кухня	23.8	-	-	-
8	посещение	2.5	-	-	-
9	посещение	3.1	-	-	-
10	посещение	3.1	-	-	-
ТЯЛО 2 - 200 м

47	службена китка	24.5	Бетонна плоча	мащаб	мащаб
48	кухня	11.5	Бетонна плоча	мащаб	мащаб
49	посещение	11.5	Бетонна плоча	мащаб	мащаб
50	кухня	11.5	Бетонна плоча	мащаб	мащаб
51	посещение	11.5	Бетонна плоча	мащаб	мащаб

ПЕЧАТ НА ГЛАВНИЯ ПРОЕКТАНТ:

ВЪЗЛОЖИТЕЛ:

ПОДПИС:

ОБЩИНА ГАБРОВО

ОБЕКТ:

Архитектурно заснемане на сградата на бившата

Професионална гимназия по текстил и моден дизайн

Разположение: съгласно ПУП, УПИ II-за техникум по

текстил, квартал 111 по ПУП на ЦГМ на гр. Габрово;

Разположение: съгласно ККОП; поминен имат с

идентификатор 14218.504.402 по ККОП на гр. Габрово;

Идентификатор на сградата: 14218.504.402.3

ЧЕРТЕЖ:

ТЯЛО 1 КОТА -3.60

ТЯЛО 2 КОТА -3.65

ФАЗА:

АРХИТЕКТУРНО ЗАСНЕМАНЕ

ГЛАВЕН ПРОЕКТАНТ:

арх. Я. ПАНЕВ

СПЕЦИАЛНОСТ:

СЪГЛАСОВАЛ:

арх. Я. ПАНЕВ

ЧАСТ:

Архитектура

ДАТА:


2023г.

МАЩАБ:

1:100

ЛИСТ №:

4/25

 

Тяло 1
План етаж +1
Кота ±0.00

Топла връзка
План етаж +1
Кота -1.15

Тяло 2
План етаж +1
Кота -1.15

ЛЕГЕНДА:
1. ТЯЛО 1
2. ТЯЛО 2
3. ТОПЛА ВРЪЗКА

СИТУАЦИОННА СХЕМА

МАЩАБ: 1:2000

№	Помещение	Площ, кв.м.	Стен	Покр.
1	таблор	24.9	мазони	мазони
2	архив	100.9	мазони	мазони
3	спал	21.7	мазони	мазони
4	спал	19.2	мазони	мазони
5	спал	22.9	мазони	мазони
6	спал	20.1	мазони	мазони
7	студийна стая	22.9	мазони	мазони
8	коридор	1.6	мазони	гидроизолация
9	коридор	1.2	мазони	гидроизолация
10	коридор	1.7	мазони	гидроизолация
11	спал	20.3	мазони	мазони
12	спал	20.3	мазони	мазони
13	коридор	1.6	мазони	гидроизолация
14	спал	13.5	мазони	мазони
15	спал	22.2	мазони	спр.
16	спал	20.7	мазони	мазони
17	коридор	25.4	мазони	мазони
18	спал	20.7	мазони	мазони
19	спал	20.0	мазони	мазони
20	спал	20.2	мазони	мазони
21	спал	20.8	мазони	мазони
22	спал	21.4	мазони	мазони
23	спал	20.4	мазони	мазони
24	техническо помещение	28.7	бетонна изстилка	мазони
25	техническо помещение	1.6	бетонна изстилка	мазони
26	техническо помещение	2.2	бетонна изстилка	мазони
27	техническо помещение	4.5	мазони	мазони
28	коридор	3.2	мазони	мазони
29	студийна стая	21.1	мазони	мазони
30	помещение	13.7	мазони	мазони
31	коридор	10.2	мазони	мазони
32	спал	20.9	перит	оборудованост
33	спал	20.0	мазони	мазони
34	спал	20.9	мазони	мазони
35	спал	20.3	мазони	мазони
36	спал	20.2	мазони	мазони
37	помещение	26.9	мазони	мазони
38	помещение	22.9	мазони	мазони
39	спал	20.3	мазони	мазони
40	коридор	2.4	мазони	мазони
41	помещение	14.4	мазони	мазони
42	спал	20.8	мазони	мазони
43	спал	20.9	мазони	мазони
44	спал	перит	мазони	мазони
45	помещение	19.2	перит	мазони
46	спал	20.9	мазони	мазони
47	помещение	16.1	мазони	мазони
48	помещение	21.4	мазони	мазони
49	техническо помещение	21.2	мазони	мазони
50	студийна стая	26.5	мазони	мазони
51	спал	22.1	мазони	мазони
52	коридор	1.9	мазони	мазони

ТОПЛА ВРЪЗКА - 1220 кв.м.					
53	архив	34.2	мазони	мазони	мазони
54	помещение	43.8	гранитерос	мазони	окрасен таван
55	помещение	4.5	гранитерос	гидроизолация	мазони
56	помещение	5.6	баластум	мазони	мазони
57	помещение	17.7	-	-	-

ТАПОЛ 2 - 392 кв.м				
58	коридор	17.6	мазони	мазони
59	помещение	17.1	-	-
60	предход	7.7	балетум	мазони
61	спал	9.9	балетум	мазони
62	спал	10.5	балетум	мазони
63	коридор	17.2	мазони	мазони
64	спал	10.3	мазони	мазони
65	спал	45.2	паркет	мазони
66	спал	57.1	паркет	мазони
67	ст. клети и вестибюл	55.8	мазони	мазони
68	таблор	10.8	мазони	мазони

ПЕЧАТ НА ГЛАВНИЯ ПРОЕКТАНТ:

ОБЩИНА ГАБРОВО

ОБЕКТ:
Архитектурно заснемане на сградата на бившата
Професионална гимназия по текстил и моден дизайн
Разположение: съгласно ПУП, УПИ II-за техникум по
текстил, квартал 111 по ПУП на ЦГМ на гр. Габрово;
Разположение: съгласно ККОП: поменим имот с
идентификатор 14218.504.402 по ККОП на гр. Габрово;
Идентификатор на сградата: 14218.504.402.3

ЧЕРТЕЖ: ТЯЛО 1 КОТА ±0.00
ТЯЛО 2 КОТА -1.15
ТОПЛА ВРЪЗКА КОТА -1.15

ФАЗА: АРХИТЕКТУРНО ЗАСНЕМАНЕ

ГЛАВЕН ПРОЕКТАНТ: арх. Я. ПАНЕВ

СПЕЦИАЛНОСТ: СИГНАТУРА:

Архитектура арх. Я. ПАНЕВ

ЧАСТ: Архитектура

МАЩАБ: 1:100


ДАТА: 2023г.

ЛИСТ №: 5/25

Тяло 1
План етаж +1.5
Кота +2.65

Топла връзка
План етаж +2
Кота +2.65

Тяло 2
План етаж +2
Кота +2.65

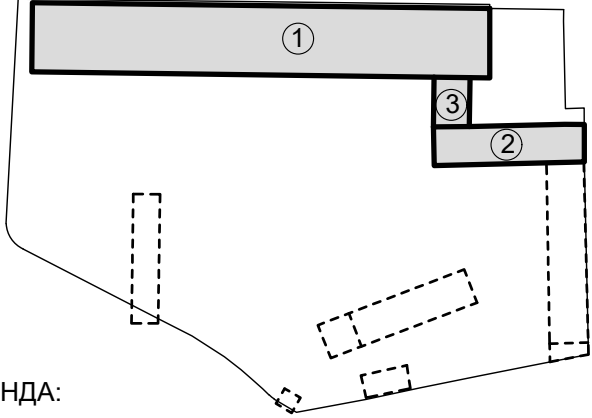

- ЛЕГЕНДА:
- 1 ТЯЛО 1
 - 2 ТЯЛО 2
 - 3 ТОПЛА ВРЪЗКА

СИТУАЦИОННА СХЕМА				МАЩАБ: 1:2000	
№	помещение	кв.м.	под	стени	таван
ТЯЛО 1					
1	стълбишна клетка	28.5	мозайка	мазитка	мазитка
2	помещение	23.4	паркет	мазитка	мазитка
3	коридор	6.9	мозайка	мазитка	мазитка
ТОПЛА ВРЪЗКА - 122кв.м.					
4	коридор	35.2	мозайка	мазитка	мазитка
5	стая	75.5	паркет	мазитка	мазитка
ТЯЛО 2 - 398кв.м.					
6	стая	35.4	паркет	мазитка	мазитка
7	коридор	17.6	мозайка	мазитка	мазитка
8	коридор	57.2	мозайка	мазитка	мазитка
9	стая	16.5	паркет	мазитка	мазитка
10	стая	18.3	паркет	облицовка	мазитка
11	стая	15.6	багетум	мазитка	мазитка
12	стая	28.5	багетум	мазитка	мазитка
13	стая	27.6	паркет	мазитка	мазитка
14	стая	27.6	паркет	мазитка	мазитка
15	ст. клетка и фойе	62.4	мозайка	мазитка	мазитка
16	стая	21.5	паркет	мазитка	мазитка

ПЕЧАТ НА ГЛАВНИЯ ПРОЕКТАНТ:

ВЪЗЛОЖИТЕЛ:
ОБЩИНА ГАБРОВО

ПОДПИС:

ОБЕКТ: Архитектурно заснемане на сградата на бившата
Професионална гимназия по текстил и моден дизайн

Разположение съгласно ПУП: УПИ II-за техникум по
текстил, квартал 111 по ПУП на ЦГЧ на гр. Габрово;
Разположение съгласно КККР: поземлен имот с
идентификатор 14218.504.402 по КККР на гр. Габрово;
Идентификатор на сграда: 14218.504.402.3

ЧЕРТЕЖ: **ТЯЛО 1 КОТА +2.65**
ТЯЛО 2 КОТА +2.65
ТОПЛА ВРЪЗКА КОТА +2.65

ФАЗА: АРХИТЕКТУРНО ЗАСНЕМАНЕ


ГЛАВЕН ПРОЕКТАНТ: арх. Я. ПАНЕВ

СПЕЦИАЛНОСТ: СЪГЛАСУВАЛ: ПОДПИС:

Архитектура арх. Я. ПАНЕВ


ЧАСТ: Архитектура ДАТА: 2023г.

МАЩАБ: 1:100 ЛИСТ №: 6/25

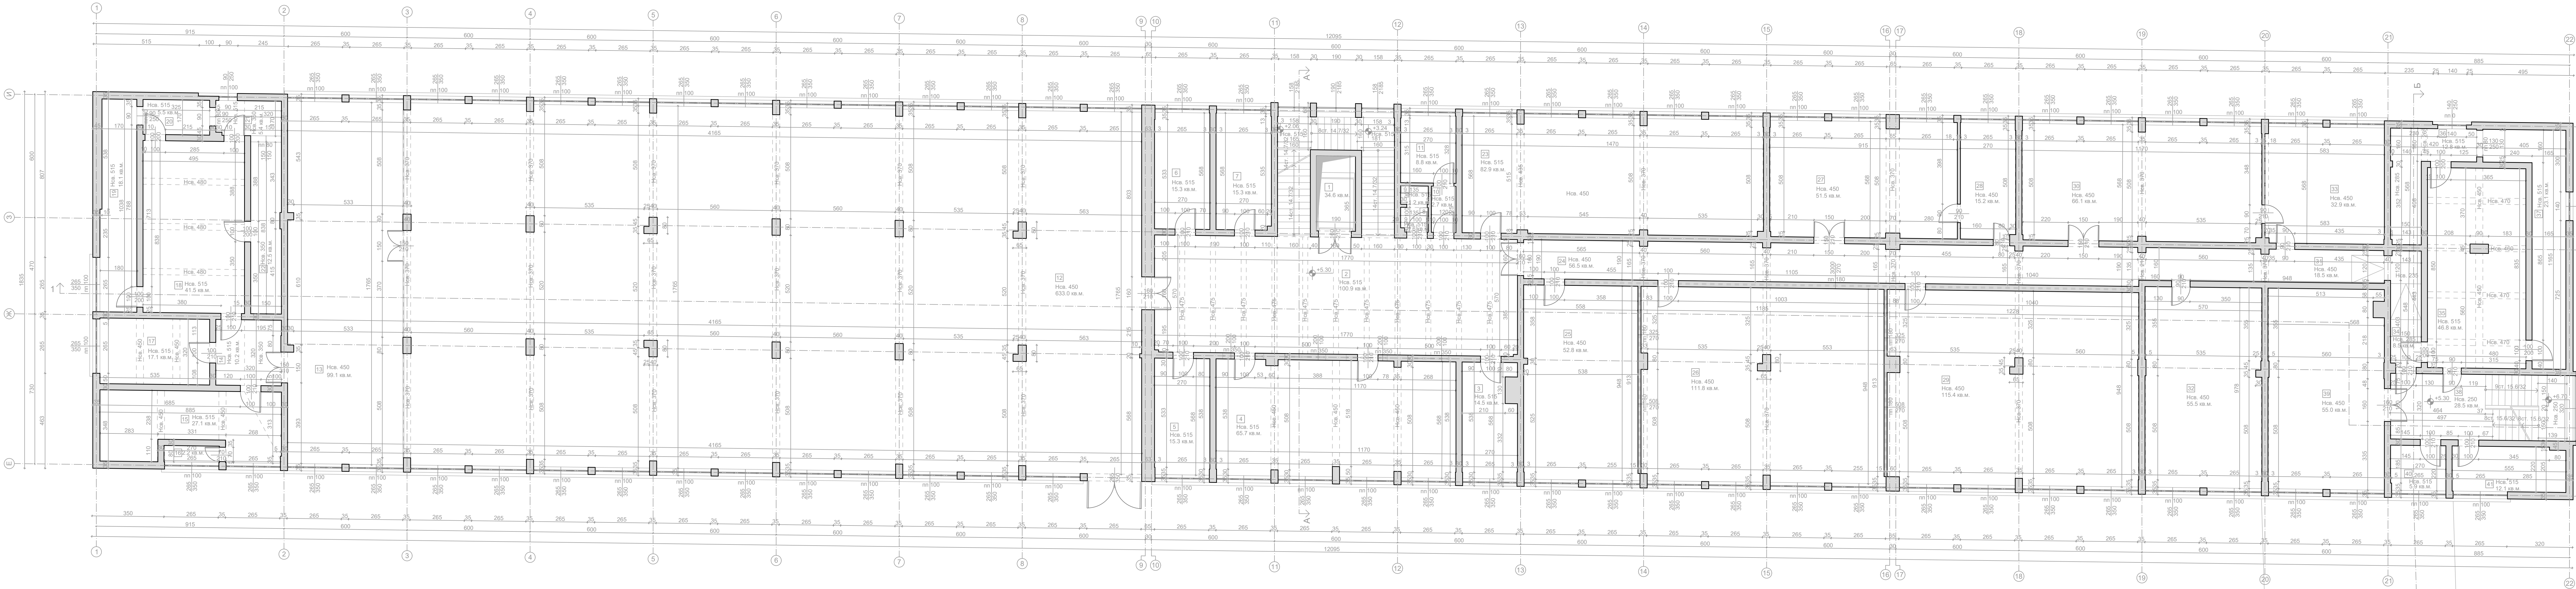


Тяло 1
План етаж +2
Кота +5.30

Топла връзка
План покрив
Кота +6.30

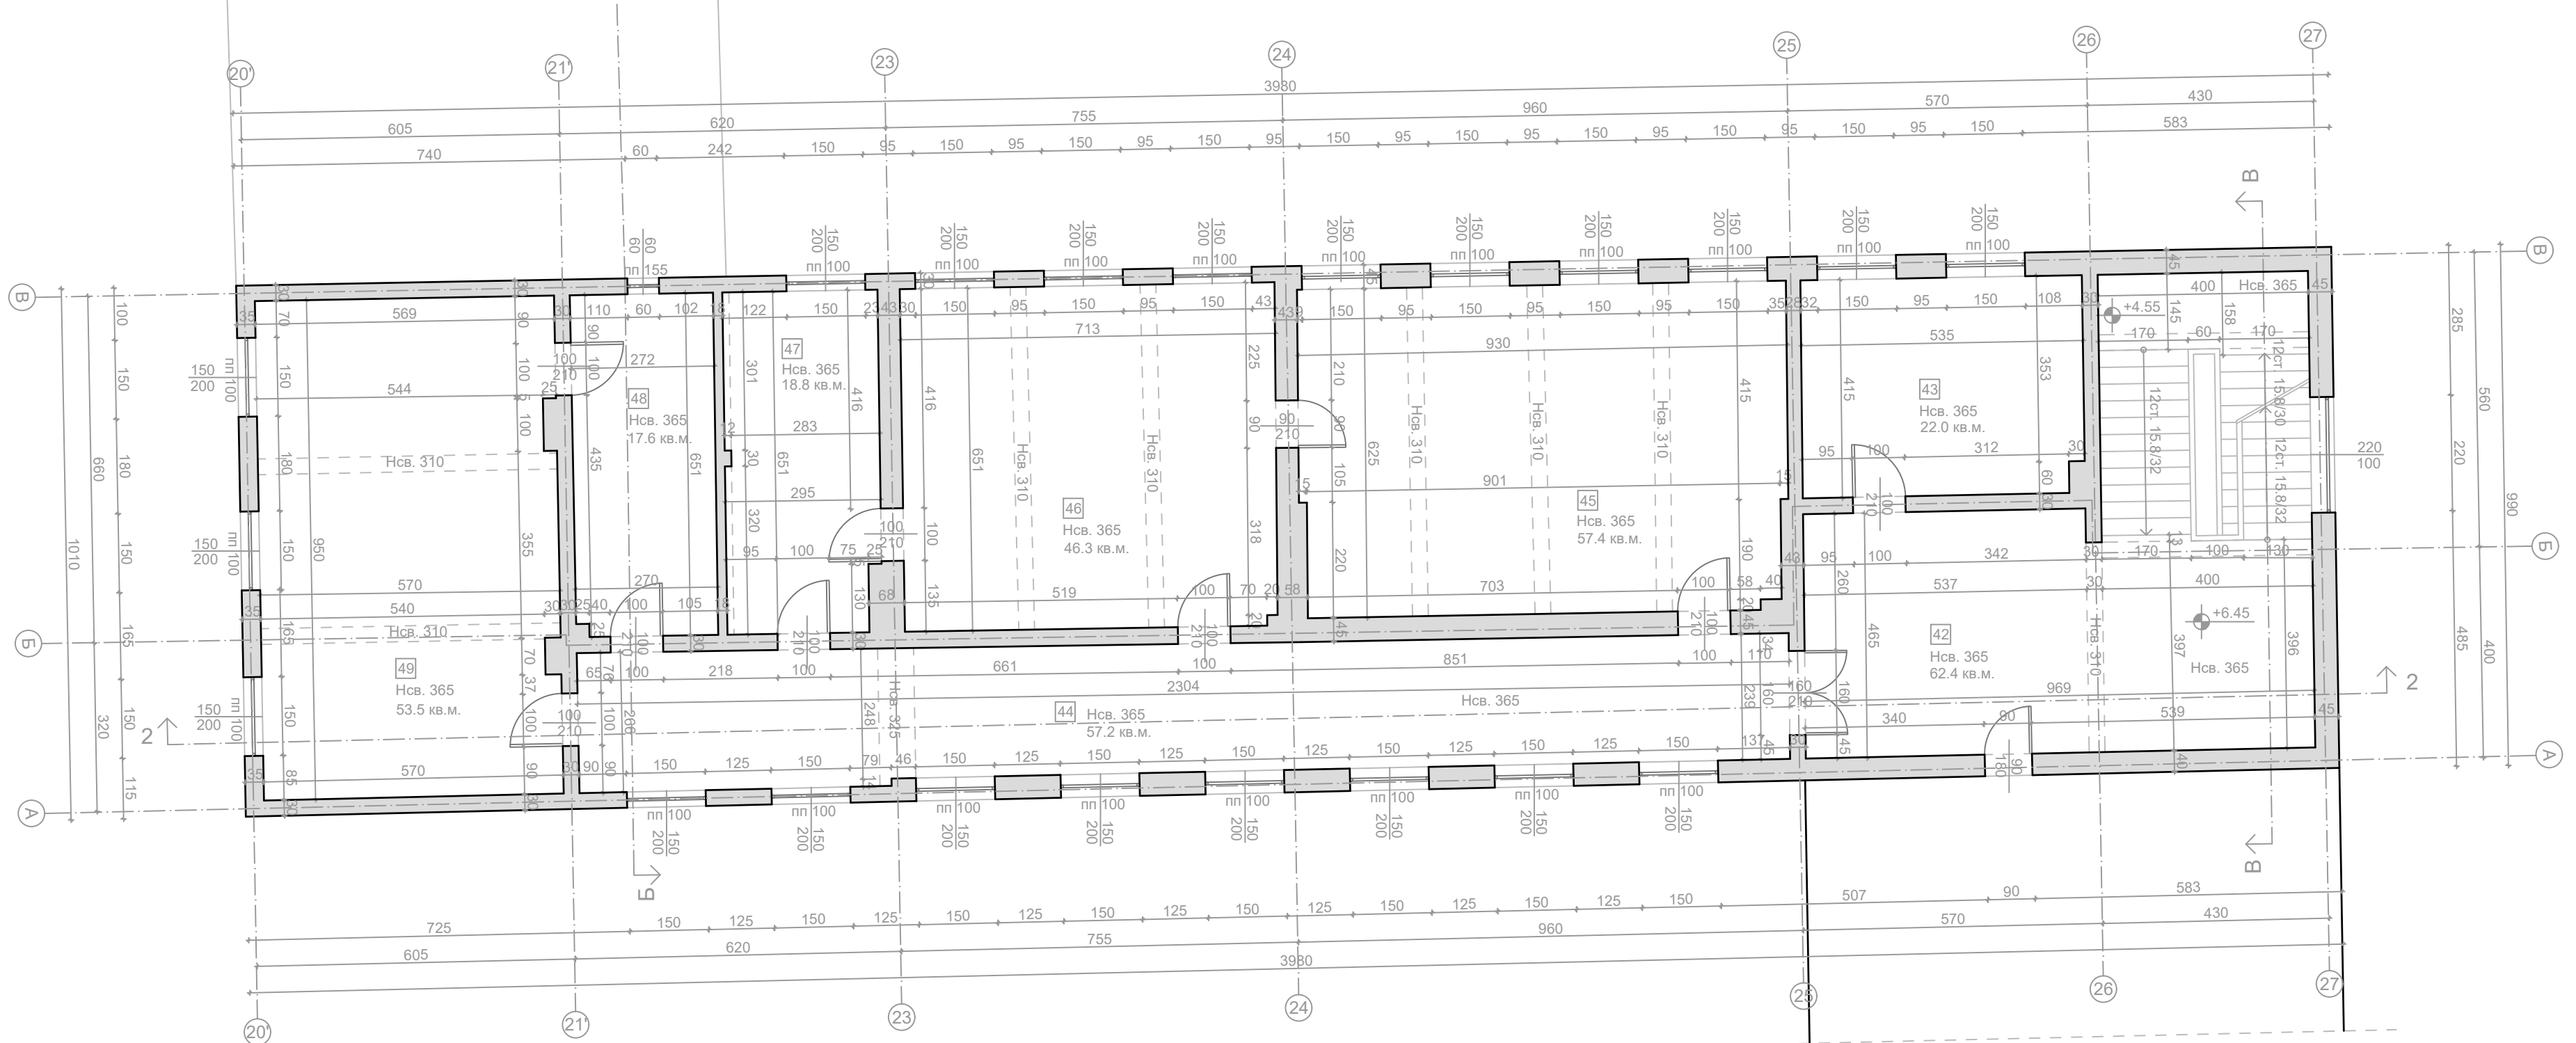

Тяло 2
План етаж +3
Кота +6.45

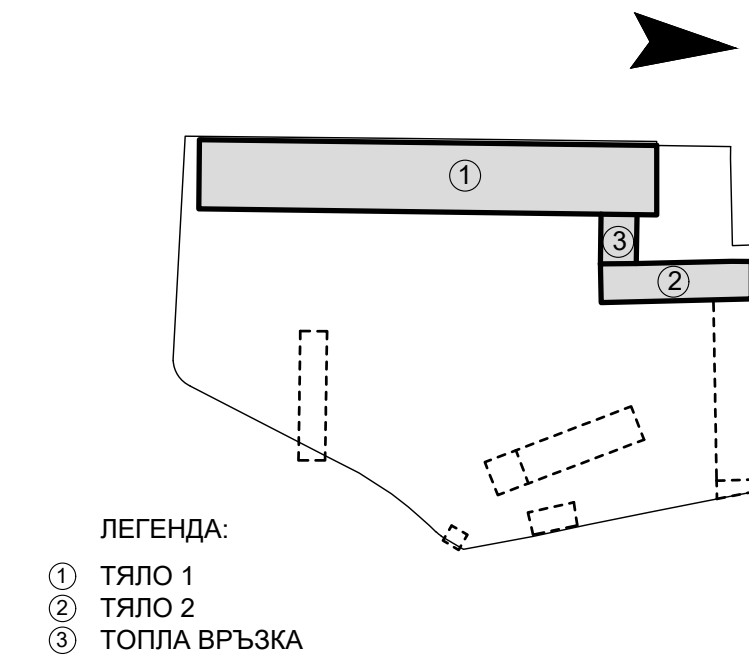

ЛЕГЕНДА:

1 ТЯЛО 1

2 ТЯЛО 2

3 ТОПЛА ВРЪЗКА

СИТУАЦИОННА СХЕМА

МАЩАБ: 1:2000

ТЯЛО 1 - 2200 м

ТЯЛО 2 - 2200 м

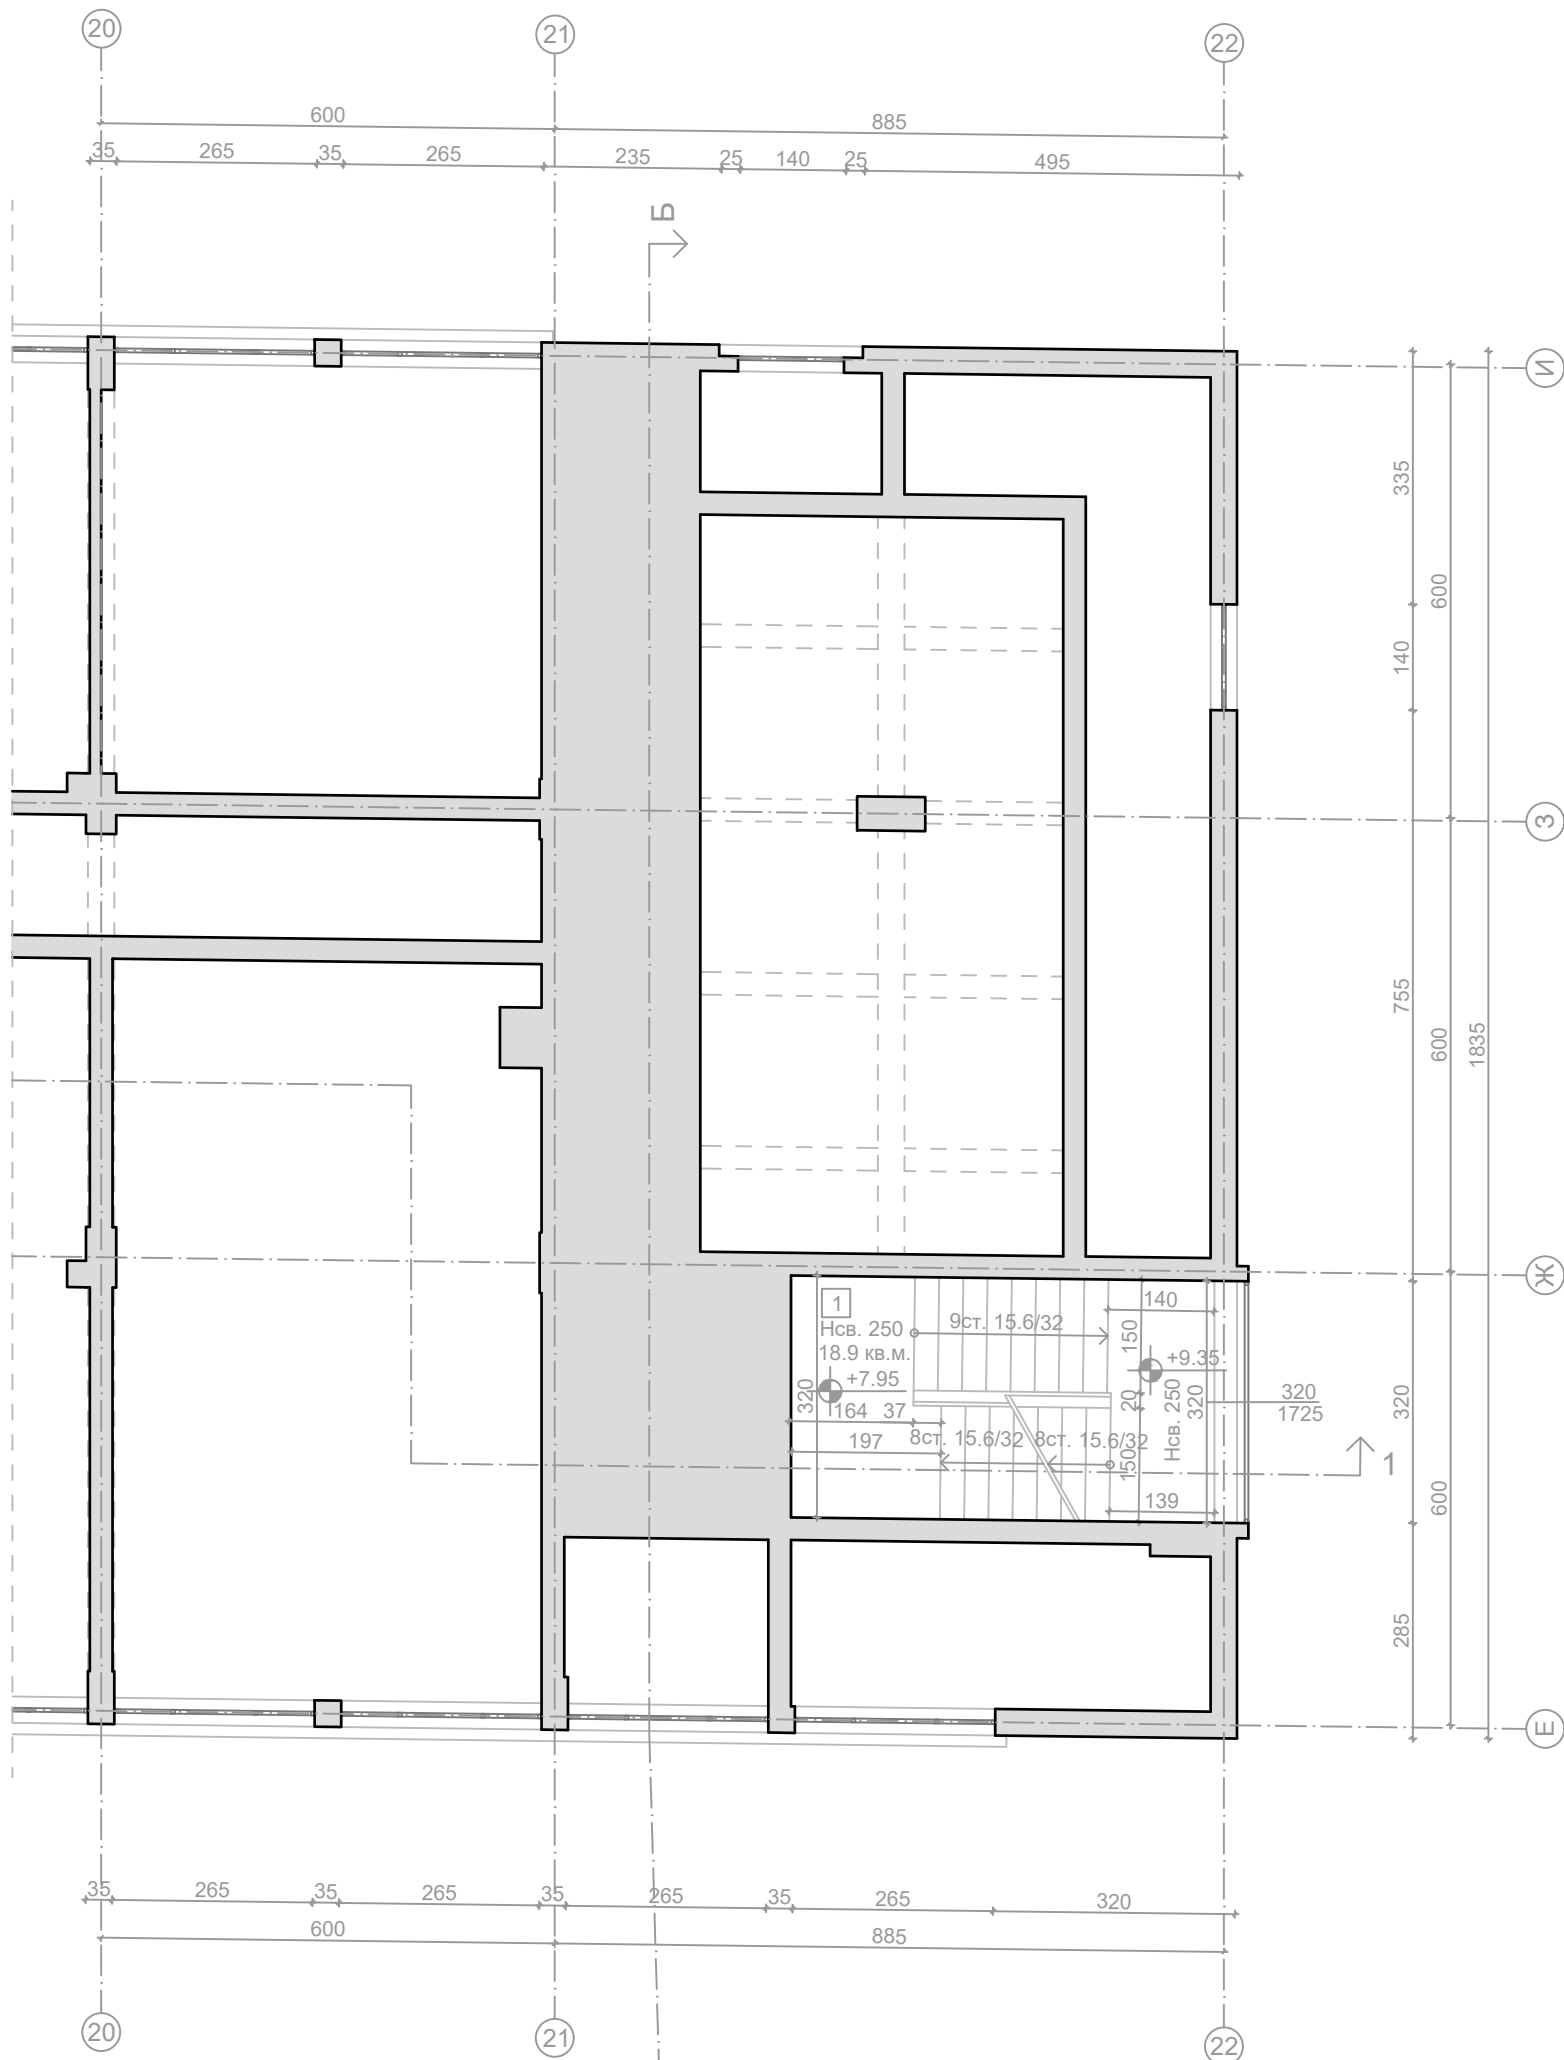

Тяло 2
План етаж +4
Кота +10.25

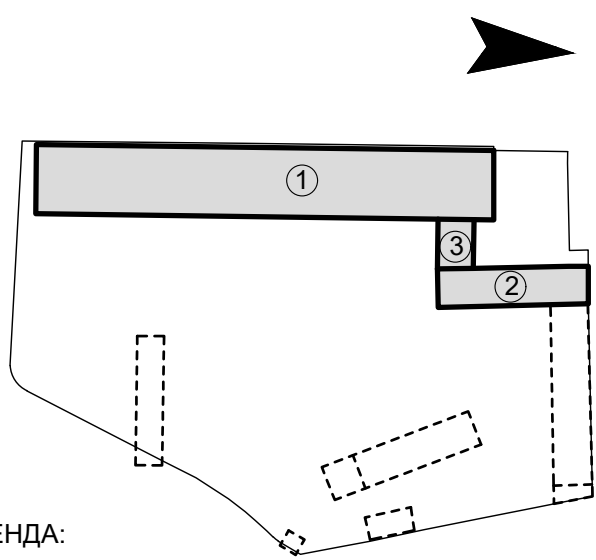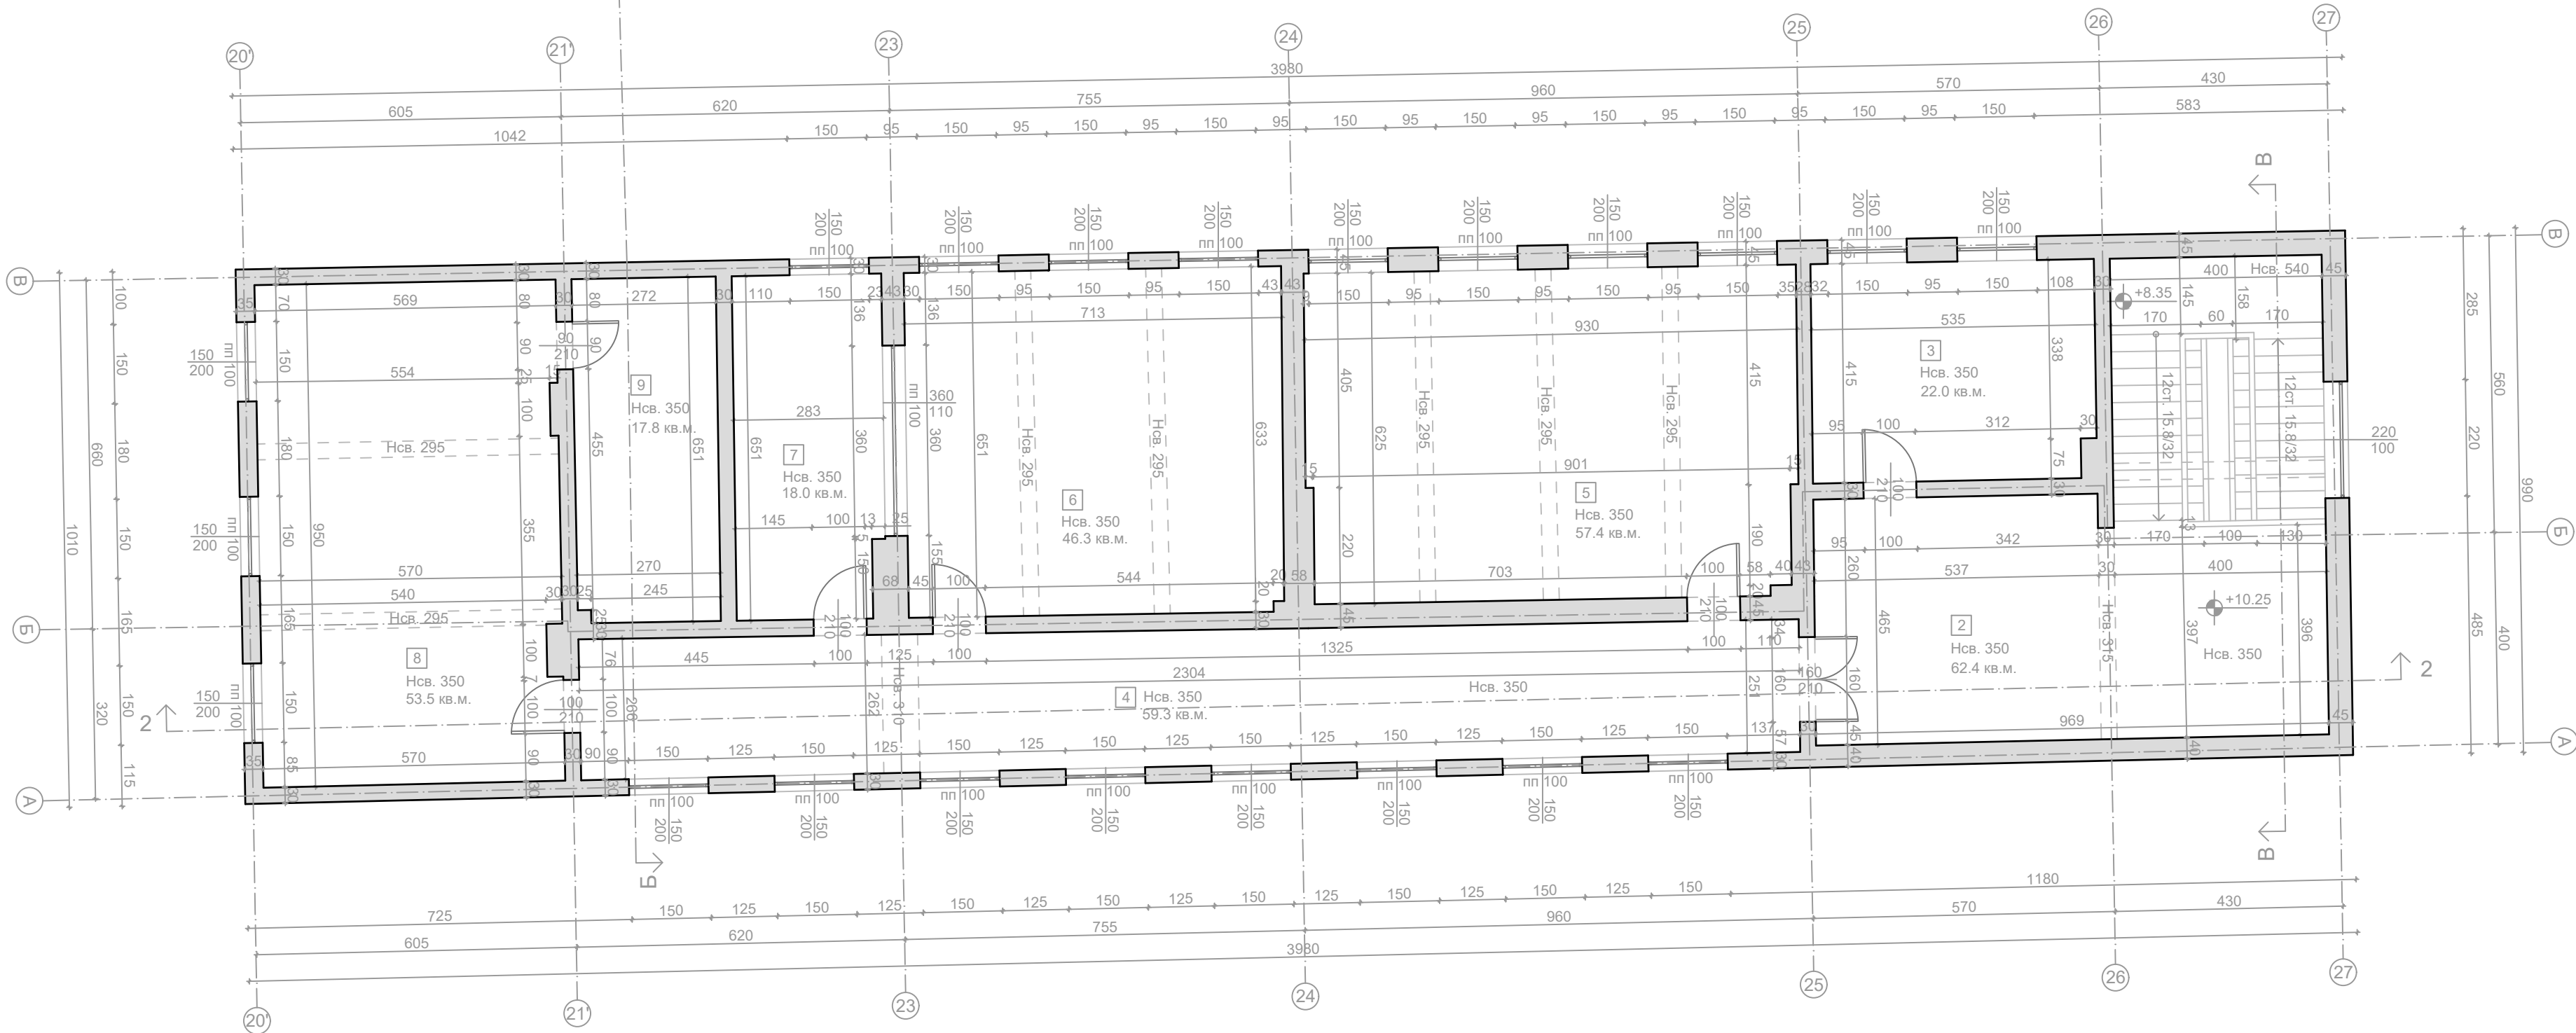

ЛЕГЕНДА:

- 1 ТЯЛО 1
- 2 ТЯЛО 2
- 3 ТОПЛА ВРЪЗКА

СИТУАЦИОННА СХЕМА

МАЩАБ: 1:2000

№	помещение	кв.м.	под	стени	таван
ТЯЛО 1					
1	стълбишна клетка	18.9	мозайка	мазилка	мазилка
ТЯЛО 2 - 398кв.м.					
2	ст. клетка и фойе	62.4	мозайка	мазилка	мазилка
3	стая	22.0	паркет	мазилка	мазилка
4	коридор	59.3	мозайка	мазилка	мазилка
5	стая	57.4	паркет	облицовка	мазилка
6	стая	46.3	паркет	мазилка	мазилка
7	стая	18.0	паркет	мазилка	мазилка
8	стая	17.8	паркет	мазилка	мазилка
9	стая	53.5	паркет	мазилка	мазилка

ПЕЧАТ НА ГЛАВНИЯ ПРОЕКТАНТ:

ВЪЗЛОЖИТЕЛ:

ОБЩИНА ГАБРОВО

ПОДПИС:

ОБЕКТ: Архитектурно заснемане на сградата на бившата
Професионална гимназия по текстил и моден дизайн

Разположение съгласно ПУП: УПИ II-за техникум по
текстил, квартал 111 по ПУП на ЦГЧ на гр. Габрово;
Разположение съгласно КККР: поземлен имот с
идентификатор 14218.504.402 по КККР на гр. Габрово;
Идентификатор на сграда: 14218.504.402.3

ЧЕРТЕЖ: ТЯЛО 1 КОТА +7.95
ТЯЛО 2 КОТА +10.25

ФАЗА: АРХИТЕКТУРНО ЗАСНЕМАНЕ


ГЛАВЕН ПРОЕКТАНТ: арх. Я. ПАНЕВ

СПЕЦИАЛНОСТ: СЪГЛАСУВАЛ: ПОДПИС:


Архитектура арх. Я. ПАНЕВ

ЧАСТ: Архитектура ДАТА: 2023г.


МАЩАБ: 1:100 ЛИСТ №: 8/25

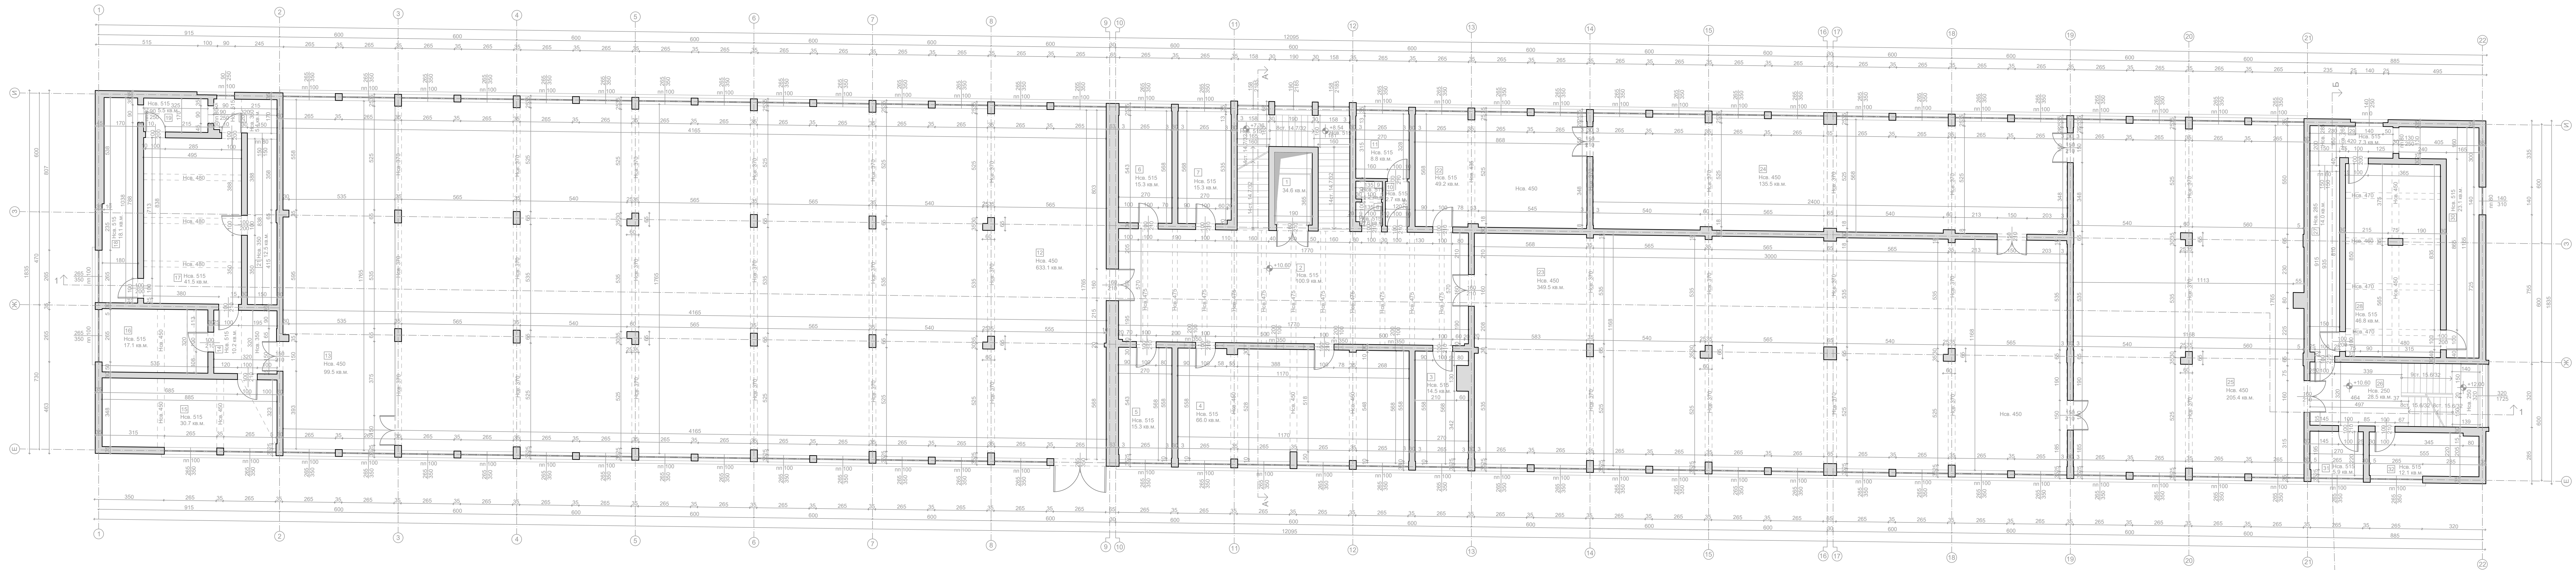

Тяло 1
План етаж +3
Кота +10.60

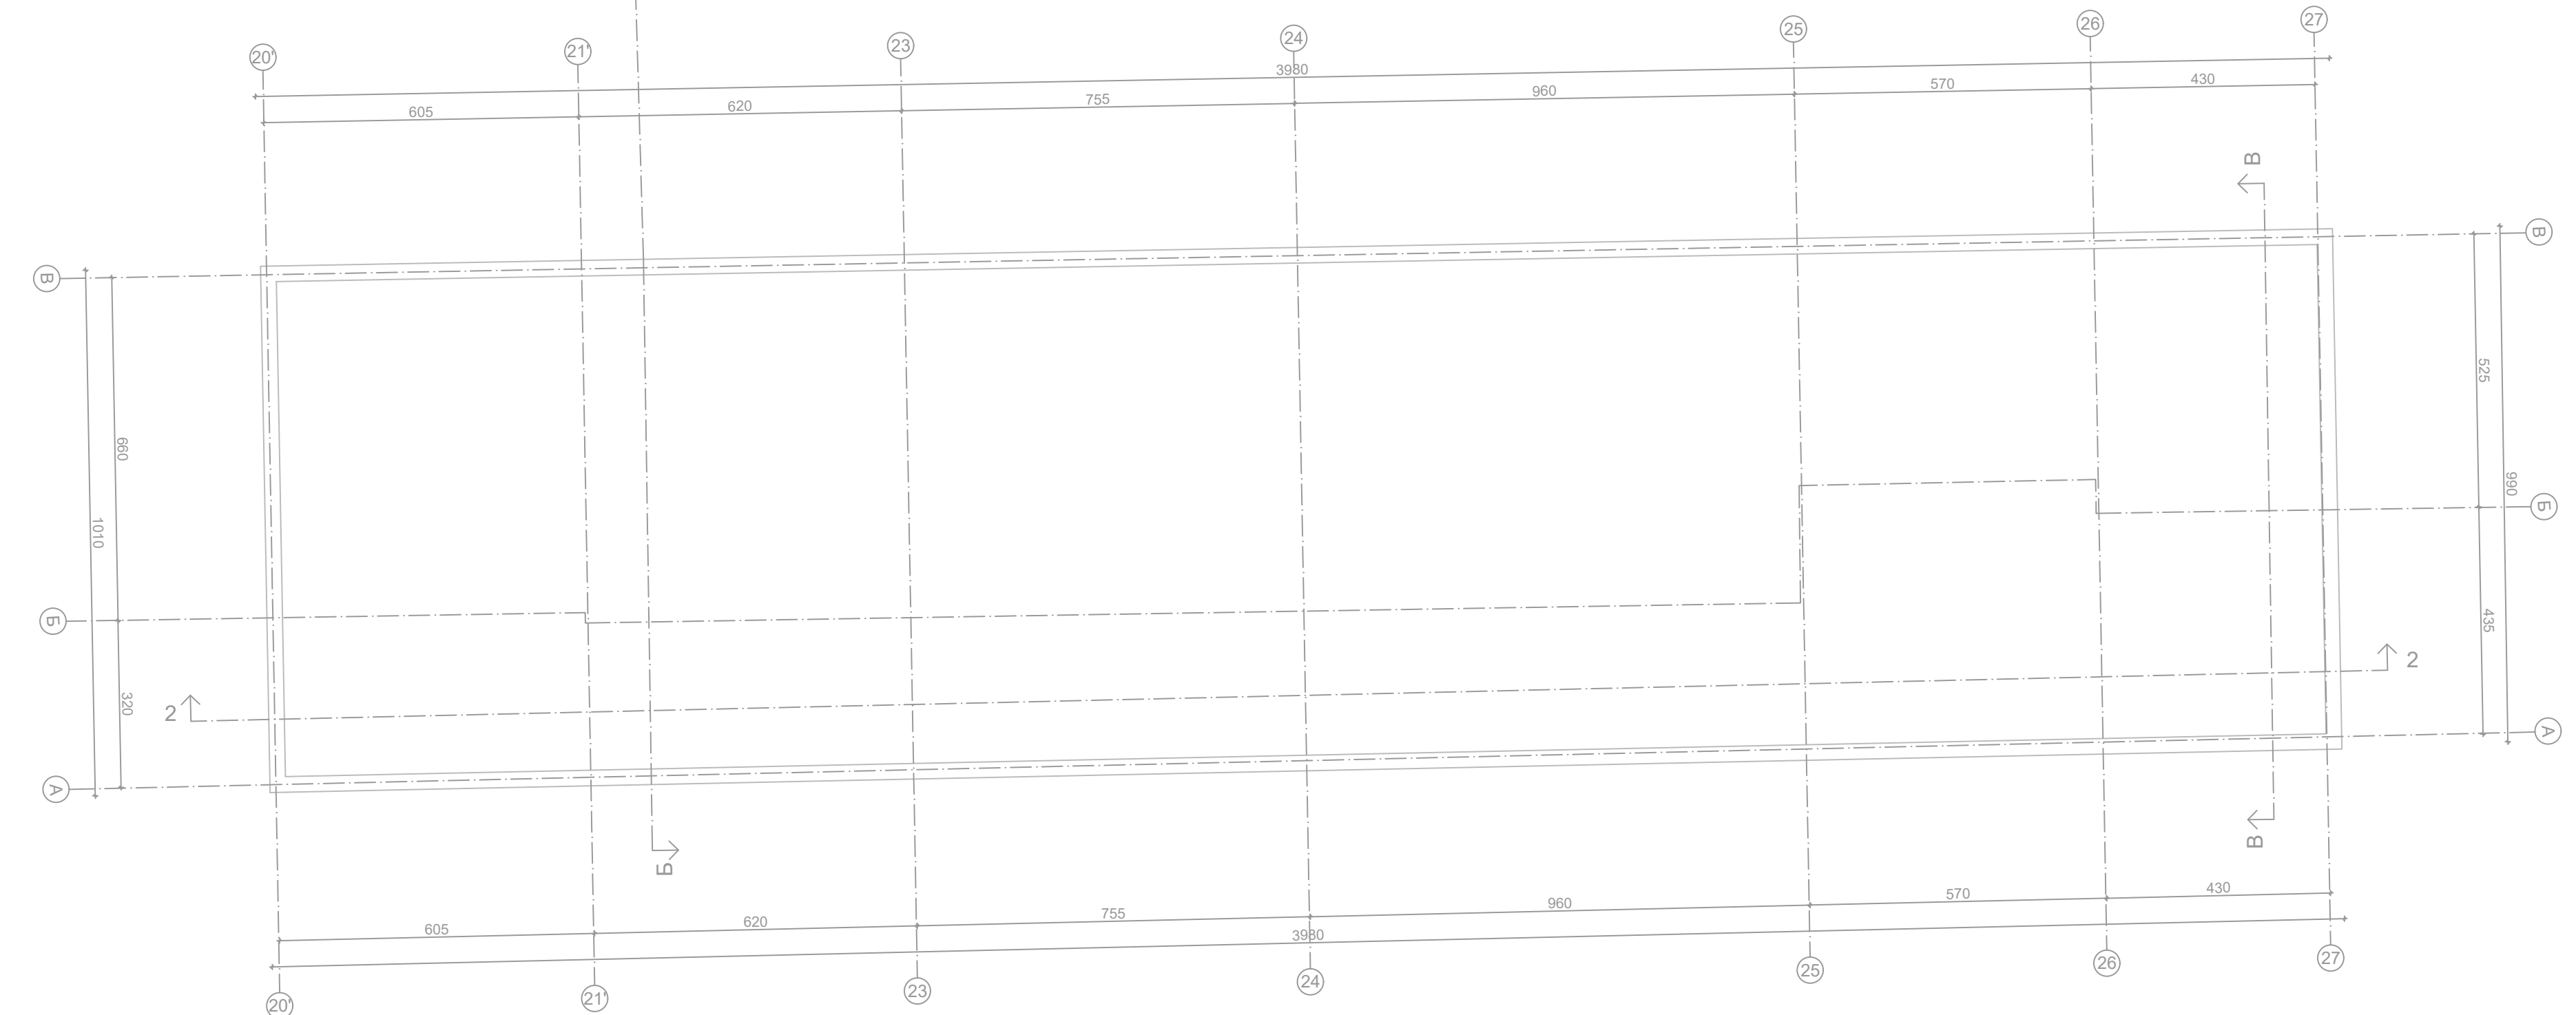

Тяло 2
План покрив
Кота +14.25

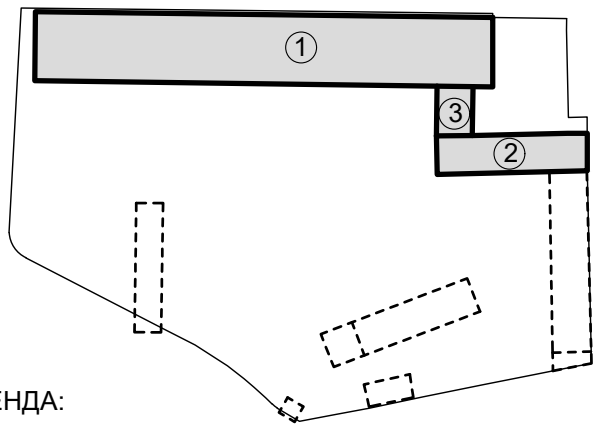

ЛЕГЕНДА:
1 ТЯЛО 1
2 ТЯЛО 2
3 ТОПЛА ВЪРЪКА

СИТУАЦИОННА СХЕМА		МАЩАБ: 1:2000			
№	ПОВЪРХОВИ	ВЪЗ.М.	ПОВ.	СТЕН	ПОКРИВ
19800 1:20000 м					
1	сградна площ	34.8	мащаб	мащаб	мащаб
2	фойе	100.9	мащаб	мащаб	мащаб
3	сан	24.5	мащаб	мащаб	мащаб
4	сан	85.5	мащаб	мащаб	мащаб
5	сан	15.3	мащаб	мащаб	мащаб
6	сан	15.3	мащаб	мащаб	мащаб
7	сан	15.3	мащаб	мащаб	мащаб
8	коридор	1.6	мащаб	мащаб	мащаб
9	коридор	1.2	мащаб	мащаб	мащаб
10	коридор	2.7	мащаб	мащаб	мащаб
11	коридор	5.8	мащаб	мащаб	мащаб
12	коридор	63.1	мащаб	мащаб	мащаб
13	коридор	8.5	мащаб	мащаб	мащаб
14	коридор	10.2	мащаб	мащаб	мащаб
15	сан	30.7	мащаб	мащаб	мащаб
16	сан	17.1	мащаб	мащаб	мащаб
17	коридор	41.5	мащаб	мащаб	мащаб
18	коридор	1.5	мащаб	мащаб	мащаб
19	коридор	5.5	мащаб	мащаб	мащаб
20	коридор	5.4	мащаб	мащаб	мащаб
21	коридор	5.3	мащаб	мащаб	мащаб
22	коридор	43.2	мащаб	мащаб	мащаб
23	коридор	46.5	мащаб	мащаб	мащаб
24	коридор	135.5	мащаб	мащаб	мащаб
25	коридор	205.4	мащаб	мащаб	мащаб
26	сградна площ	8.2	мащаб	мащаб	мащаб
27	коридор	14.5	мащаб	мащаб	мащаб
28	коридор	48.8	мащаб	мащаб	мащаб
29	коридор	1.3	мащаб	мащаб	мащаб
30	коридор	23.1	мащаб	мащаб	мащаб
31	сан	5.9	мащаб	мащаб	мащаб
32	сан	12.1	мащаб	мащаб	мащаб

ПЕЧАТ НА ГЛАВНИЯ ПРОЕКТАНТ:

ВЪЗЛОЖИТЕЛ:

ОБЩИНА ГАБРОВО

ПОДПИС:

ОБЕКТ: Архитектурно заснемане на сградата на бившата
Професионална гимназия по текстил и моден дизайн
Разположение: съгласно ПУП, УПИ II-за технически по
текстил, квартал 111 по ПУП на ЦГМ на гр. Габрово;
Разположение: съгласно ККОП: поминен имот с
идентификатор 14218.504.402 по ККОП на гр. Габрово;
Идентификатор на сграда: 14218.504.402.3

ЧЕРТЕЖ: ТЯЛО 1 КОТА +10.60
ТЯЛО 2 КОТА +14.25

ФАЗА: АРХИТЕКТУРНО ЗАСНЕМАНЕ

ГЛАВЕН ПРОЕКТАНТ: арх. Я. ПАНЕВ

СПЕЦИАЛНОСТ: СИГНАТУРА:


Архитектура арх. Я. ПАНЕВ

ЧАСТ: Архитектура


МАЩАБ: 1:100

ДАТА: 2023г.

ЛИСТ №: 9/25

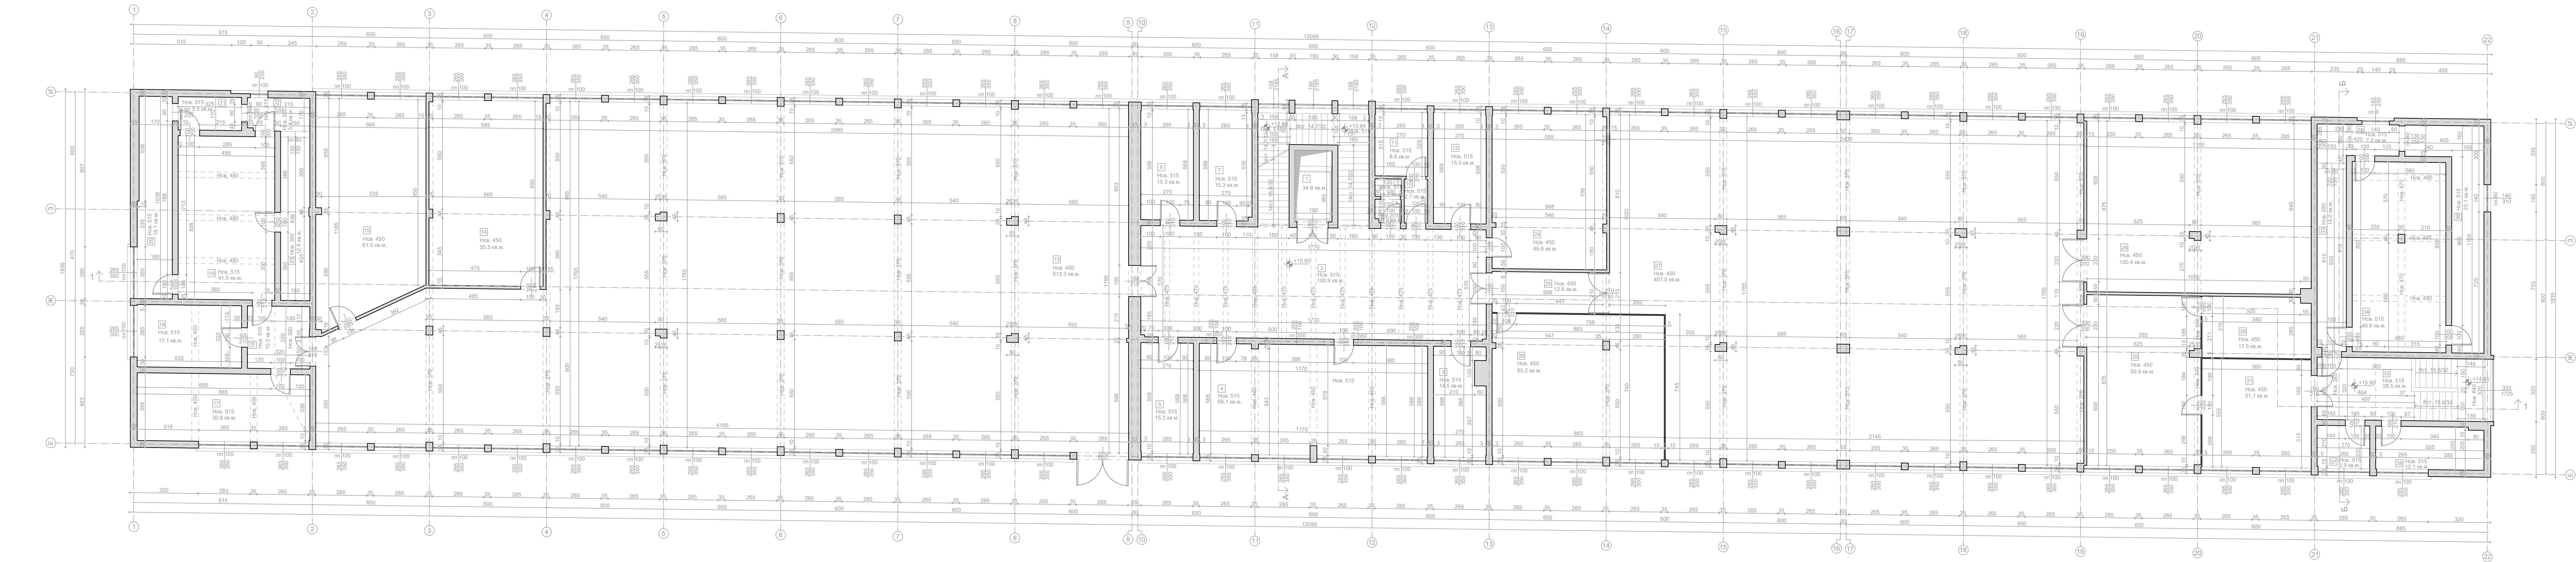

Тяло 1
План етаж 4
Кота +15.90

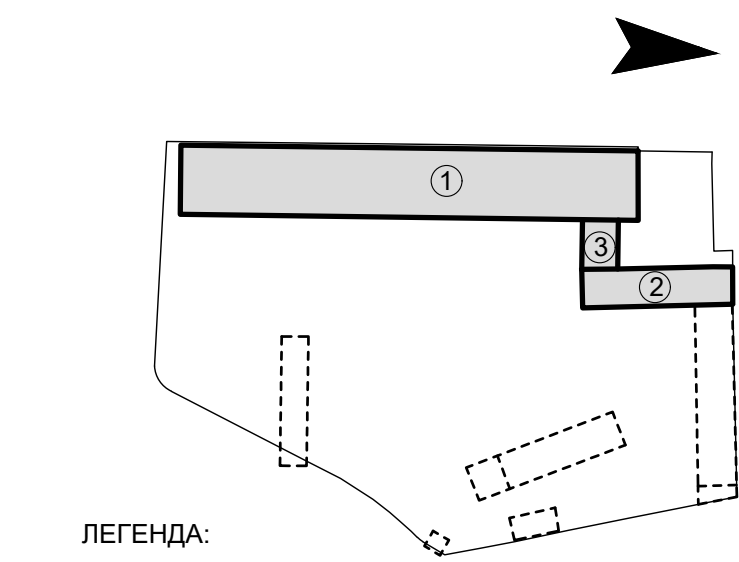

ЛЕГЕНДА:
1. ТЯЛО 1
2. ТЯЛО 2
3. ТОПЛА ВРЪЗКА

СИТУАЦИОННА СХЕМА
МАЩАБ: 1:2000

№	позоваване	кв. м.	под	стени	табани
ТЯЛО 1 - 2220 кв. м.					
1	стъпалови клетки	34.6	мозайка	мозайка	мозайка
2	коридор	102.9	мозайка	мозайка	мозайка
3	стая	14.5	мозайка	мозайка	мозайка
4	стая	65.1	паркет	мозайка	окочен таван
5	стая	15.3	мозайка	мозайка	мозайка
6	стая	15.3	багетур	мозайка	мозайка
7	стая	15.3	паркет	мозайка	мозайка
8	придаване	1.6	мозайка	мозайка	мозайка
9	тоалетна	1.2	мозайка	мозайка	мозайка
10	придаване	2.7	мозайка	мозайка	мозайка
11	тоалетна	8.8	мозайка	мозайка	мозайка
12	стая	15.3	мозайка	мозайка	мозайка
13	позоваване	613.3	мозайка	мозайка	мозайка
14	позоваване	56.8	мозайка	мозайка	мозайка
15	позоваване	61.0	мозайка	мозайка	мозайка
16	придаване	10.2	мозайка	мозайка	мозайка
17	стая	30.8	мозайка	мозайка	окочен таван
18	стая	17.1	мозайка	мозайка	окочен таван
19	техническо позоваване	41.5	бетонна настилка	мозайка	мозайка
20	техническо позоваване	18.1	бетонна настилка	мозайка	мозайка
21	техническо позоваване	5.5	бетонна настилка	мозайка	мозайка
22	техническо позоваване	5.4	бетонна настилка	мозайка	мозайка
23	техническо позоваване	12.3	бетонна настилка	мозайка	мозайка
24	стая	45.6	багетур	мозайка	окочен таван
25	коридор	12.6	мозайка	мозайка	мозайка
26	стая	65.2	мозайка	мозайка	мозайка
27	позоваване	407.0	мозайка	мозайка	мозайка
28	позоваване	100.4	мозайка	мозайка	мозайка
29	позоваване	50.9	мозайка	мозайка	мозайка
30	позоваване	17.5	мозайка	мозайка	мозайка
31	позоваване	31.1	мозайка	мозайка	мозайка
32	стъпалови клетки	28.5	мозайка	мозайка	мозайка
33	техническо позоваване	14.0	бетонна настилка	мозайка	мозайка
34	техническо позоваване	45.8	бетонна настилка	мозайка	мозайка
35	техническо позоваване	7.3	бетонна настилка	мозайка	мозайка
36	техническо позоваване	23.1	бетонна настилка	мозайка	мозайка
37	стая	5.0	багетур	мозайка	мозайка
38	стая	12.1	мозайка	мозайка	мозайка

ПЕЧАТ НА ГЛАВНИЯ ПРОЕКТАНТ:

ВЪЗЛОЖИТЕЛ: ОБЩИНА ГАБРОВО

ОБЕКТ: Архитектурно заснемане на сградата на бившата
Професионална гимназия по текстил и моден дизайн
Разположение съгласно ПУП: УПИ II-за техникум по
текстил, квартал 111 по ПУП на ЦГЧ на гр. Габрово.
Разположение съгласно КККР: поземлен имот с
идентификатор 14218.504.402 по КККР на гр. Габрово;
Идентификатор на сграда: 14218.504.402.3

ЧЕРТЕЖ: ТЯЛО 1 КОТА +15.90


ФАЗА: АРХИТЕКТУРНО ЗАСНЕМАНЕ

ГЛАВЕН ПРОЕКТАНТ: арх. Я. ПАНЕВ


СПЕЦИАЛНОСТ: СЪГЛАСУВАЛ: ПОДПИС:

Архитектура арх. Я. ПАНЕВ

ЧАСТ: Архитектура ДАТА: 2023г.
МАЩАБ: 1:100 ЛИСТ №: 11/25

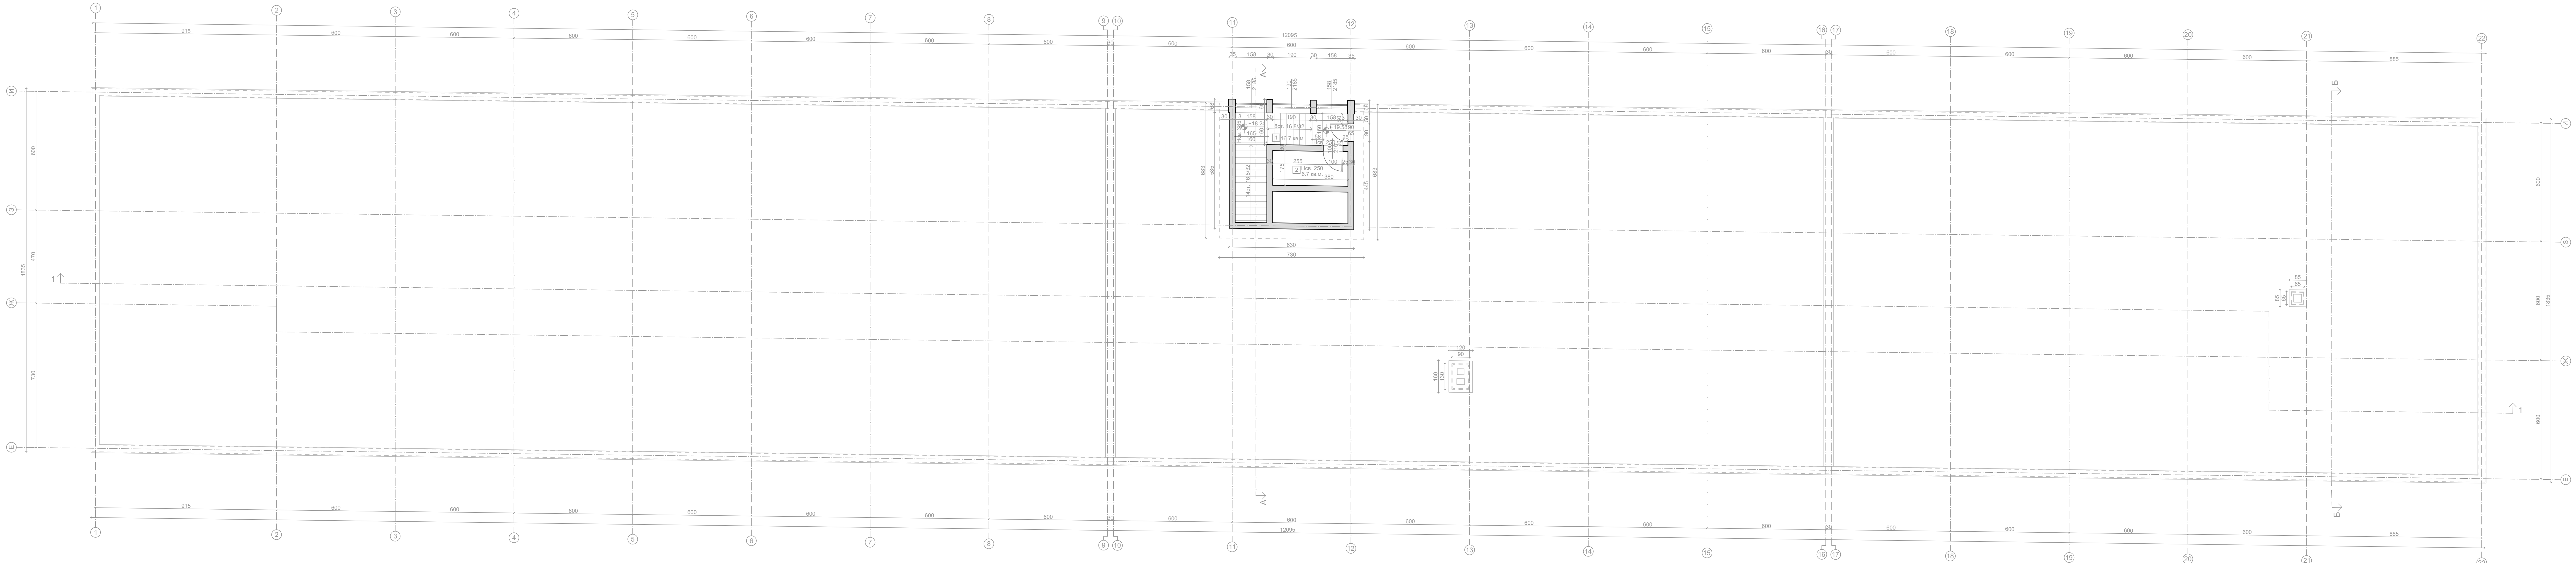

Тяло 1
План покрив
Кота +21.50

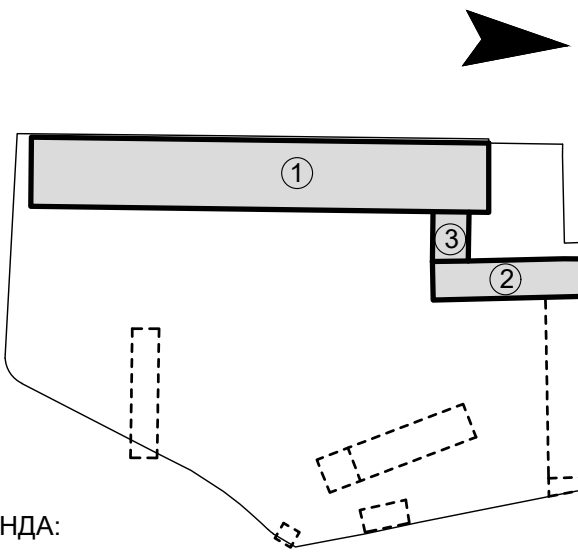

- ЛЕГЕНДА:
① ТЯЛО 1
② ТЯЛО 2
③ ТОПЛА БРЪЗКА

СИТУАЦИОННА СХЕМА

МАЩАБ: 1:2000

№	позоваване	на м.	под.	стени	таван
---	------------	-------	------	-------	-------

1	стъпаловна клетка	16.7	человна	человна	человна
---	-------------------	------	---------	---------	---------

2	периметрична конструкция	6.7	бетонна конструкция	человна	человна
---	--------------------------	-----	---------------------	---------	---------

ПЕЧАТ НА ГЛАВНИЯ ПРОЕКТАНТ:

ВЪЗЛОЖИТЕЛ:

ПОДПИС:

ОБЩИНА ГАБРОВО

ОБЕКТ: Архитектурно заснемане на сградата на бившата
Професионална гимназия по текстил и моден дизайн
Разположение съгласно ПЛП: УПИ II-за техникум по
текстил, квартал 111 по ПУП на ЦГЧ на гр. Габрово;
Разположение съгласно ККР: поземлен имот с
идентификатор 14218.504.402 по ККР на гр. Габрово;
Идентификатор на сграда: 14218.504.402.3

ЧЕРТЕЖ: ТЯЛО 1 КОТА +21.50

ФАЗА: АРХИТЕКТУРНО ЗАСНЕМАНЕ

ГЛАВЕН ПРОЕКТАНТ: арх. Я. ПАНЕВ

СПЕЦИАЛНОСТ: АРХИТЕКТУРА

СЪГЛАСУВАЛ: арх. Я. ПАНЕВ

ЧАСТ: Архитектура


МАЩАБ: 1:100

ДАТА: 2023г.

ЛИСТ №: 12/25



Разрез 1-1

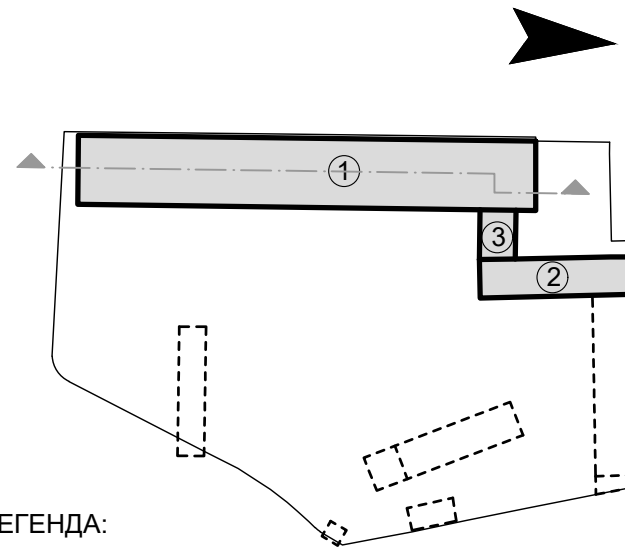

ЛЕГЕНДА:
1 ТЯЛО 1
2 ТЯЛО 2
3 ТОПЛА ВРЪЗКА

СИТУАЦИОННА СХЕМА МАЩАБ: 1:2000

ПЕЧАТ НА ГЛАВНИЯ ПРОЕКТАНТ:



ВЪЗЛОЖИТЕЛ:

ОБЩИНА ГАБРОВО

ОБЕКТ: Архитектурно заснемане на сградата на бившата
Професионална гимназия по текстил и моден дизайн
Разположение съгласно ПУП: УПИ II-за техникум по
текстил, квартал 111 по ПУП на ЦГЧ на гр. Габрово;
Разположение съгласно ККР: поземлен имот с
идентификатор 14218.504.402 по ККР на гр. Габрово;
Идентификатор на сграда: 14218.504.402.3

ЧЕРТЕЖ: РАЗРЕЗ 1-1

ФАЗА: АРХИТЕКТУРНО ЗАСНЕМАНЕ		
ГЛАВЕН ПРОЕКТАНТ:	арх. Я. ПАНЕВ	
СПЕЦИАЛНОСТ:	СЪГЛАСУВАЛ:	ПОДПИС:
Архитектура	арх. Я. ПАНЕВ	
ЧАСТ: Архитектура	ДАТА: 2023г.	
МАЩАБ: 1:100	ЛИСТ №:	13/25

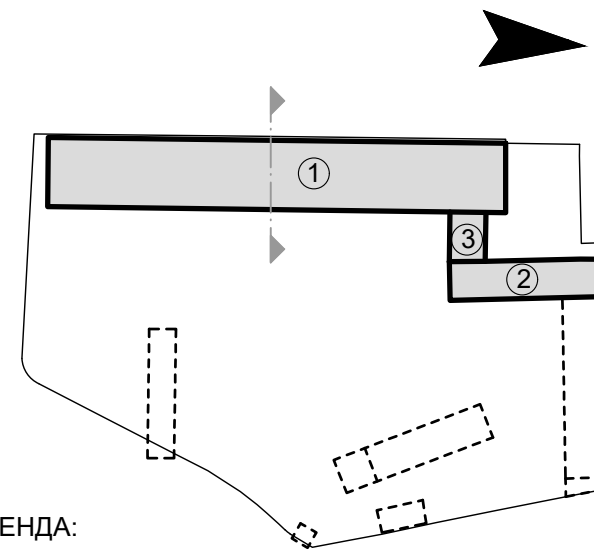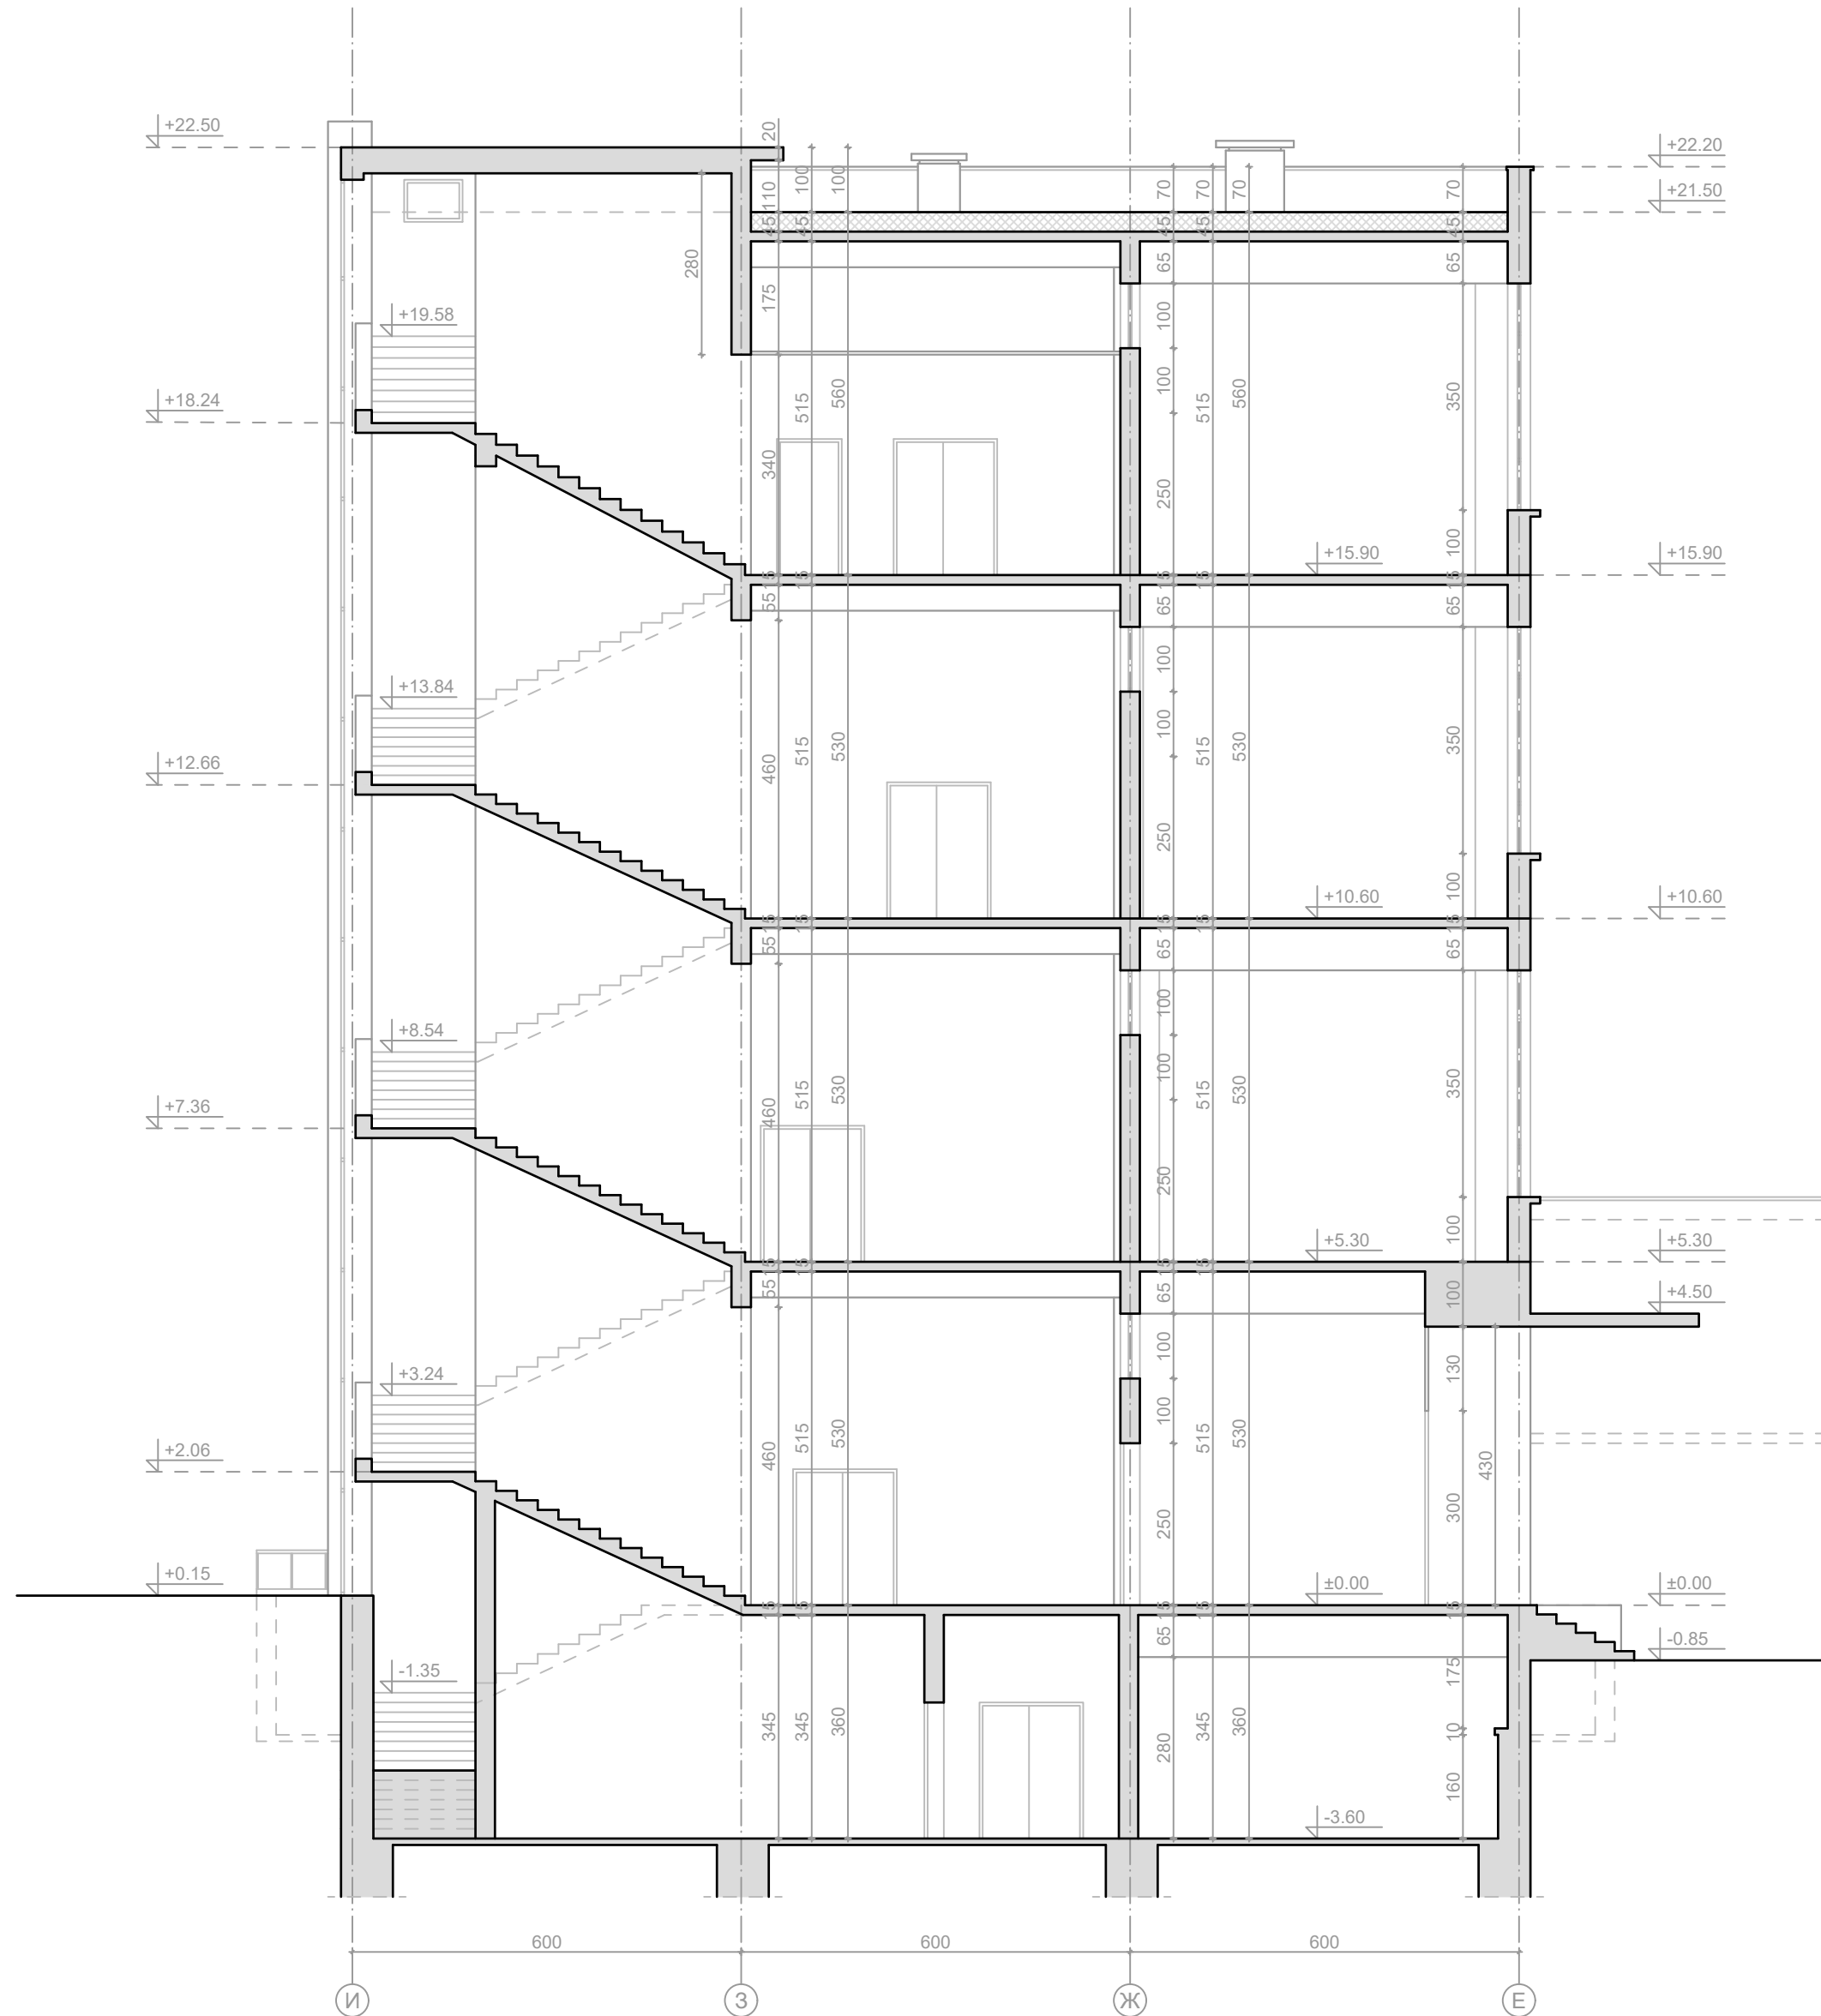

ЛЕГЕНДА:

- ① ТЯЛО 1
② ТЯЛО 2
③ ТОПЛА ВРЪЗКА

СИТУАЦИОННА СХЕМА

МАЩАБ: 1:2000

ПЕЧАТ НА ГЛАВНИЯ ПРОЕКТАНТ:

ВЪЗЛОЖИТЕЛ:

ПОДПИС:

ОБЩИНА ГАБРОВО

ОБЕКТ: Архитектурно заснемане на сградата на бившата
Професионална гимназия по текстил и моден дизайн

Разположение съгласно ПУП: УПИ II-за техникум по
текстил, квартал 111 по ПУП на ЦГЧ на гр. Габрово;
Разположение съгласно КККР: поземлен имот с
идентификатор 14218.504.402 по КККР на гр. Габрово;
Идентификатор на сграда: 14218.504.402.3

ЧЕРТЕЖ:

РАЗРЕЗ А-А

ФАЗА: АРХИТЕКТУРНО ЗАСНЕМАНЕ

ГЛАВЕН ПРОЕКТАНТ: арх. Я. ПАНЕВ

СПЕЦИАЛНОСТ: СЪГЛАСУВАЛ:

ПОДПИС:

Архитектура арх. Я. ПАНЕВ


ЧАСТ: Архитектура

ДАТА: 2023г.


МАЩАБ: 1:100

ЛИСТ № : 14/25

Разрез А-А

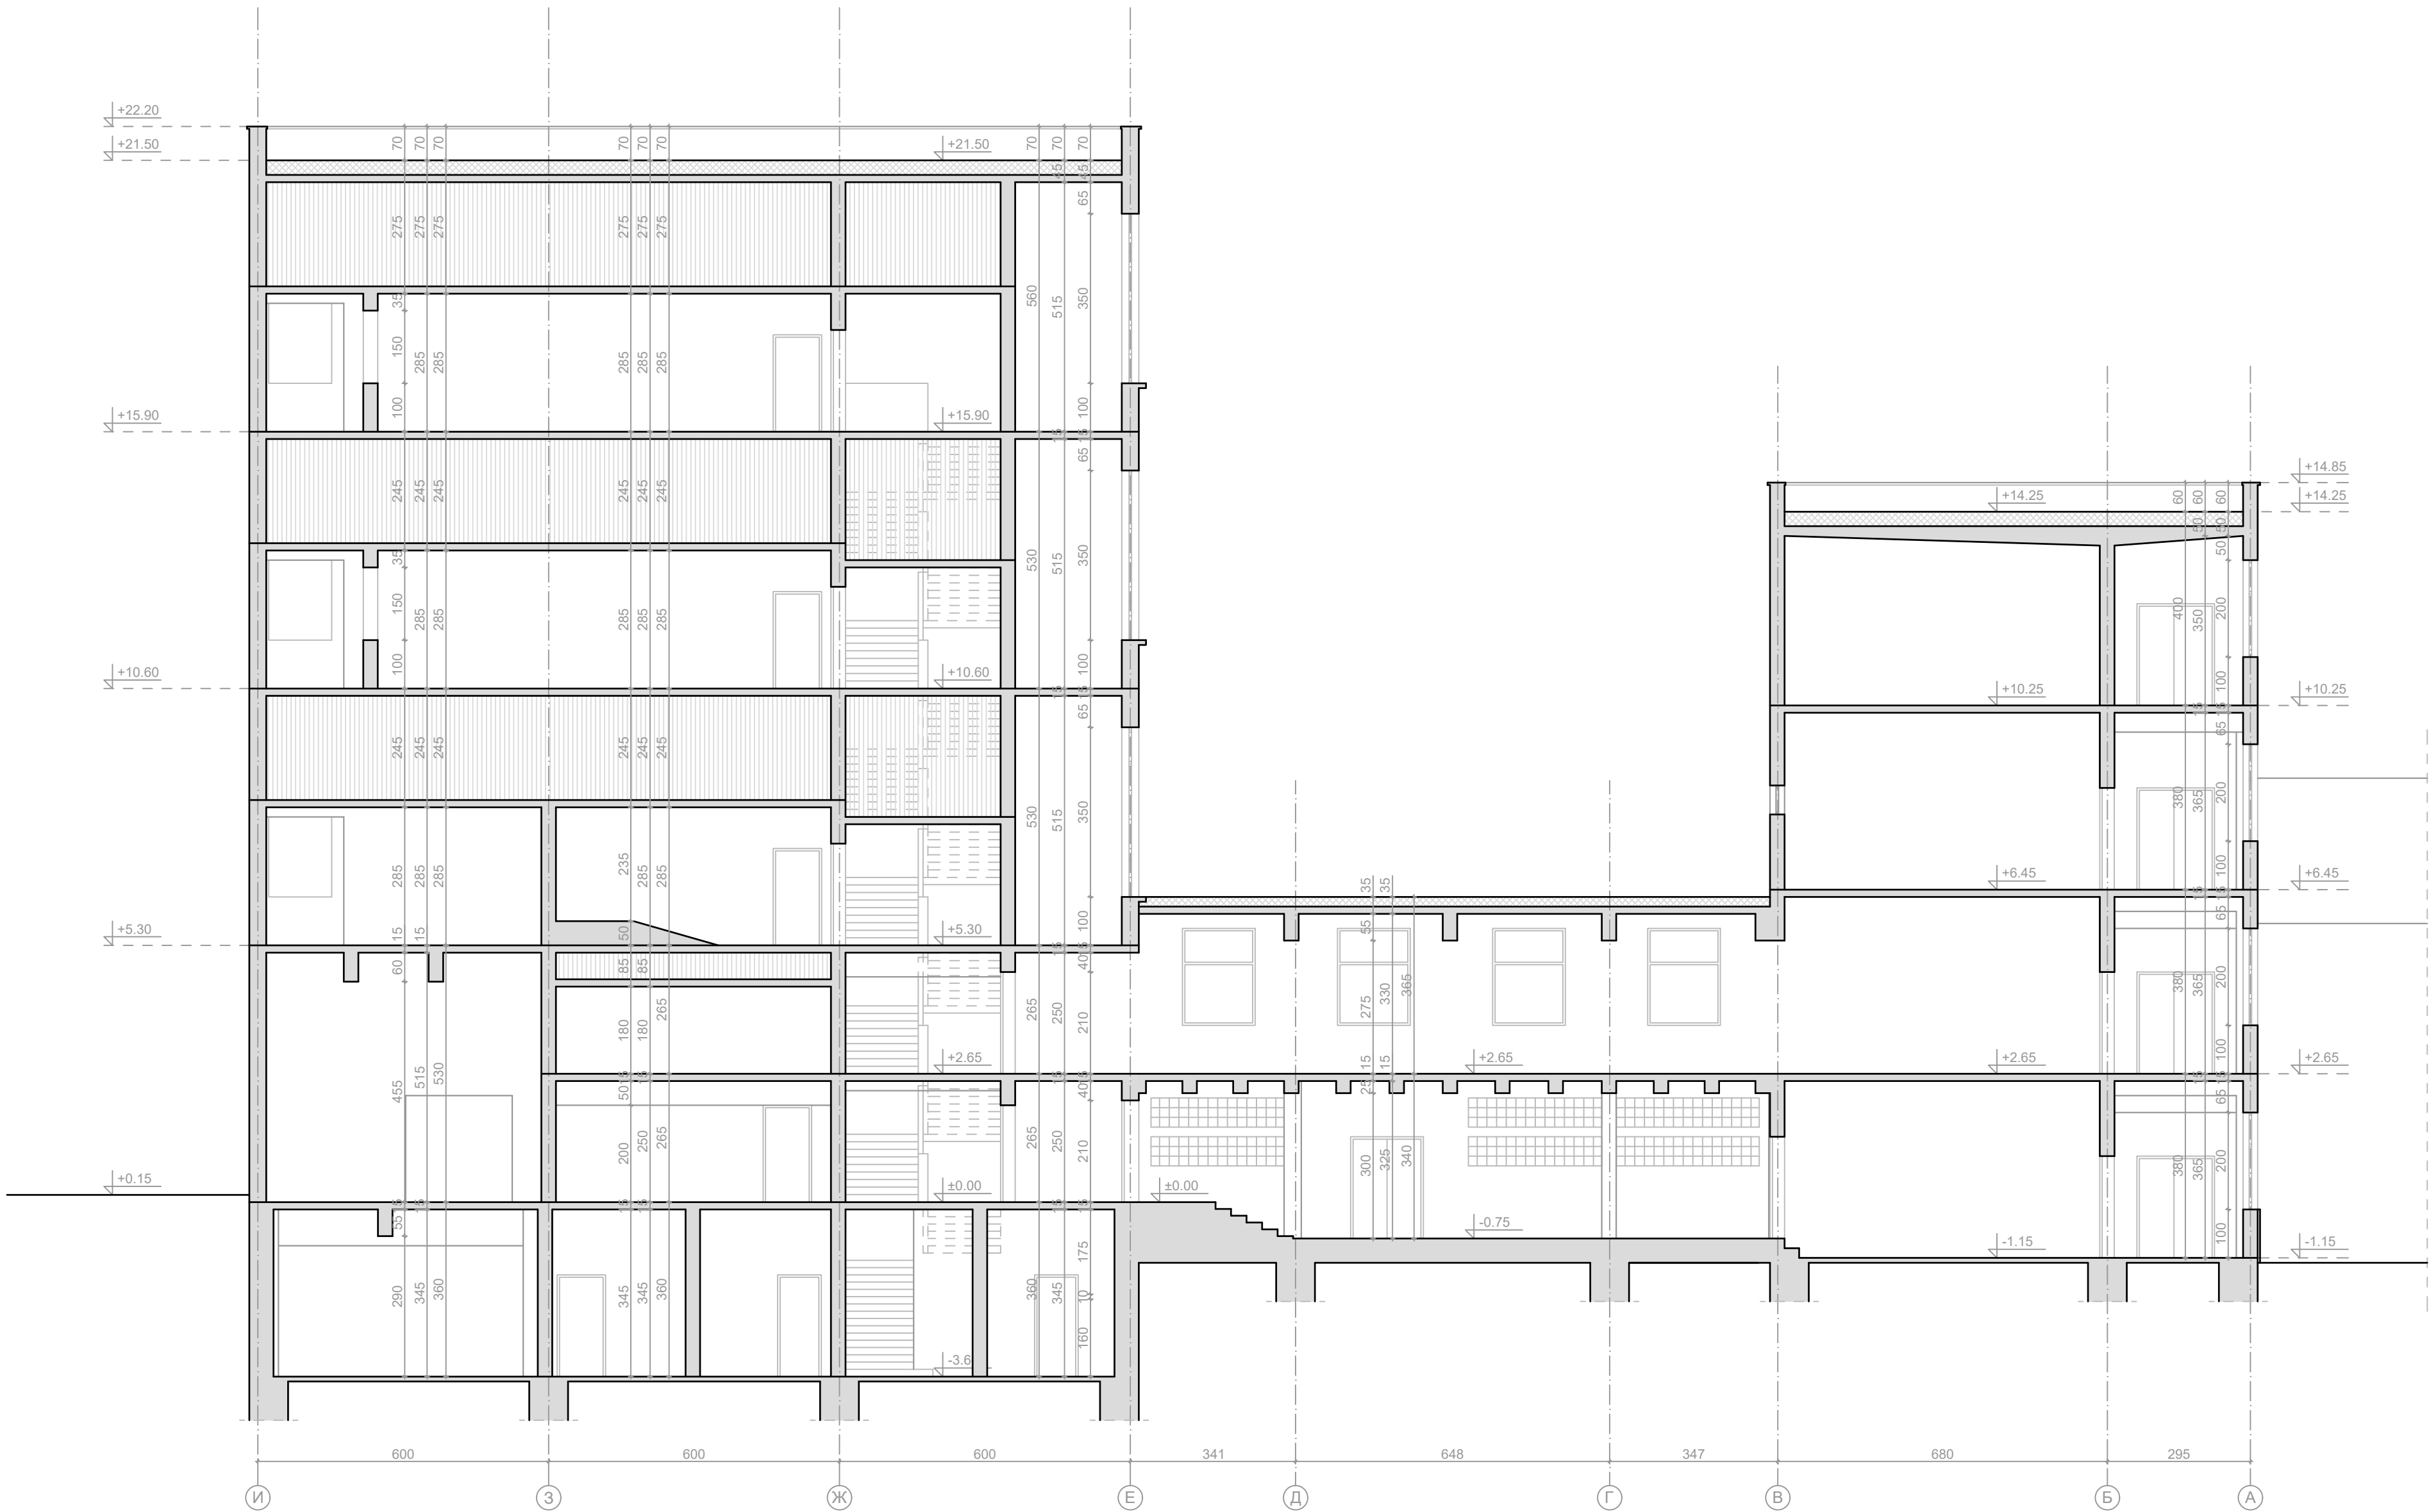


Разрез Б-Б

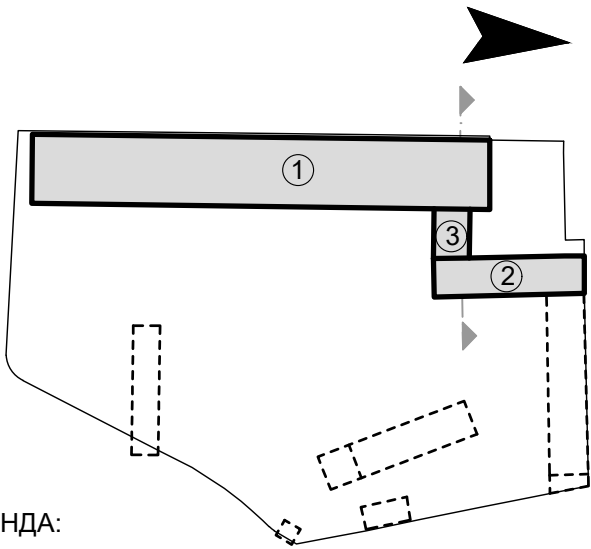


- ЛЕГЕНДА:
- ① ТЯЛО 1
 - ② ТЯЛО 2
 - ③ ТОПЛА ВРЪЗКА

СИТУАЦИОННА СХЕМА		МАЩАБ: 1:2000	
ПЕЧАТ НА ГЛАВНИЯ ПРОЕКТАНТ:			

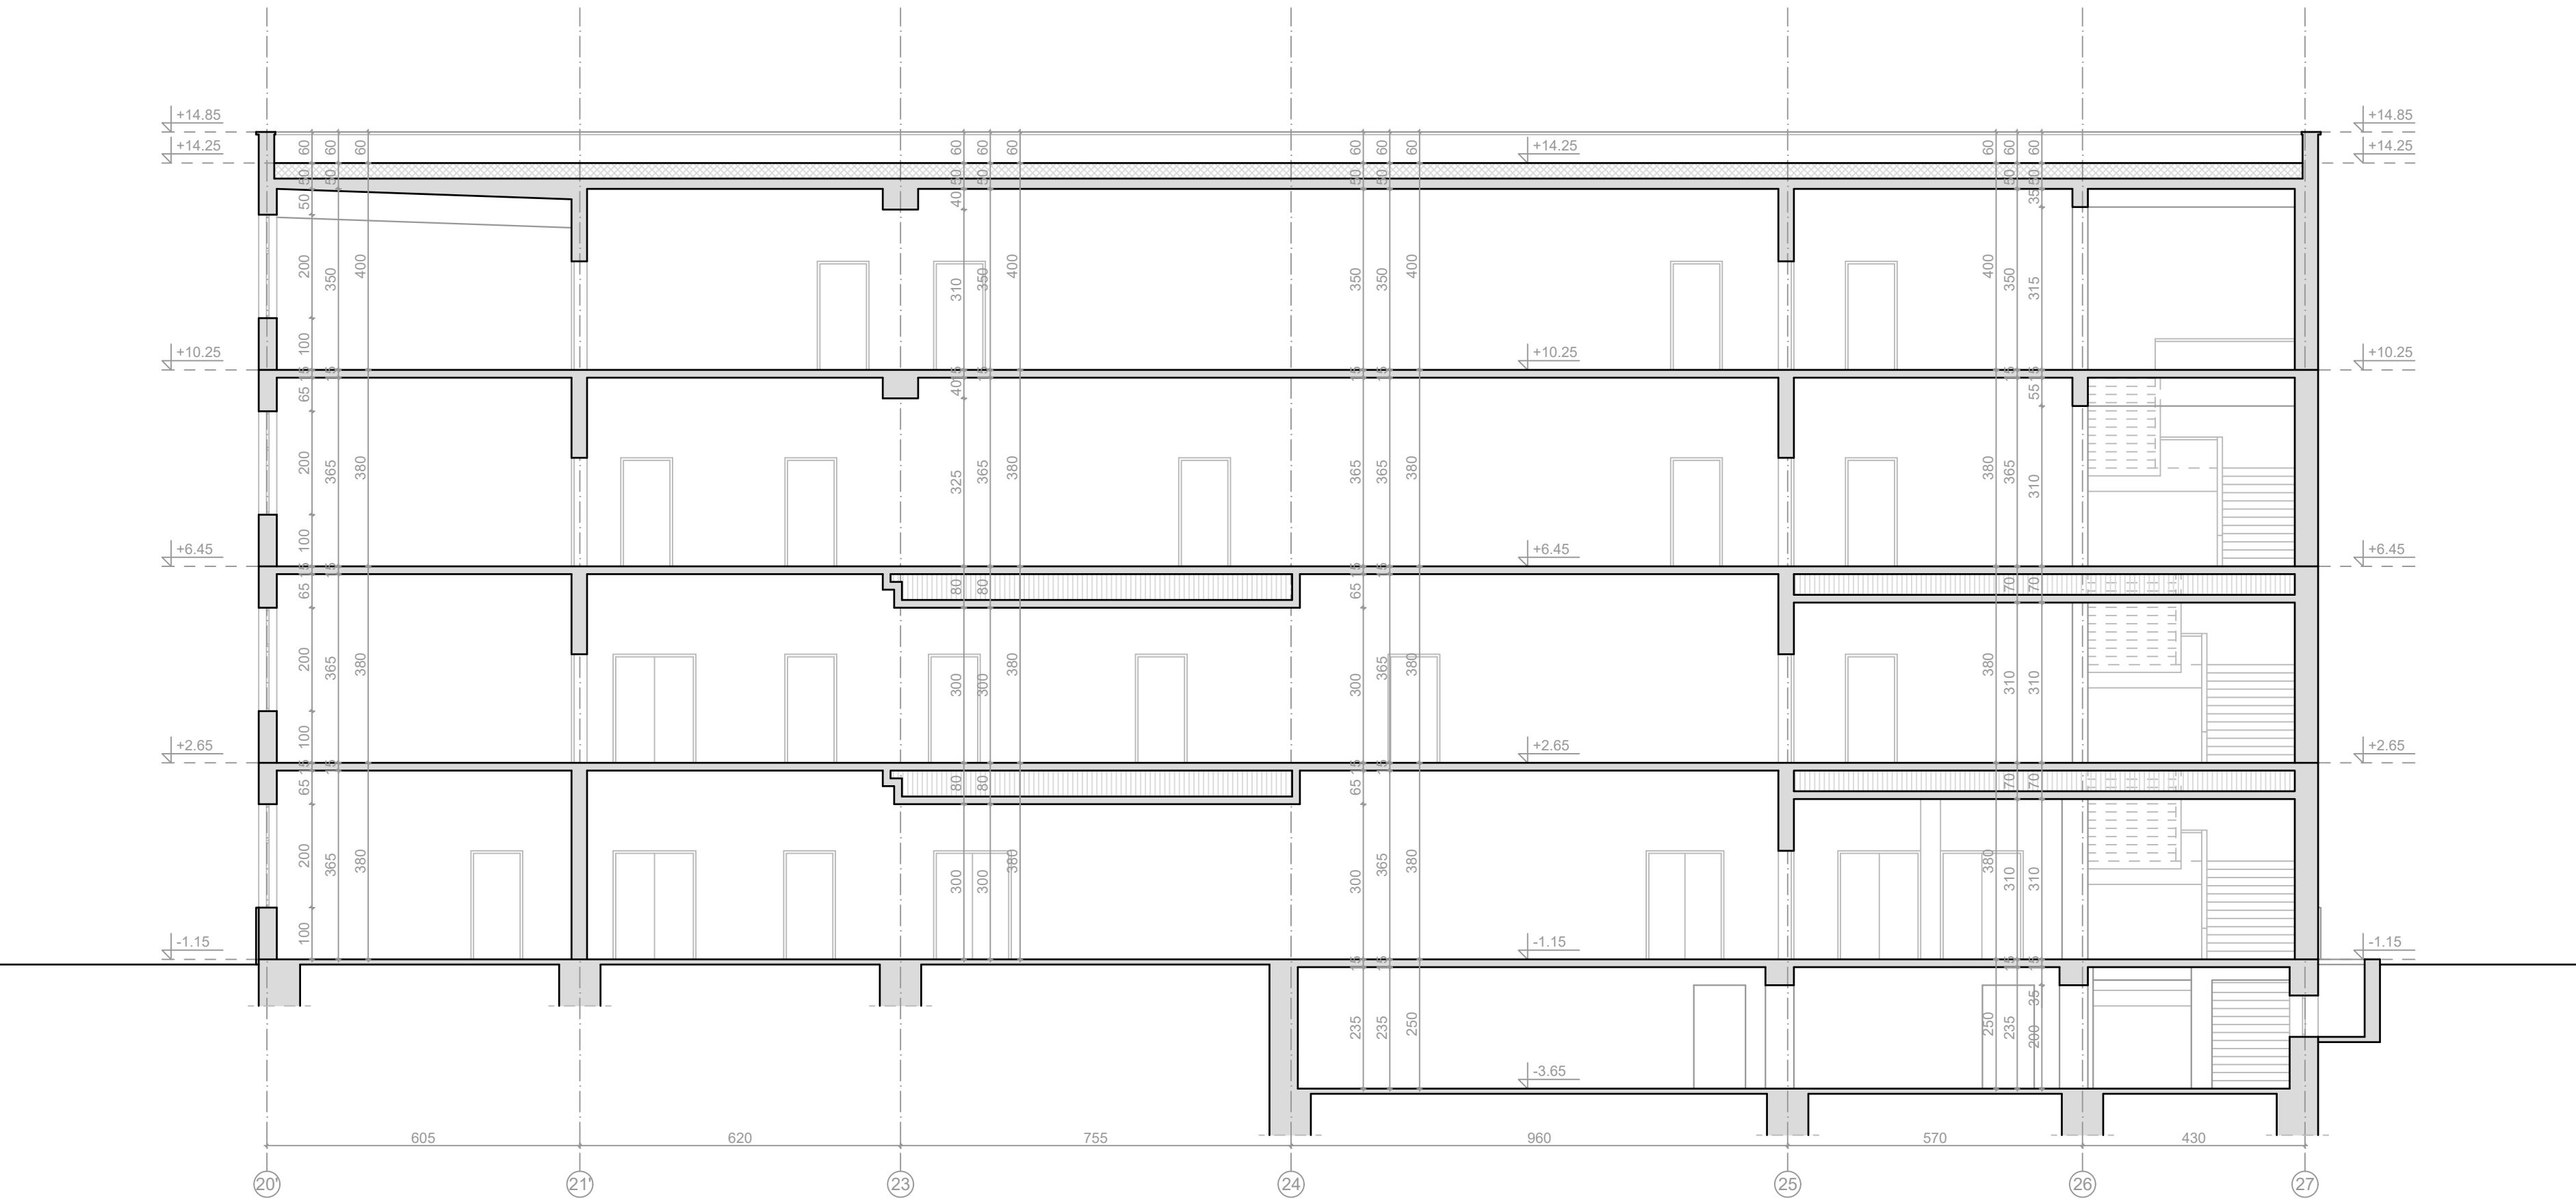

Разрез 2-2

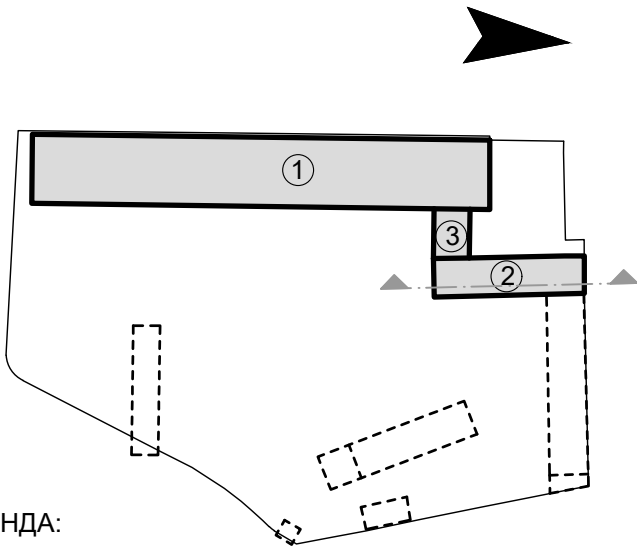

- ЛЕГЕНДА:
- ① ТЯЛО 1
 - ② ТЯЛО 2
 - ③ ТОПЛА ВРЪЗКА

СИТУАЦИОННА СХЕМА МАЩАБ: 1:2000

ПЕЧАТ НА ГЛАВНИЯ ПРОЕКТАНТ:


ВЪЗЛОЖИТЕЛ:	ПОДПИС:
ОБЩИНА ГАБРОВО	

ОБЕКТ: Архитектурно заснемане на сградата на бившата Професионална гимназия по текстил и моден дизайн


Разположение съгласно ПУП: УПИ II-за техникум по текстил, квартал 111 по ПУП на ЦГЧ на гр. Габрово;
Разположение съгласно КККР: поземлен, имот с идентификатор 14218.504.402 по КККР на гр. Габрово;
Идентификатор на сграда: 14218.504.402.3

ЧЕРТЕЖ: РАЗРЕЗ 2-2

ФАЗА: АРХИТЕКТУРНО ЗАСНЕМАНЕ			
ГЛАВЕН ПРОЕКТАНТ:	арх. Я. ПАНЕВ		
СПЕЦИАЛНОСТ:	СЪГЛАСУВАЛ:	ПОДПИС:	
Архитектура	арх. Я. ПАНЕВ		
ЧАСТ:	Архитектура	ДАТА:	2023г.
МАЩАБ:	1:100	ЛИСТ № :	16/25

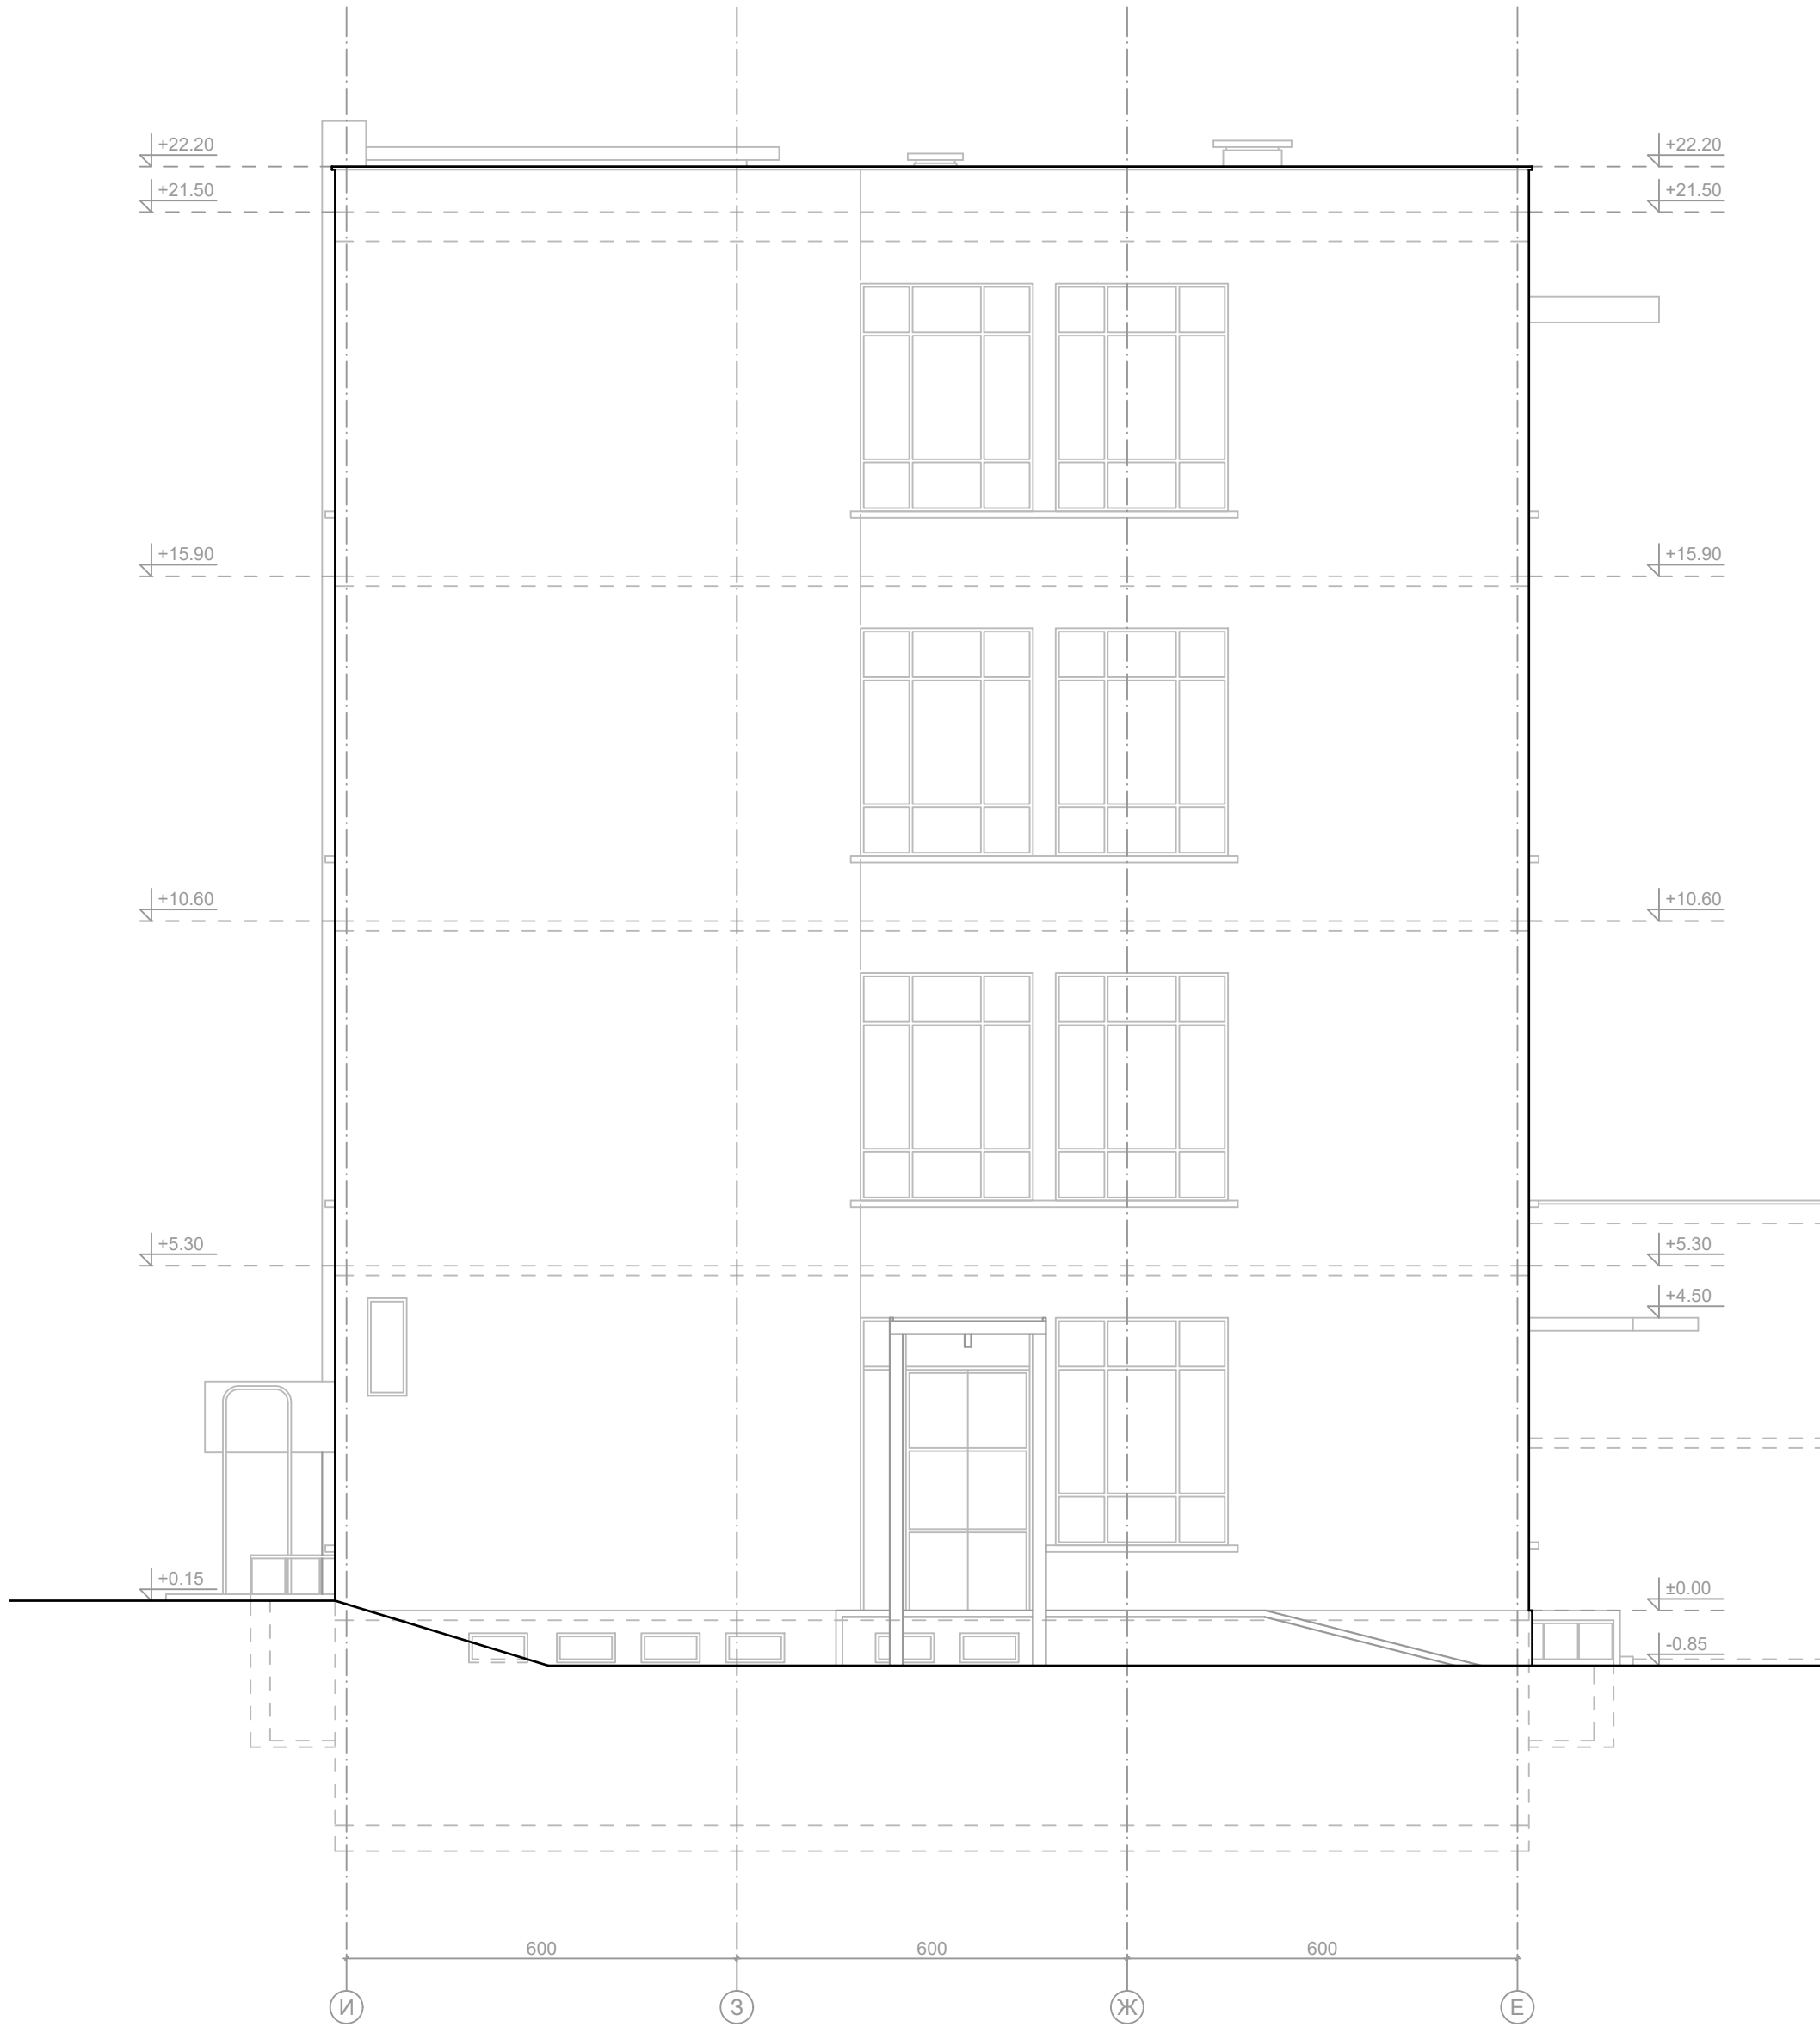

Тяло 1
Фасада ЮГ

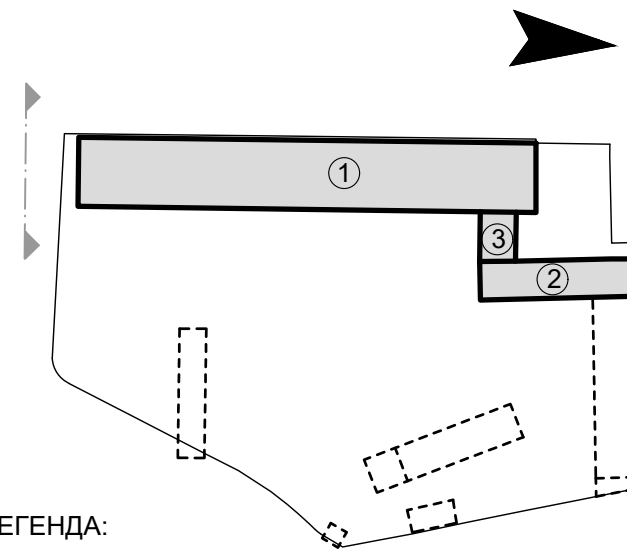


- ЛЕГЕНДА:
- ① ТЯЛО 1
 - ② ТЯЛО 2
 - ③ ТОПЛА ВРЪЗКА

СИТУАЦИОННА СХЕМА		МАЩАБ: 1:2000	
ПЕЧАТ НА ГЛАВНИЯ ПРОЕКТАНТ:			
ВЪЗЛОЖИТЕЛ:		ПОДПИС:	
ОБЩИНА ГАБРОВО			
ОБЕКТ: Архитектурно заснемане на сградата на бившата Професионална гимназия по текстил и моден дизайн Разположение съгласно ПУП: УПИ II-за техникум по текстил, квартал 111 по ПУП на ЦГЧ на гр. Габрово; Разположение съгласно КККР: поземлен имот с идентификатор 14218.504.402 по КККР на гр. Габрово; Идентификатор на сграда: 14218.504.402.3			
ЧЕРТЕЖ: ТЯЛО 1 ФАСАДА ЮГ			
ФАЗА: АРХИТЕКТУРНО ЗАСНЕМАНЕ			
ГЛАВЕН ПРОЕКТАНТ:		арх. Я. ПАНЕВ	
СПЕЦИАЛНОСТ:		СЪГЛАСУВАЛ:	ПОДПИС:
Архитектура		арх. Я. ПАНЕВ	
ЧАСТ: Архитектура		ДАТА: 2023г.	
МАЩАБ: 1:100		ЛИСТ № : 18/25	



Тяло 1
Фасада ИЗТОК

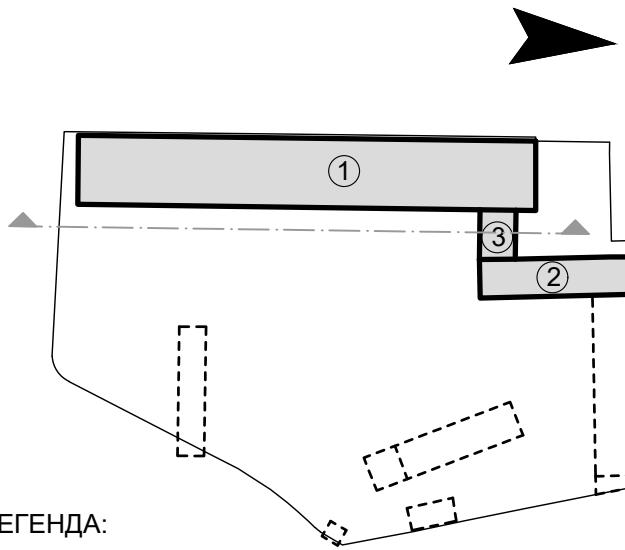

ЛЕГЕНДА:

- 1. Тяло 1
- 2. Тяло 2
- 3. Топла връзка

СИТУАЦИОННА СХЕМА

МАЩАБ: 1:2000

ПЕЧАТ НА ГЛАВНИЯ ПРОЕКТАНТ:

ВЪЗЛОЖИТЕЛ:

ОБЩИНА ГАБРОВО

ПОДПИС:

ОБЕКТ: Архитектурно заснемане на сградата на бившата
Професионална гимназия по текстил и моден дизайн
Разположение съгласно ПУП: УПИ II-за техникум по
текстил, квартал 111 по ПУП на ЦГЧ на гр. Габрово;
Разположение съгласно КККР: поземлен имот с
идентификатор 14218.504.402 по КККР на гр. Габрово;
Идентификатор на сграда: 14218.504.402.3

ЧЕРТЕЖ: ТЯЛО 1 ФАСАДА ИЗТОК

ФАЗА: АРХИТЕКТУРНО ЗАСНЕМАНЕ

ГЛАВЕН ПРОЕКТАНТ: арх. Я. ПАНЕВ

СПЕЦИАЛНОСТ: СЪГЛАСУВАЛ:


Архитектура арх. Я. ПАНЕВ

ЧАСТ: Архитектура


ДАТА: 2023г.

МАЩАБ: 1:100

ЛИСТ №: 19/25

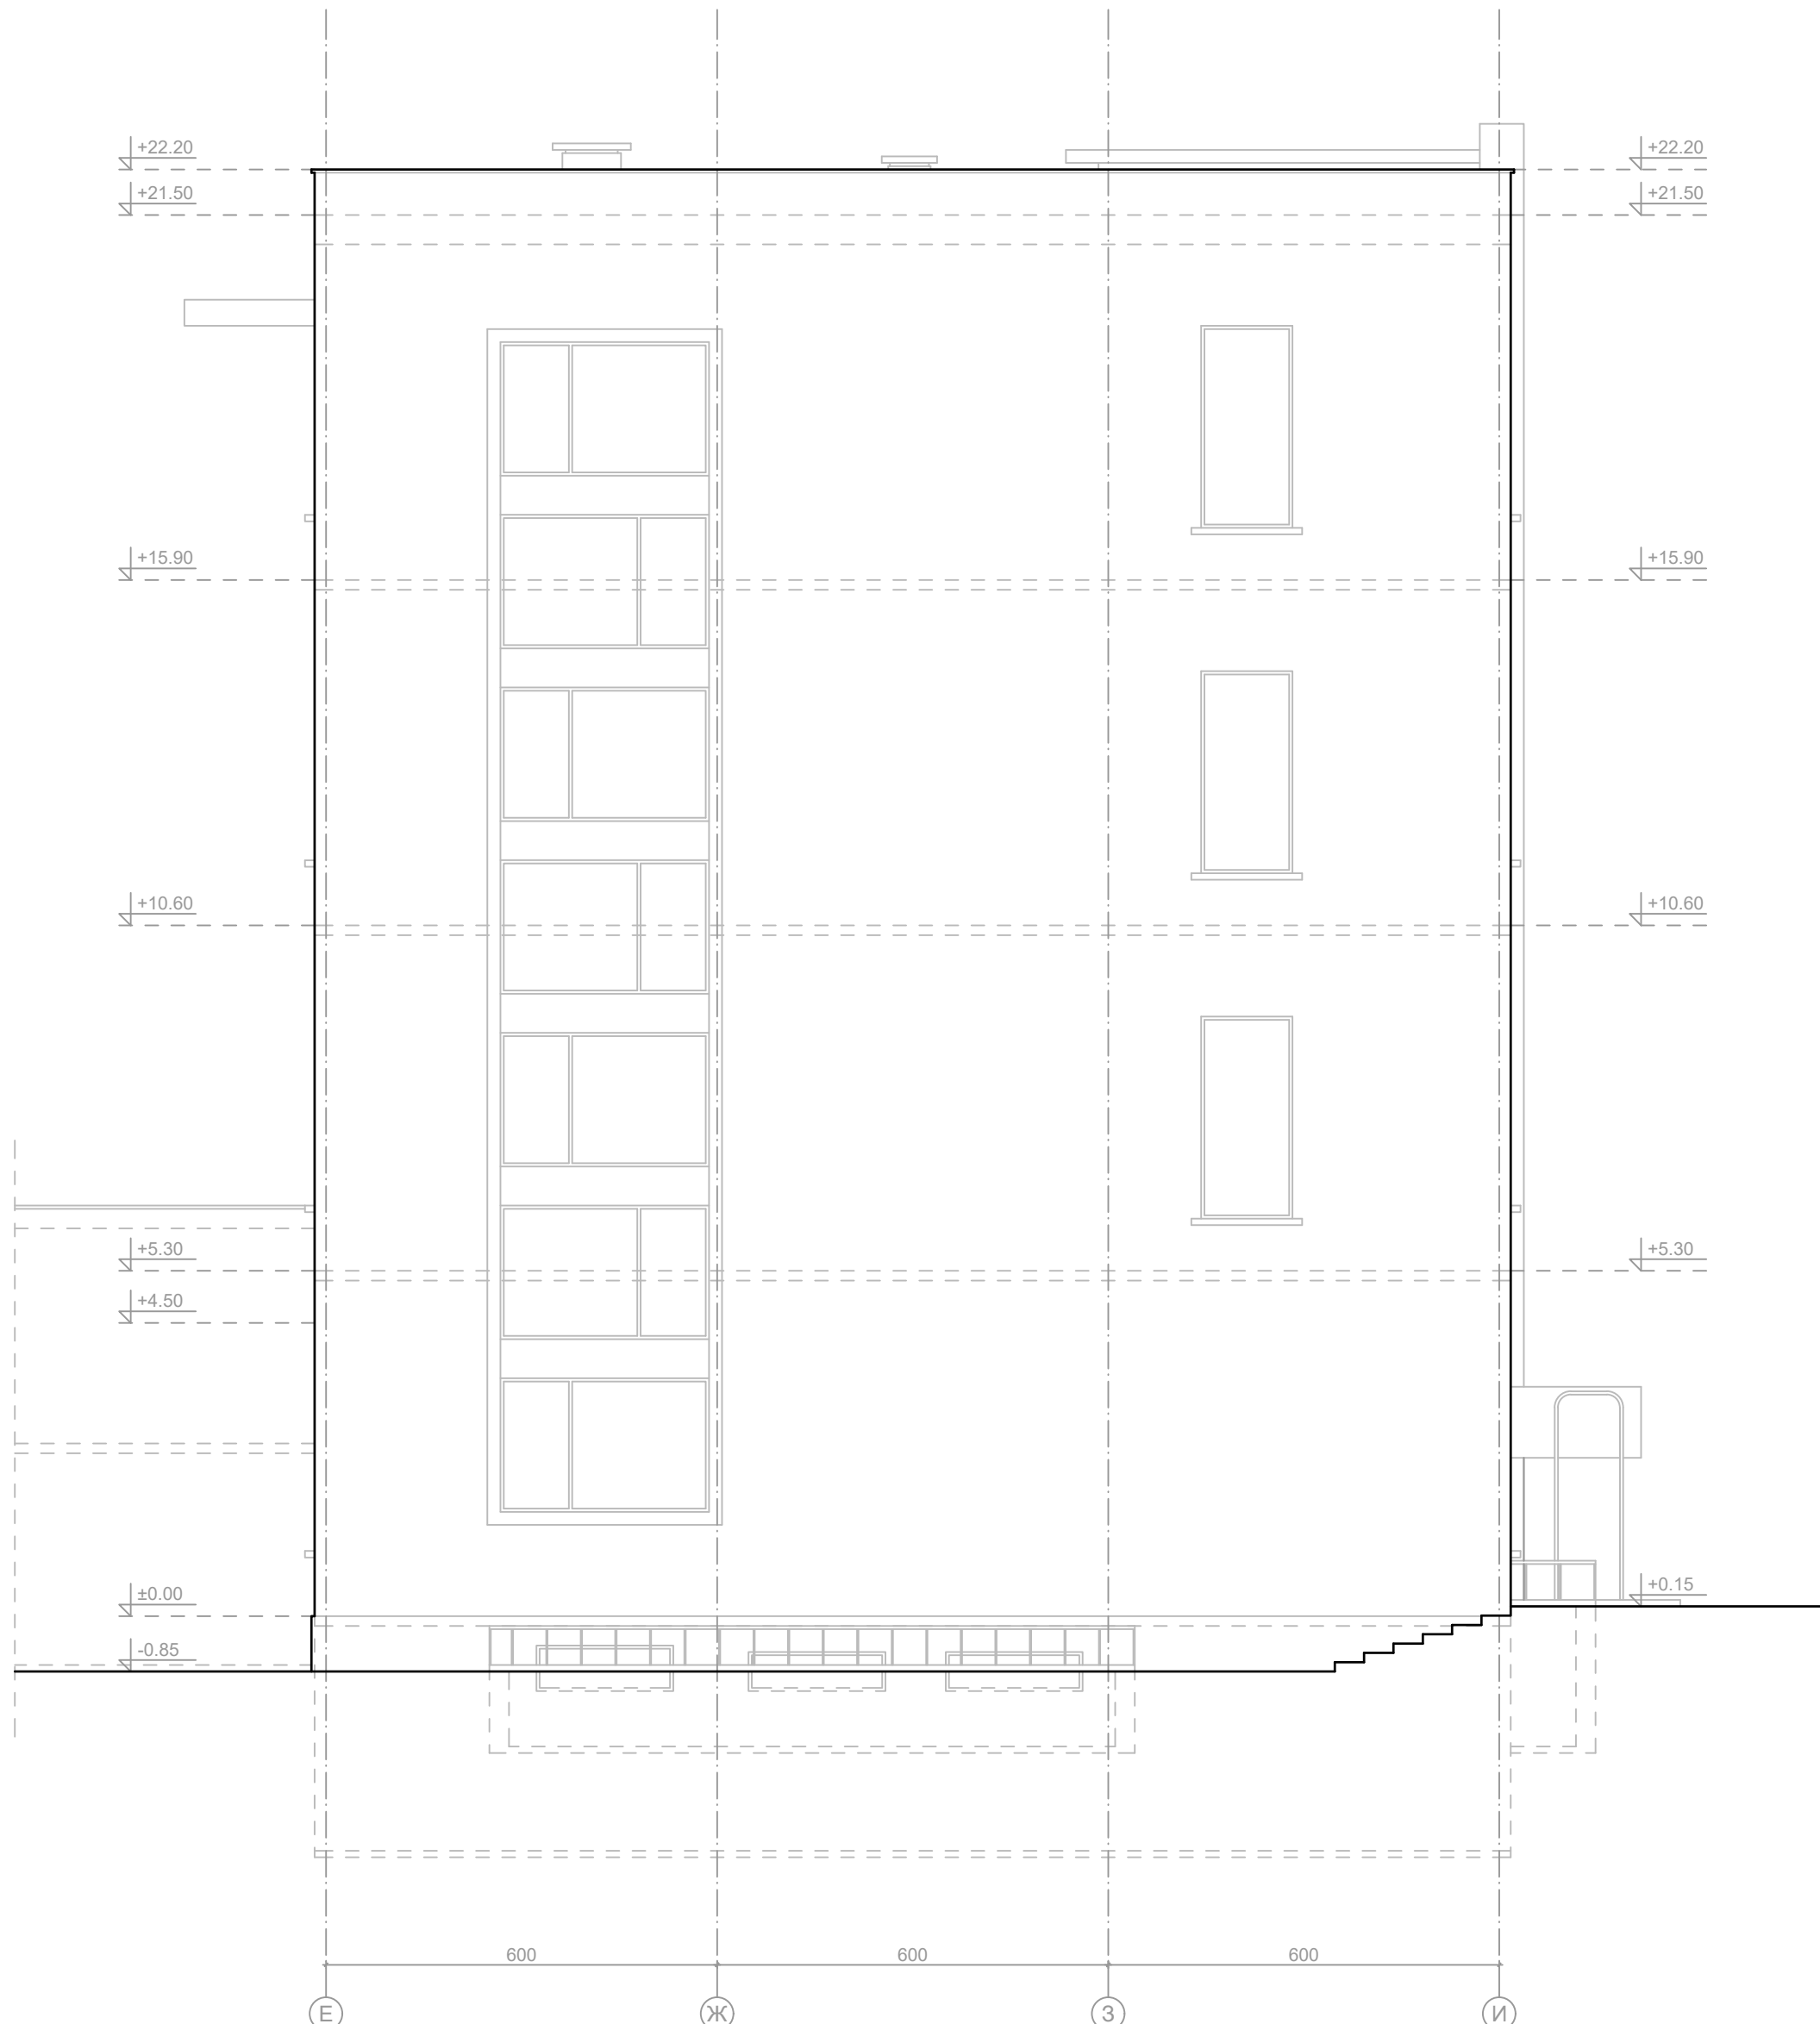

Тяло 1
Фасада СЕВЕР

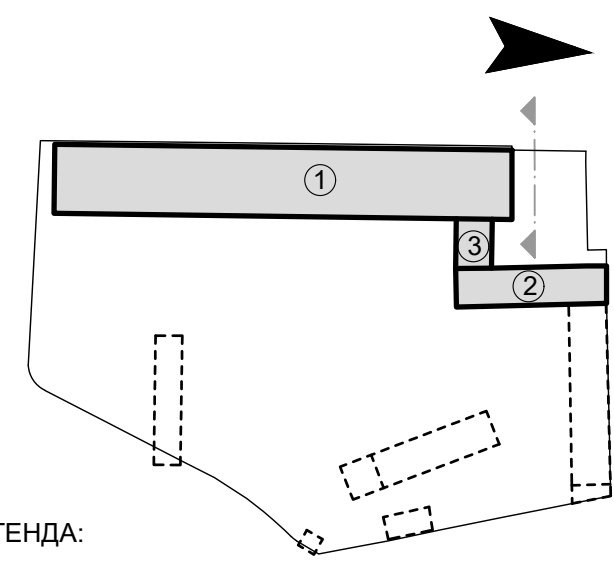

- ЛЕГЕНДА:
- ① ТЯЛО 1
 - ② ТЯЛО 2
 - ③ ТОПЛА ВРЪЗКА

СИТУАЦИОННА СХЕМА	МАЩАБ: 1:2000
-------------------	---------------

ПЕЧАТ НА ГЛАВНИЯ ПРОЕКТАНТ:


ВЪЗЛОЖИТЕЛ:	ПОДПИС:
ОБЩИНА ГАБРОВО	

ОБЕКТ: Архитектурно заснемане на сградата на бившата
Професионална гимназия по текстил и моден дизайн


Разположение съгласно ПУП: УПИ II-за техникум по
текстил, квартал 111 по ПУП на ЦГЧ на гр. Габрово;
Разположение съгласно КККР: поземлен имот с
идентификатор 14218.504.402 по КККР на гр. Габрово;
Идентификатор на сграда: 14218.504.402.3

ЧЕРТЕЖ: ТЯЛО 1 ФАСАДА СЕВЕР

ФАЗА:	АРХИТЕКТУРНО ЗАСНЕМАНЕ		
ГЛАВЕН ПРОЕКТАНТ:	арх. Я. ПАНЕВ		
СПЕЦИАЛНОСТ:	СЪГЛАСУВАЛ:	ПОДПИС:	
Архитектура	арх. Я. ПАНЕВ		
ЧАСТ:	Архитектура	ДАТА:	2023г.
МАЩАБ:	1:100	ЛИСТ № :	20/25

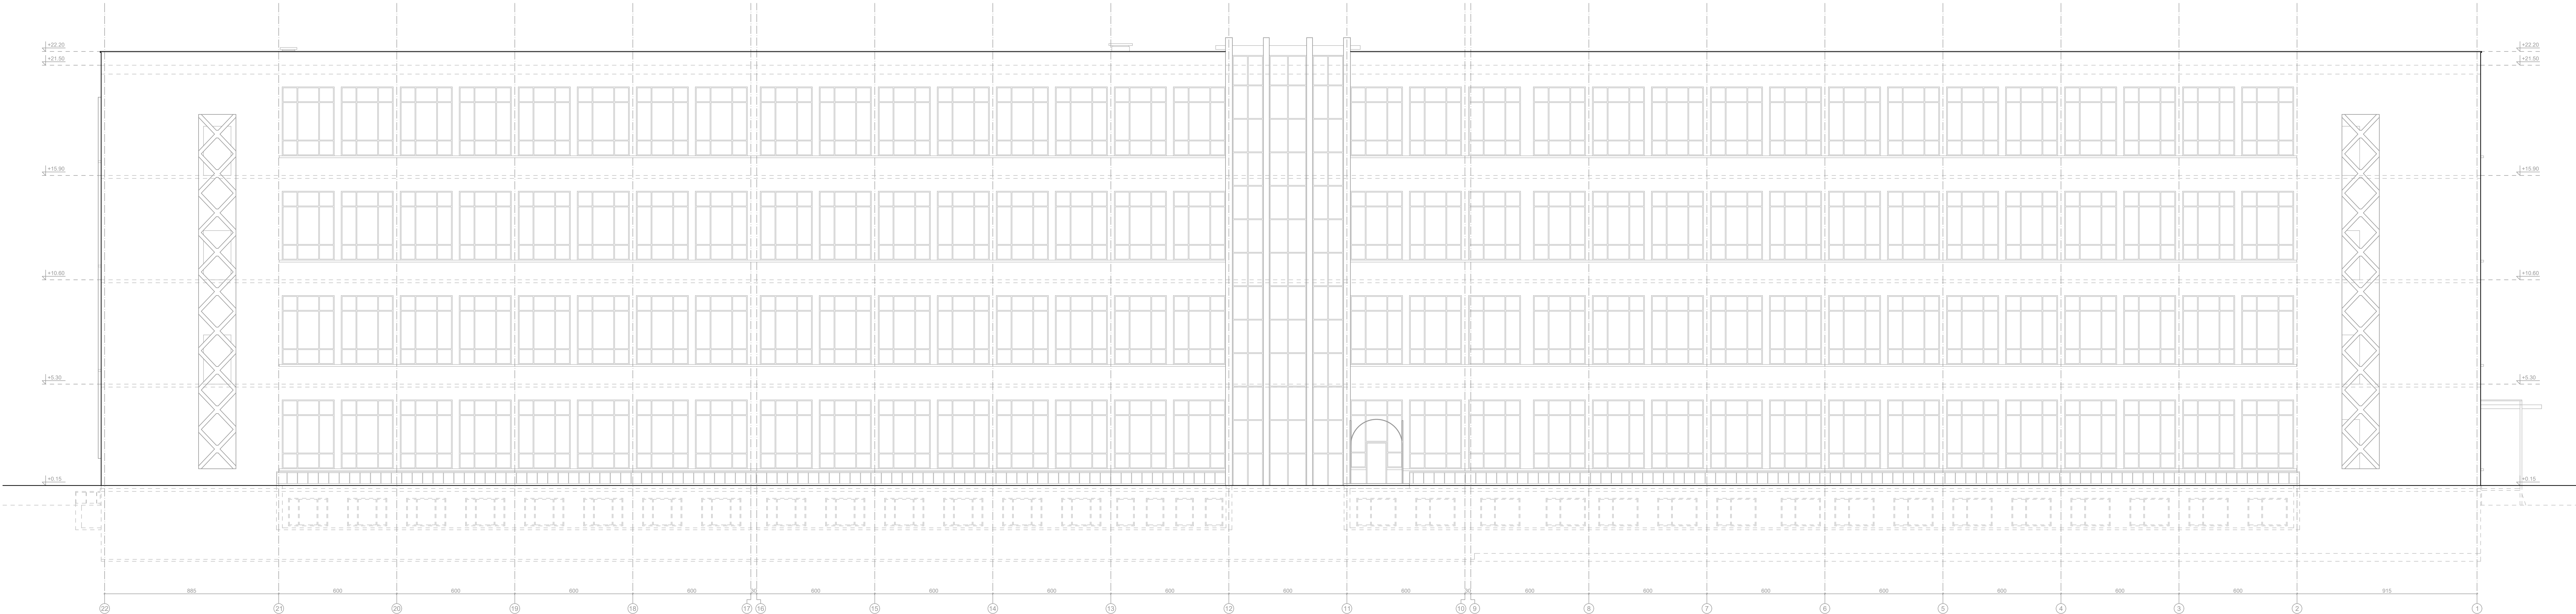

Тяло 1
Фасада ЗАПАД

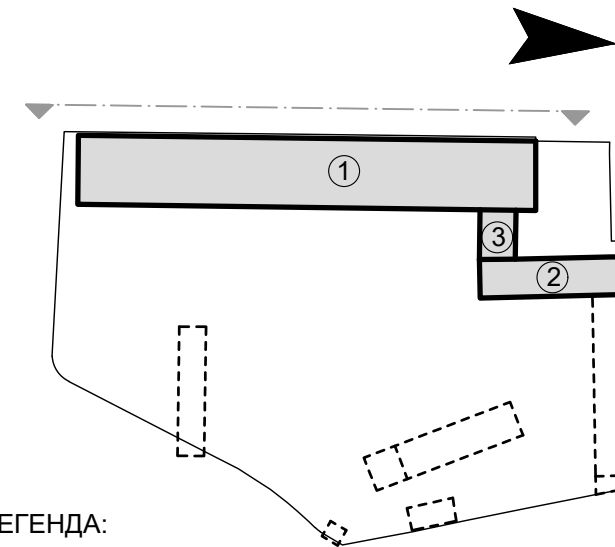

ЛЕГЕНДА:

- 1 ТЯЛО 1
- 2 ТЯЛО 2
- 3 ТОПЛА ВРЪЗКА

СИТУАЦИОННА СХЕМА

МАЩАБ: 1:2000

ПЕЧАТ НА ГЛАВНИЯ ПРОЕКТАНТ:

ВЪЗЛОЖИТЕЛ:

ОБЩИНА ГАБРОВО

ПОДПИС:

ОБЕКТ: Архитектурно заснемане на сградата на бившата
Професионална гимназия по текстил и моден дизайн
Разположение съгласно ПУП: УПИ II-за техникум по
текстил, квартал 111 по ПУП на ЦГЧ на гр. Габрово;
Разположение съгласно ККР: поземлен имот с
идентификатор 14218.504.402 по ККР на гр. Габрово;
Идентификатор на сграда: 14218.504.402.3

ЧЕРТЕЖ: ТЯЛО 1 ФАСАДА ЗАПАД

ФАЗА: АРХИТЕКТУРНО ЗАСНЕМАНЕ

ГЛАВЕН ПРОЕКТАНТ: арх. Я. ПАНЕВ

СПЕЦИАЛНОСТ: АРХИТЕКТУРА

СЪГЛАСУВАЛ: арх. Я. ПАНЕВ

ПОДПИС:

ЧАСТ: Архитектура


МАЩАБ: 1:100

ДАТА: 2023г.

ЛИСТ №: 21/25



Тяло 2 и топла връзка
Фасада ЮГ

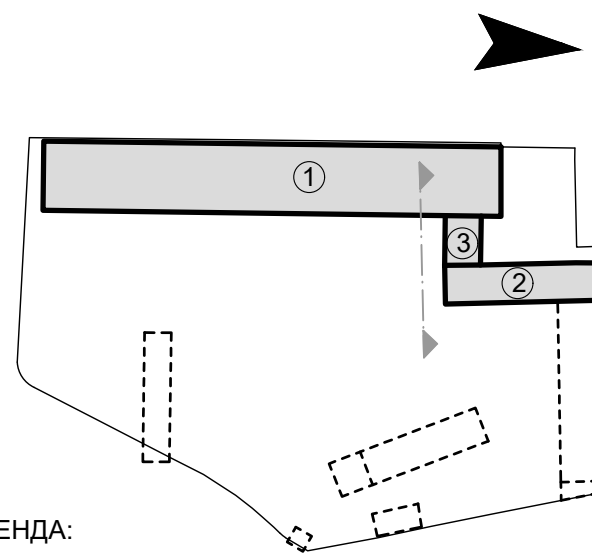

ЛЕГЕНДА:

- ① ТЯЛО 1
- ② ТЯЛО 2
- ③ ТОПЛА ВРЪЗКА

СИТУАЦИОННА СХЕМА

МАЩАБ: 1:2000

ПЕЧАТ НА ГЛАВНИЯ ПРОЕКТАНТ:

ВЪЗЛОЖИТЕЛ:

ОБЩИНА ГАБРОВО

ПОДПИС:

ОБЕКТ: Архитектурно заснемане на сградата на бившата
Професионална гимназия по текстил и моден дизайн

Разположение съгласно ПУП: УПИ II-за техникум по
текстил, квартал 111 по ПУП на ЦГЧ на гр. Габрово;
Разположение съгласно КККР: поземлен имот с
идентификатор 14218.504.402 по КККР на гр. Габрово;
Идентификатор на сграда: 14218.504.402.3

ЧЕРТЕЖ: ТЯЛО 2 И ТОПЛА ВР. ФАСАДА ЮГ

ФАЗА: АРХИТЕКТУРНО ЗАСНЕМАНЕ


ГЛАВЕН ПРОЕКТАНТ: арх. Я. ПАНЕВ

СПЕЦИАЛНОСТ: СЪГЛАСУВАЛ: ПОДПИС:


Архитектура арх. Я. ПАНЕВ

ЧАСТ: Архитектура ДАТА: 2023г.

МАЩАБ: 1:100 ЛИСТ № : 22/25

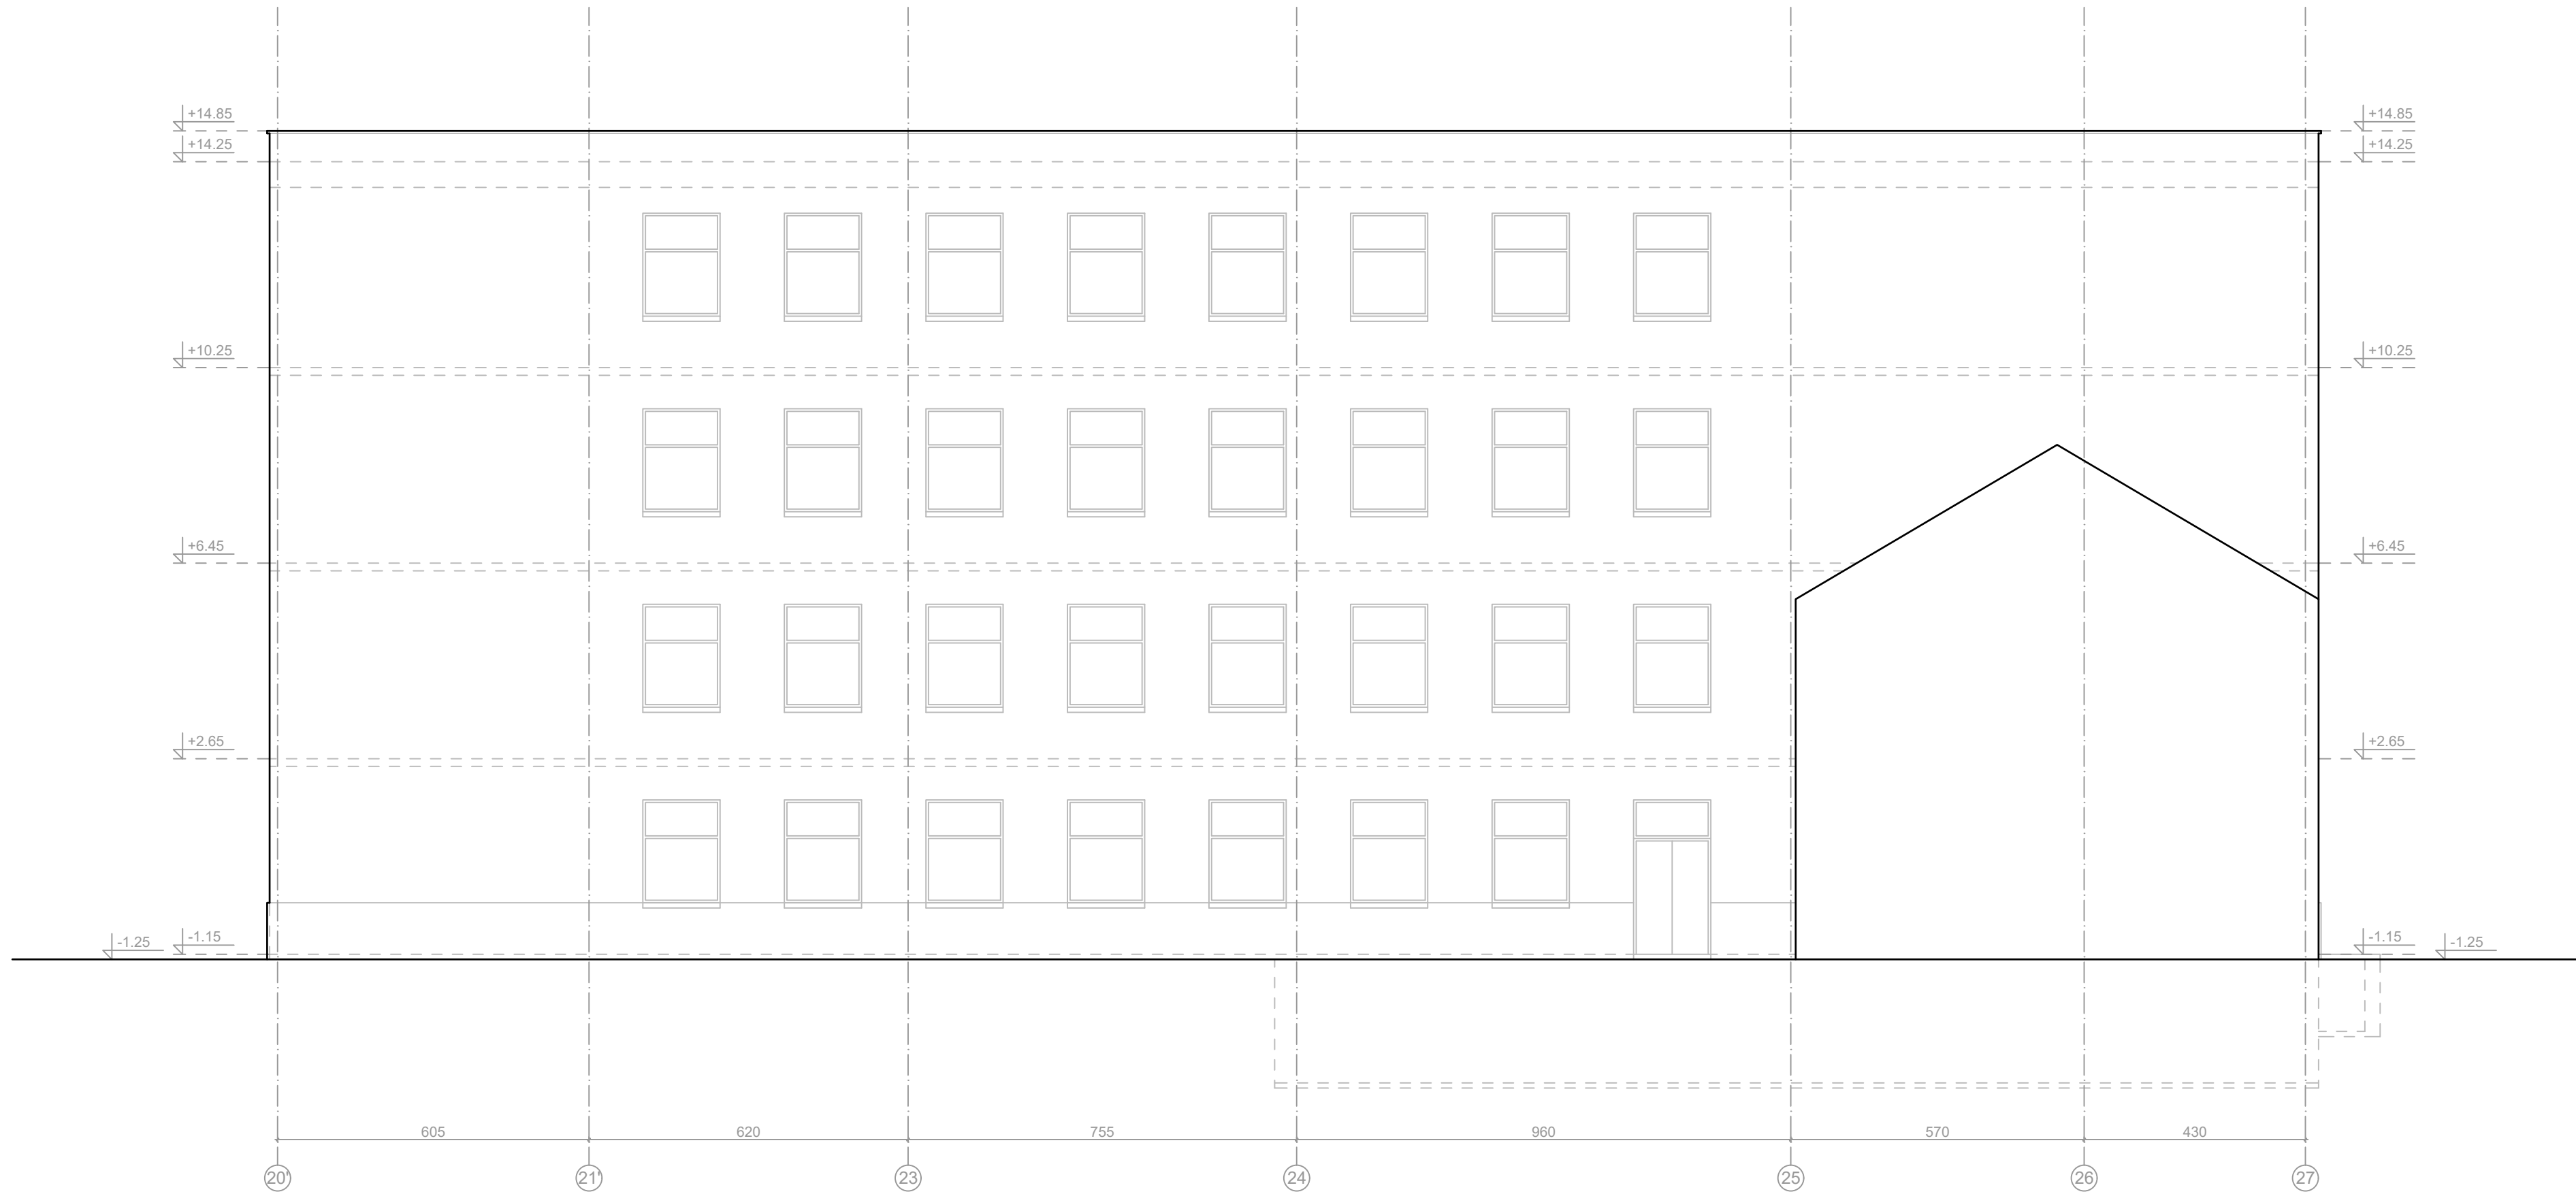

Тяло 2 и топла връзка
Фасада ИЗТОК

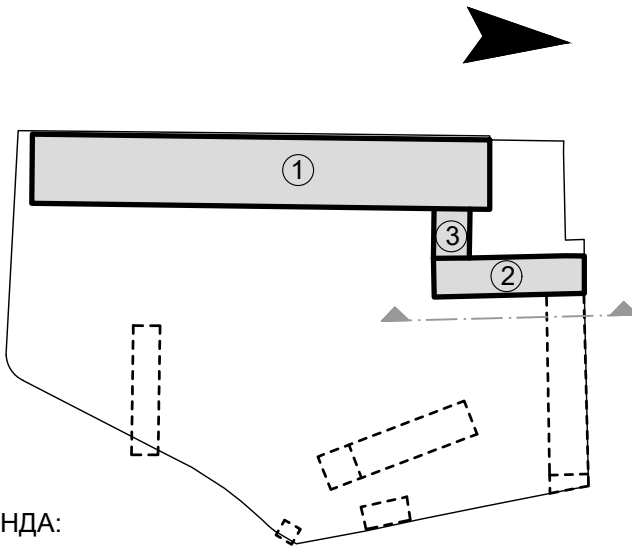

- ЛЕГЕНДА:
- ① ТЯЛО 1
 - ② ТЯЛО 2
 - ③ ТОПЛА ВРЪЗКА

СИТУАЦИОННА СХЕМА

МАЩАБ: 1:2000

ПЕЧАТ НА ГЛАВНИЯ ПРОЕКТАНТ:

ВЪЗЛОЖИТЕЛ:

ОБЩИНА ГАБРОВО

ПОДПИС:

ОБЕКТ: Архитектурно заснемане на сградата на бившата
Професионална гимназия по текстил и моден дизайн

Разположение съгласно ПУП: УПИ II-за техникум по
текстил, квартал 111 по ПУП на ЦГЧ на гр. Габрово;
Разположение съгласно КККР: поземлен имот с
идентификатор 14218.504.402 по КККР на гр. Габрово;
Идентификатор на сграда: 14218.504.402.3

ЧЕРТЕЖ: ТЯЛО 2 И ТОПЛА ВР. ФАСАДА ИЗТОК

ФАЗА: АРХИТЕКТУРНО ЗАСНЕМАНЕ

ГЛАВЕН ПРОЕКТАНТ: арх. Я. ПАНЕВ

СПЕЦИАЛНОСТ: Архитектура


арх. Я. ПАНЕВ

ЧАСТ: Архитектура


ДАТА: 2023г.

МАЩАБ: 1:100

ЛИСТ № : 23/25

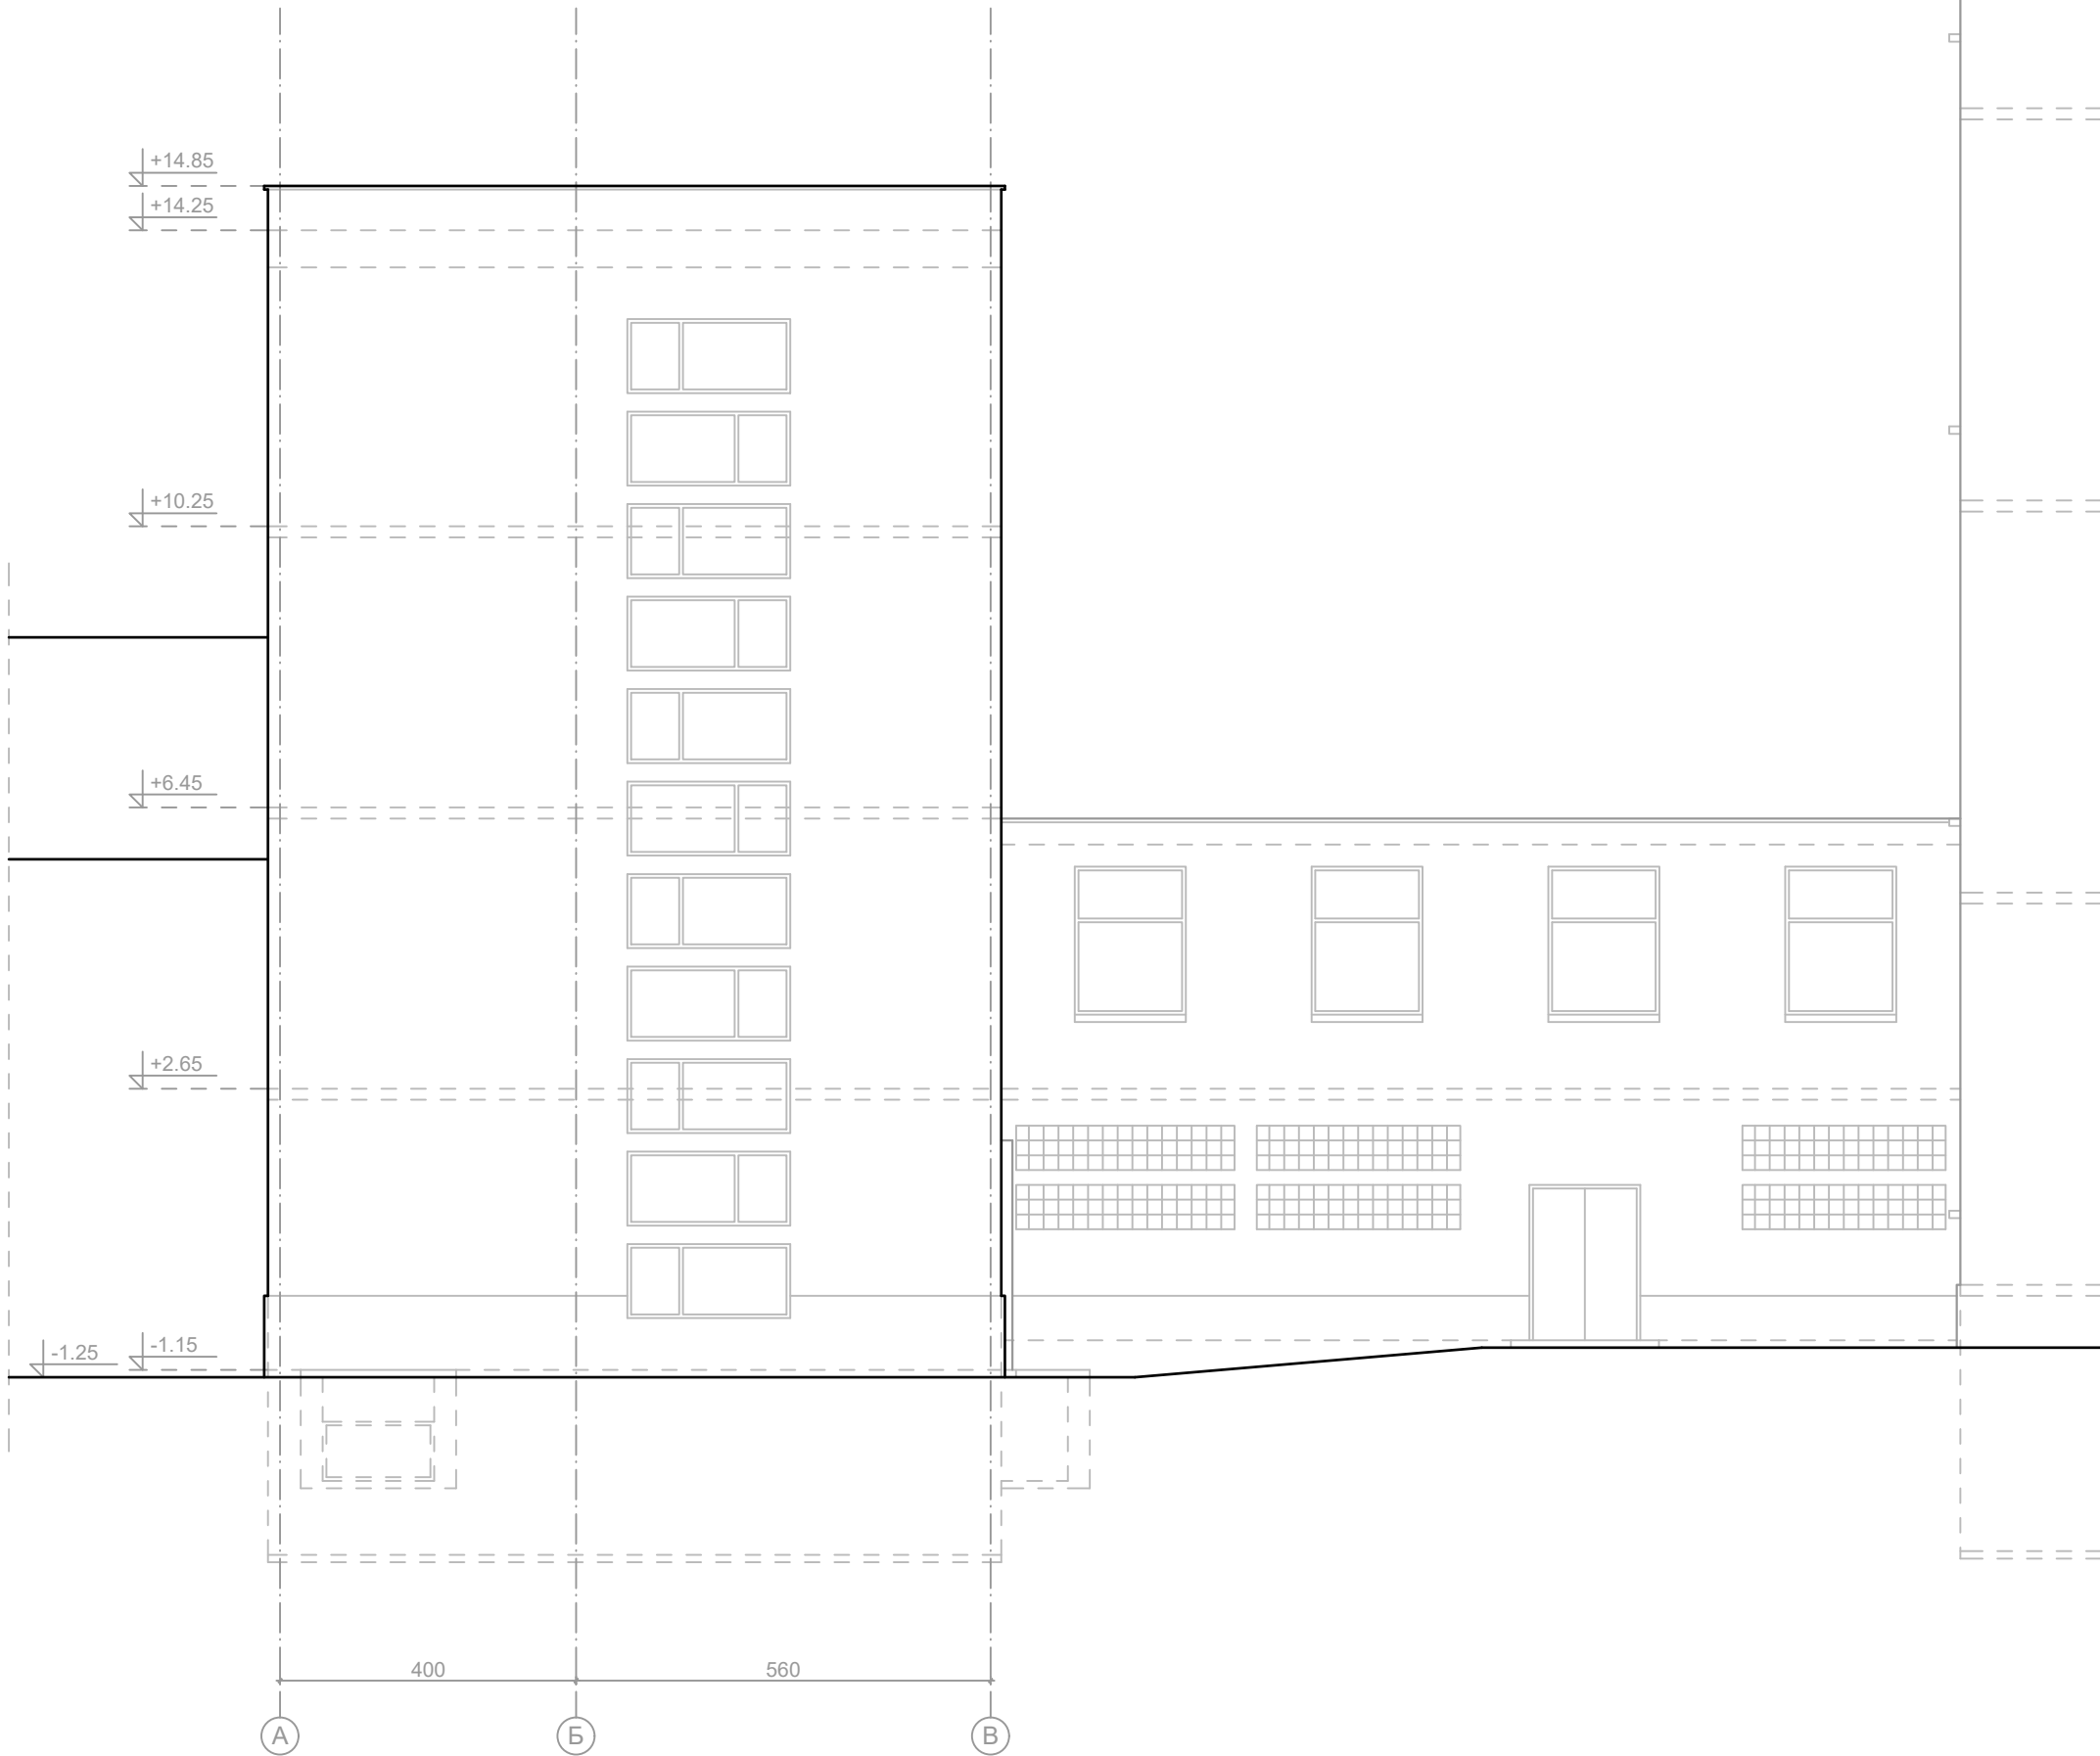



Тяло 2 и топла връзка
Фасада СЕВЕР

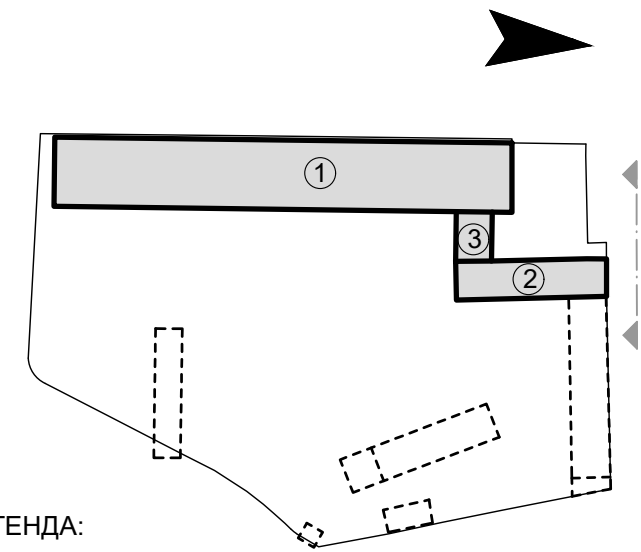

- ЛЕГЕНДА:
- ① ТЯЛО 1
 - ② ТЯЛО 2
 - ③ ТОПЛА ВРЪЗКА

СИТУАЦИОННА СХЕМА		МАЩАБ: 1:2000
ПЕЧАТ НА ГЛАВНИЯ ПРОЕКТАНТ:		
ВЪЗЛОЖИТЕЛ:		ПОДПИС:
ОБЩИНА ГАБРОВО		
ОБЕКТ: Архитектурно заснемане на сградата на бившата Професионална гимназия по текстил и моден дизайн Разположение съгласно ПУП: УПИ II-за техникум по текстил, квартал 111 по ПУП на ЦГЧ на гр. Габрово; Разположение съгласно КККР: поземлен имот с идентификатор 14218.504.402 по КККР на гр. Габрово; Идентификатор на сграда: 14218.504.402.3		
ЧЕРТЕЖ: ТЯЛО 2 И ТОПЛА ВР. ФАСАДА СЕВЕР		
ФАЗА: АРХИТЕКТУРНО ЗАСНЕМАНЕ		
ГЛАВЕН ПРОЕКТАНТ:	арх. Я. ПАНЕВ	
СПЕЦИАЛНОСТ:	СЪГЛАСУВАЛ:	ПОДПИС:
Архитектура	арх. Я. ПАНЕВ	
ЧАСТ: Архитектура	ДАТА: 2023г.	
МАЩАБ: 1:100	ЛИСТ № :	24/25

Тяло 2 и топла връзка
Фасада ЗАПАД

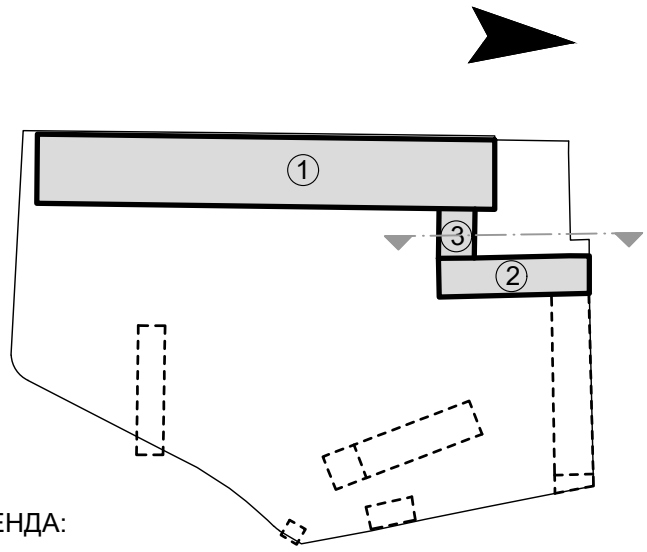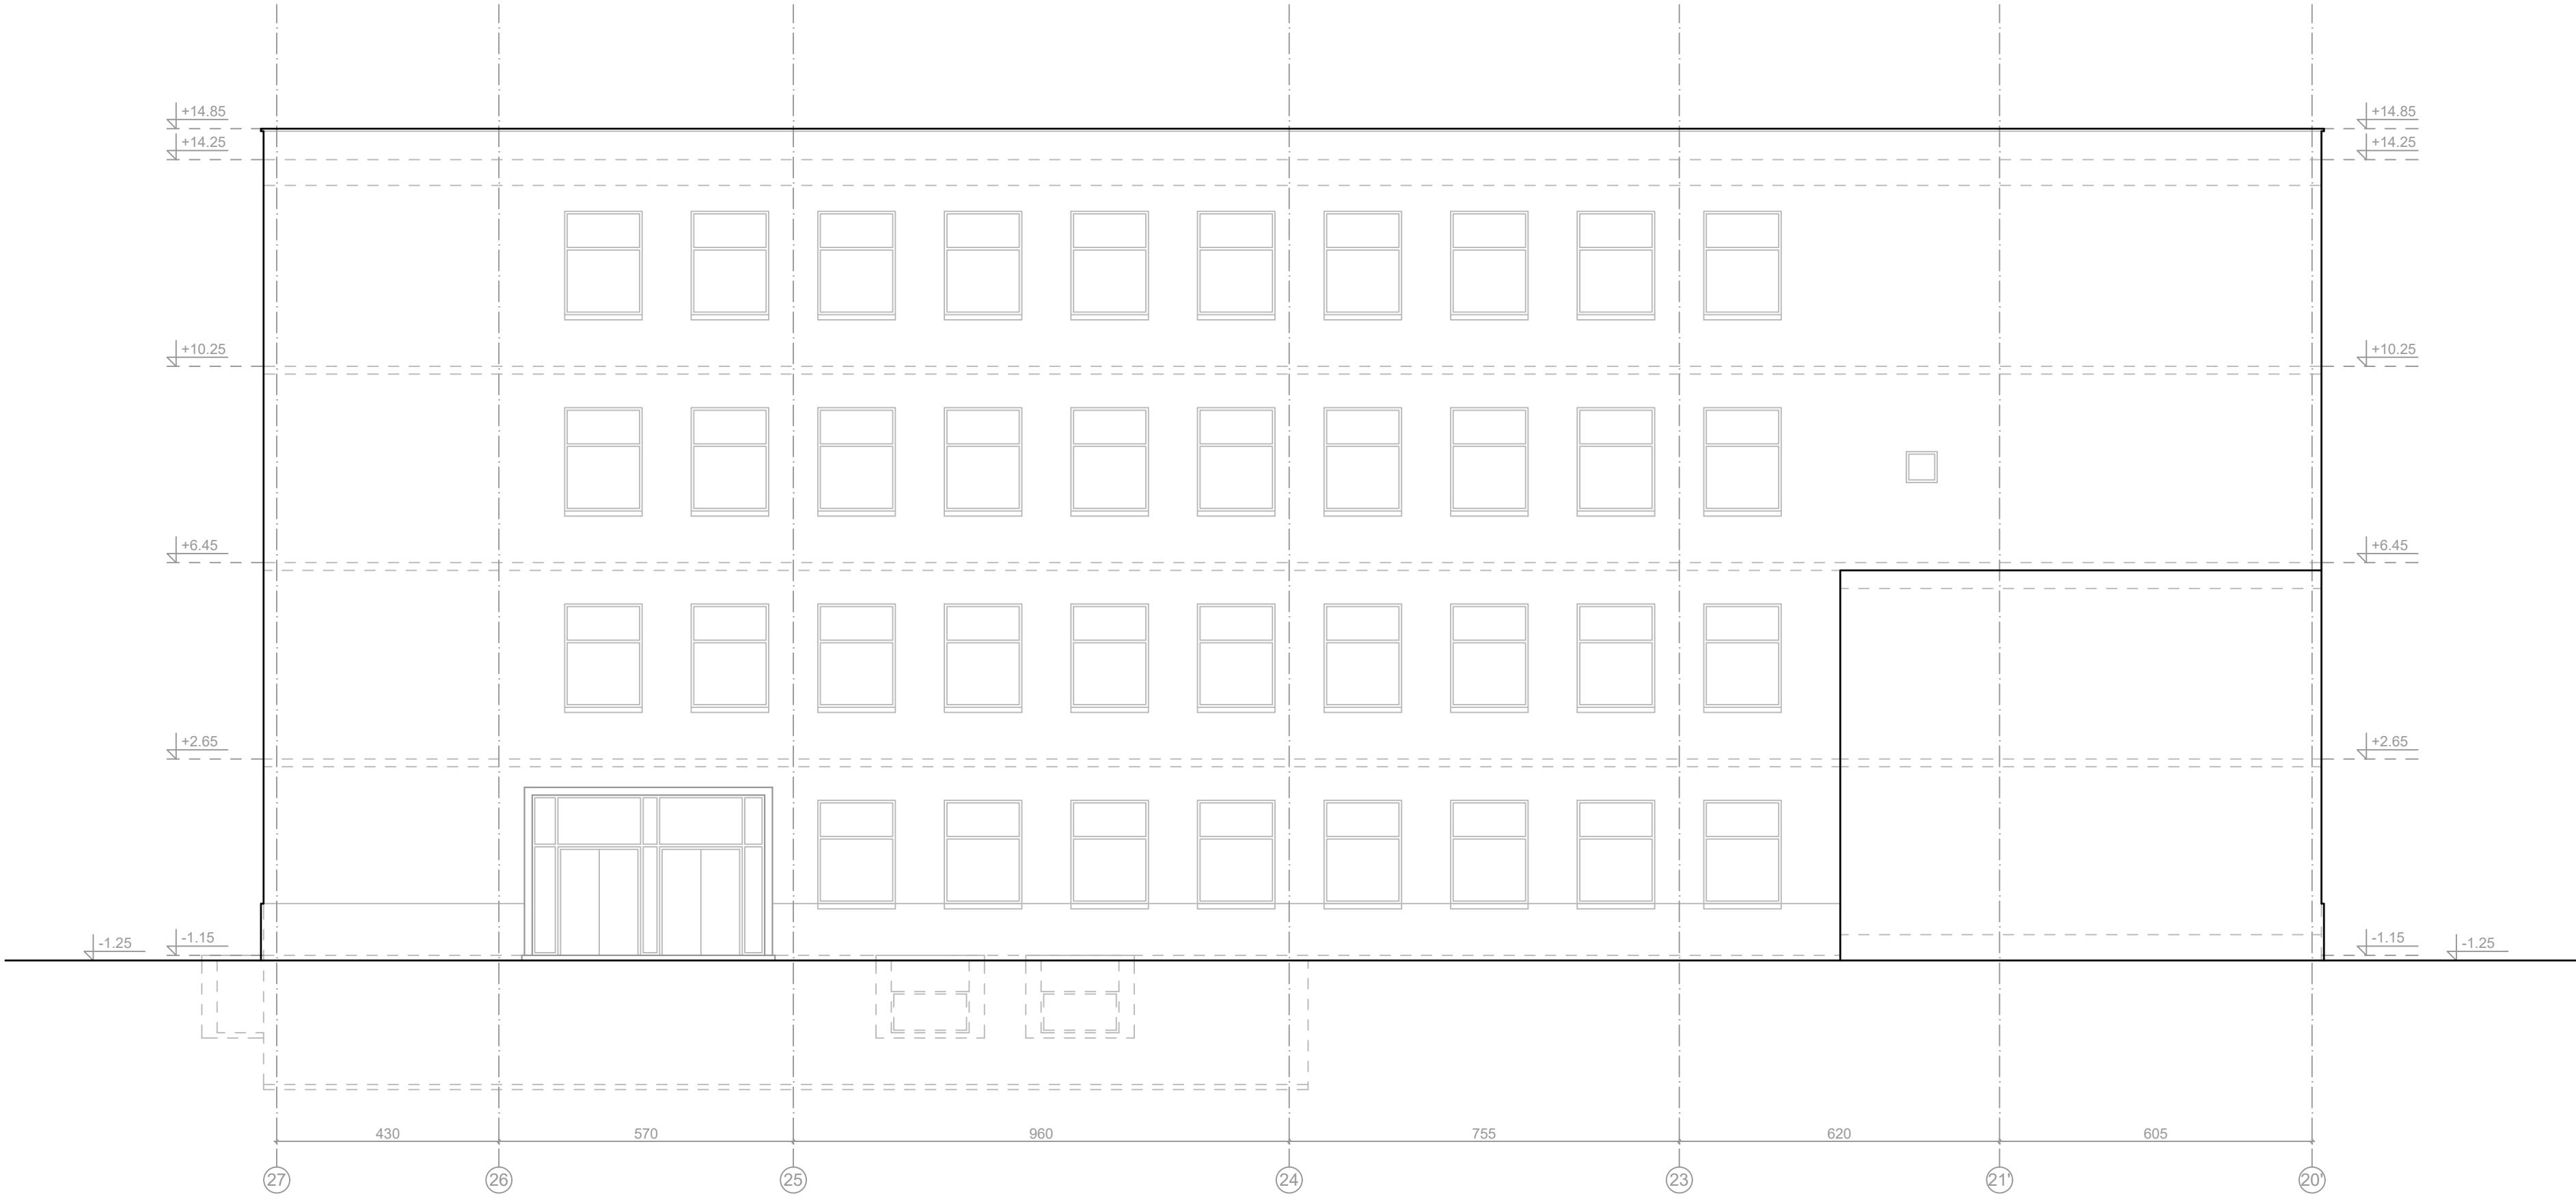

- ЛЕГЕНДА:
- ① ТЯЛО 1
 - ② ТЯЛО 2
 - ③ ТОПЛА ВРЪЗКА

СИТУАЦИОННА СХЕМА МАЩАБ: 1:2000

ПЕЧАТ НА ГЛАВНИЯ ПРОЕКТАНТ:

ВЪЗЛОЖИТЕЛ: ОБЩИНА ГАБРОВО ПОДПИС:

ОБЕКТ: Архитектурно заснемане на сградата на бившата
Професионална гимназия по текстил и моден дизайн

Разположение съгласно ПУП: УПИ II-за техникум по
текстил, квартал 111 по ПУП на ЦГЧ на гр. Габрово;
Разположение съгласно КККР: поземлен имот с
идентификатор 14218.504.402 по КККР на гр. Габрово;
Идентификатор на сграда: 14218.504.402.3

ЧЕРТЕЖ: ТЯЛО 2 И ТОПЛА ВР. ФАСАДА ЗАПАД

ФАЗА: АРХИТЕКТУРНО ЗАСЕМАНЕ

ГЛАВЕН ПРОЕКТАНТ: арх. Я. ПАНЕВ

СПЕЦИАЛНОСТ: Архитектура СЪГЛАСУВАЛ: арх. Я. ПАНЕВ ПОДПИС:

ЧАСТ: Архитектура ДАТА: 2023г.

МАЩАБ: 1:100 ЛИСТ № : 25/25