


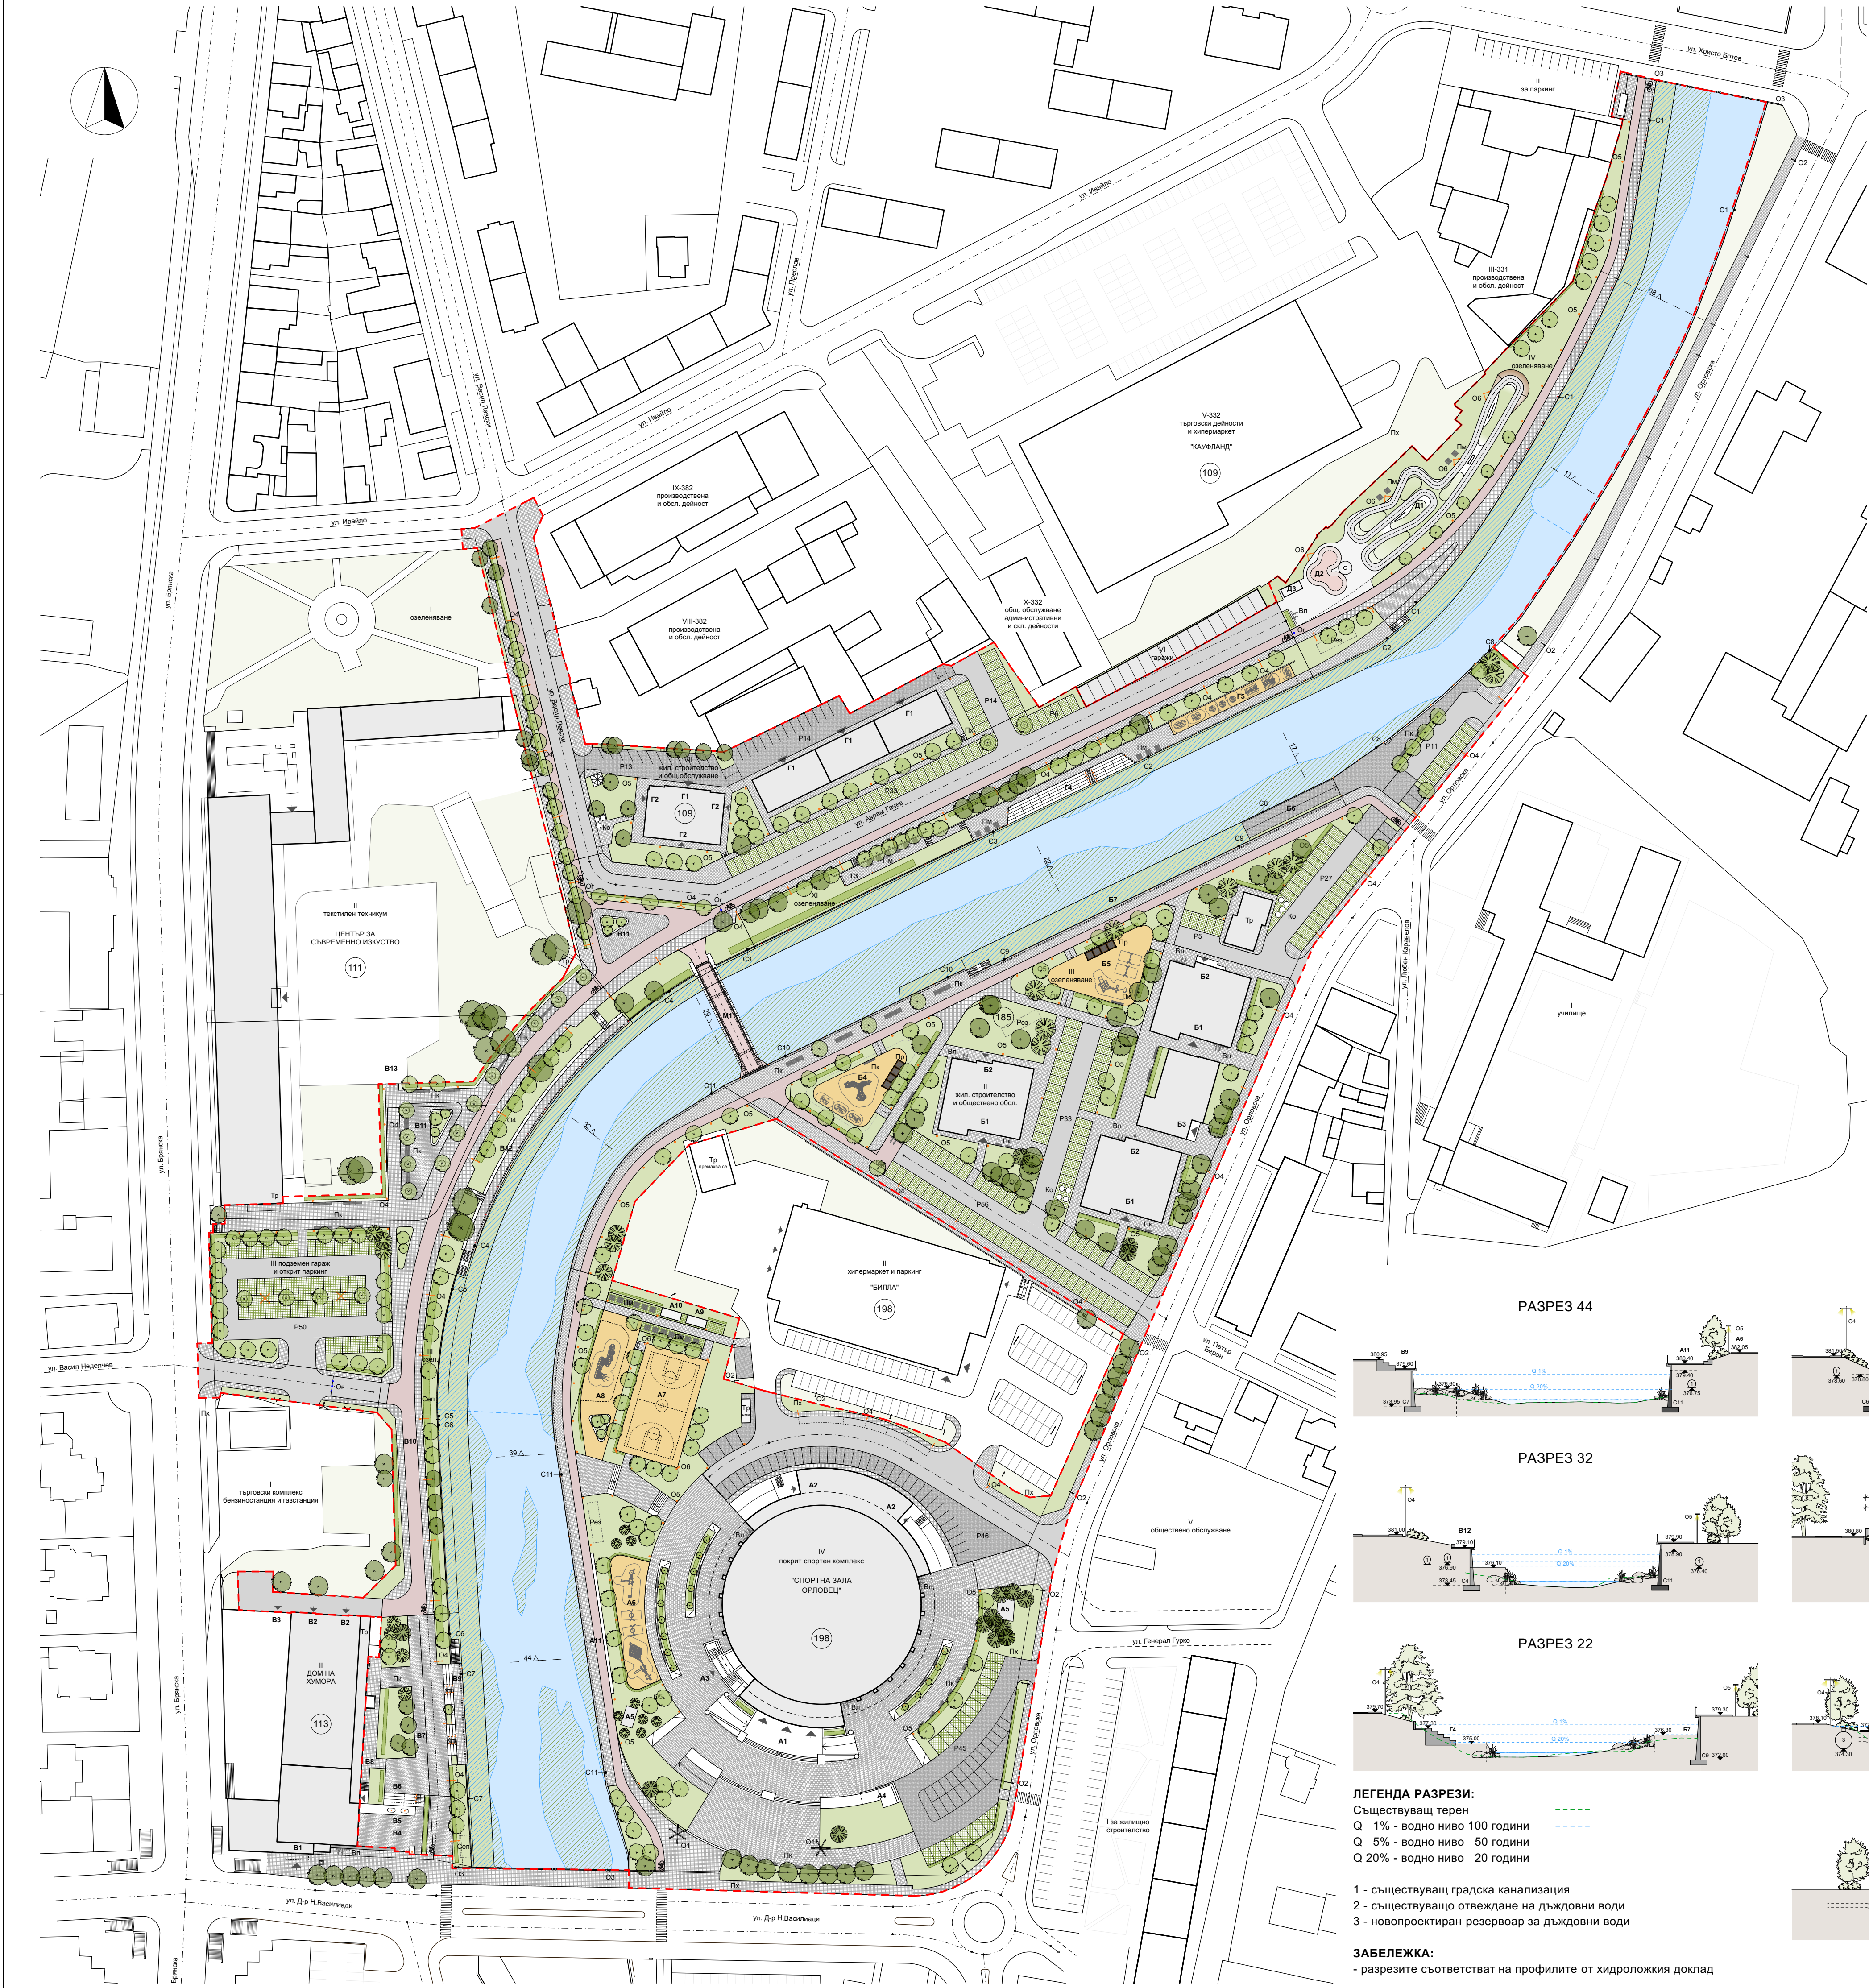

ЛЕГЕНДА

- ПОДОбЕКТ - ДЕСЕН БРЯГ ЮГ**
КВАРТАЛ 198 - СПОРТНА ЗАЛА ОРЛОВОЦ
A1 - ГЛАВЕН ВХОД СПОРТНА ЗАЛА
A2 - СЛУЖЕБЕН ВХОД СПОРТНА ЗАЛА
A3 - ВХОД СУТЕРЕН
A4 - ПИЛОНИ ЗА ЗНАМЕНА
A5 - ВЕНТИЛАЦИЯ НА СПОРТНА ЗАЛА
A6 - ДЕТСКА ПЛОЩАДКА 3-12г. ~ 350м²
A7 - СПОРТНА ПЛОЩАДКА ~630м²
A8 - ВЪЖЕНО СЪОРЪЖЕНИЕ ~ 400м²
A9 - ОБЩЕСТВЕНА ТОАЛЕТНА
A10 - БЮФЕТ
A11 - АЛЕЯ НА СПОРТИСТИТЕ

- ПОДОбЕКТ - ДЕСЕН БРЯГ СЕВЕР**
КВАРТАЛ 185
B1 - ГЛАВЕН ВХОД ЖИЛИЩНА СГРАДА
B2 - ЕВАКУАЦИОНЕН ИЗХОД ЖИЛИЩНА СГРАДА
B3 - ВХОД ТЪРГОВСКА СГРАДА
B4 - СПОРТНА ПЛОЩАДКА ~ 435м²
B5 - ДЕТСКА ПЛОЩАДКА 0-3г. ~ 425м²
B6 - РАМПА ЗА ДОСТЪП ДО РЕКАТА
B7 - ХВАТКИ ЗА КАТЕРЕНЕ НА СТЕНАТА

- ПОДОбЕКТ - ЛЯВ БРЯГ**
КВАРТАЛ 113
ДОМ НА ХУМОРА И САТИРАТА
B1 - ГЛАВЕН ВХОД
B2 - ВХОД ЗА КАРНАВАЛНА РАБОТИЛНИЦА
B3 - СЛУЖЕБЕН ВХОД
B4 - ПЛОЩАД
B5 - СКУЛПТУРНА КОМПОЗИЦИЯ
B6 - ТРИБУНА
B7 - ПАРК НА ХУМОРА
B8 - ИЗХОД ОТ ВАРИЕТЕ
B9 - ТЕРАСА И СЪПЛАЛА КЪМ РЕКАТА
B10 - АЛЕЯ НА ХУМОРА

- КАВАРТАЛ 111**
ЦЕНТЪР ЗА СЪВРЕМЕННО ИЗКУСТВО
B11 - ЗОНА ЗА ИЗЛОЖБИ
B12 - ТЕРАСА И СЪПЛАЛА КЪМ РЕКАТА
B13 - ПЛОЩАД КЪМ ЦЕНТЪР ЗА ИЗКУСТВО
КВАРТАЛ 109
G1 - ВХОД ЖИЛИЩНА СГРАДА
G2 - ВХОД ТЪРГОВСКИ ПЛОЩИ
G3 - ТЕРАСА КЪМ РЕКАТА
G4 - ТРИБУНА КЪМ РЕКАТА
G5 - СПОРТНА ПЛОЩАДКА ~ 160м²

- ПОДОбЕКТ - ЛЯВ БРЯГ СЕВЕР**
КВАРТАЛ 109
D1 - ПЪМПАТРАК
D2 - СКЕЙТБОРД ПУЛ
D3 - ОБЩЕСТВЕНА ТОАЛЕТНА

- ПОДОбЕКТ - ПЕШЕХОДЕН МОСТ**
M1 - ПЕШЕХОДЕН МОСТ

- ПОДПОРНИ СТЕНИ РЕКА**
ЛЯВ (ЗАПАДЕН) БРЯГ
C1 - НОВА СТЕНА Н=5.0-2.5м, L=184м
C2 - НОВА СТЕНА Н=2.5м, L=92м
C3 - НОВА СТЕНА Н=2.5м, L=96м
C4 - НОВА СТЕНА Н=2.5м, L=115м
C5 - НОВА СТЕНА Н=3.0м, L=51м
C6 - НАДГРАЖДАНЕ Н=2.5+0.5м, L=73м
C7 - НОВА СТЕНА Н=3.0м, L=68м
ДЕСЕН (ИЗТОЧЕН) БРЯГ
C8 - НОВА СТЕНА Н=5.0-0.0м, L=92м
C9 - НОВА СТЕНА Н=3.0м, L=123м
C10 - НАДГРАЖДАНЕ Н=3.5+1.0м, L=73м
C11 - НАДГРАЖДАНЕ Н=4.5+1.0м, L=234м

ОБХВАТ НА ОБЕКТА

РАСТИТЕЛНОСТ

ОЗЕЛЕНЕНИ ПЛОЩИ

ХРАСТОВА РАСТИТЕЛНОСТ

СЪЩЕСТВУВАЩИ ДЪРВЕТА

широколистни/ иглолистни

НОВОПРОЕКТИРАНИ ДЪРВЕТА

РЕКА

ОСНОВНО ТЕЧЕНИЕ НА РЕКАТА

ЗОНА С РЕЧНА РАСТИТЕЛНОСТ

ПОДРАВНЕНА ПЕШЕХОДНА ЗОНА

укрепване с ломен камък

НАСТИЛКИ

Зала Орловец

ГРАНИТНИ ПЛОЧИ 60/40см

Дом на хумора

ГРАНИТНИ ПЛОЧИ 60/40см

ПАВЕТА 20/20см

пешеходно движение

ПАВЕТА 20/10см

автомобилно движение

ПАРКИНГ НА ТРЕВНА ФУГА

АСФАЛТ

ЧЕРВЕН АСФАЛТ

АКРИЛНА НАСТИЛКА МОСТ

УДАРОПОГЛЪЩАЩА НАСТИЛКА

СПОРТНА НАСТИЛКА

ИНФРАСТРУКТУРА

Р - БРОЙ ПАРКОМЕСТА

Ко - КОНТЕЙНЕРИ ЗА ВЪГРАЖДАНЕ

Тр - ТРАФОПОСТ

Ог - ОГРАНИЧИТЕЛИ ЗА АВТОМОБИЛИ

Пх - ПОЖАРЕН ХИДРАНТ

Рез - ПОДЗЕМЕН РЕЗЕРВОАР

Сеп - СЕПАРАТОР

ГРАДСКО ОБЗАВЕЖДАНЕ

Пк - ПЕЙКИ

Пм - ПИКНИК МАСИ

Пр - ПЕРГОЛА С ПЕЙКИ

Вл - СТОЙКИ ЗА ВЕЛОСИПЕДИ

УЛИЧНО ОСВЕТЛЕНИЕ:

O1 - СЪЩЕСТВУВАЩ ВИСОК СЪТЪЛБ 10м








O2 - СЪЩЕСТВУВАЩ УЛИЧЕН СЪТЪЛБ 9м

O3 - СЪЩЕСТВУВАЩ СЪТЪЛБ 4.0м

O4 - НОВО УЛИЧНО ОСВЕТЛЕНИЕ 7.5м

O5 - НОВО ПАРКОВО ОСВЕТЛЕНИЕ 4.5м

O6 - НОВО СПОРТНО ОСВЕТЛЕНИЕ 10м

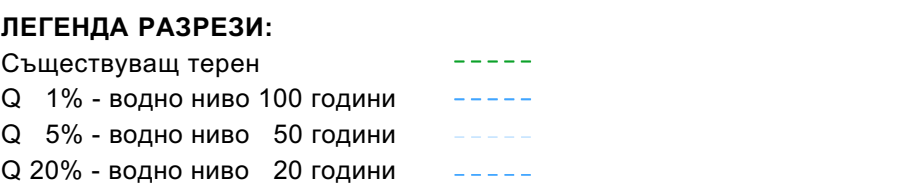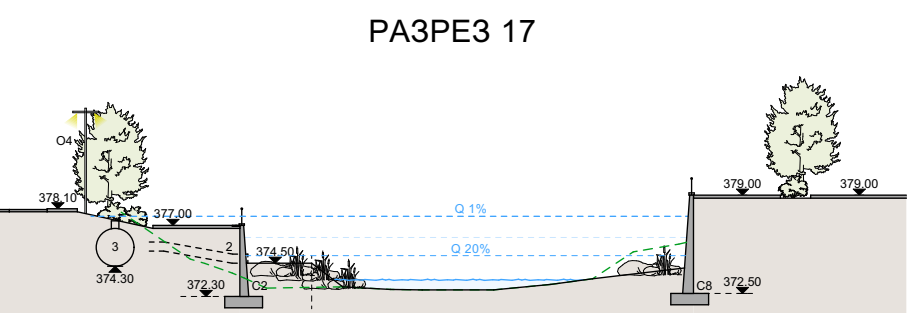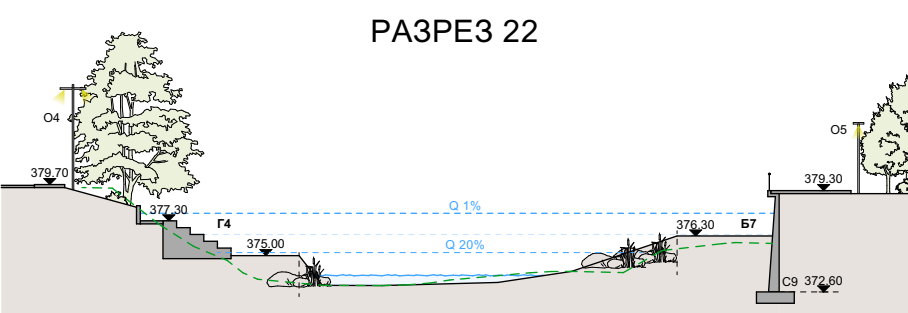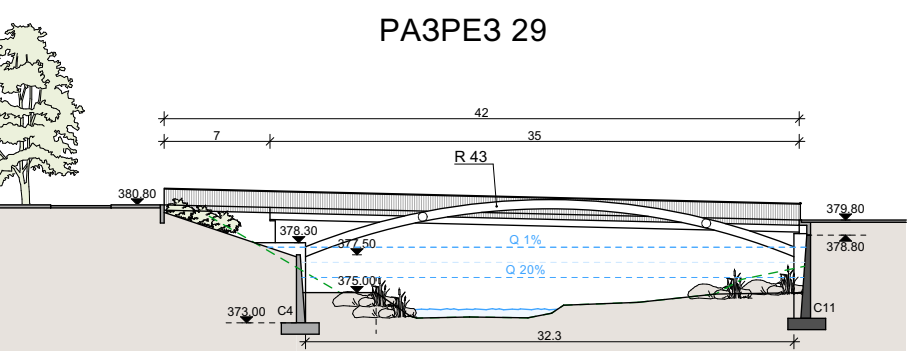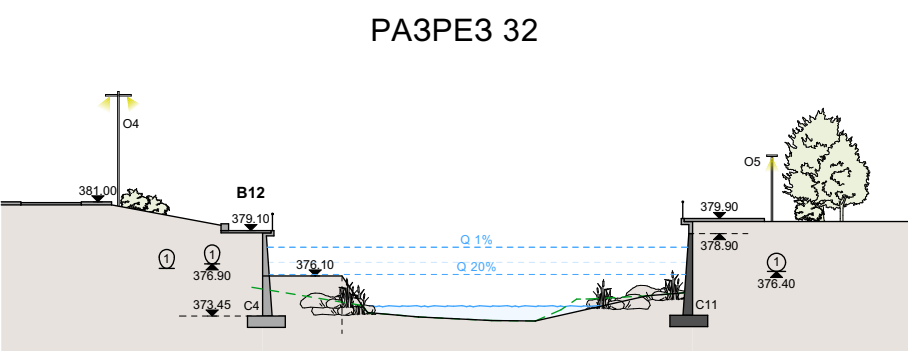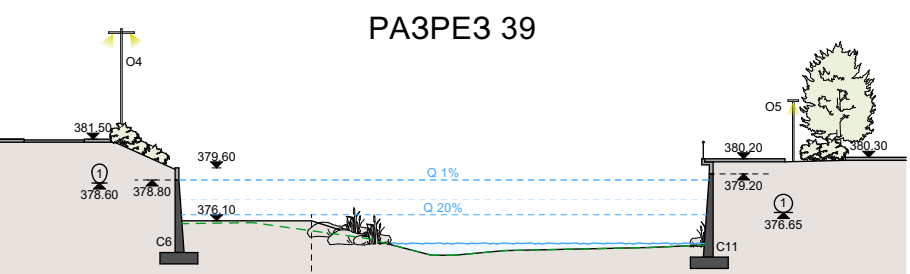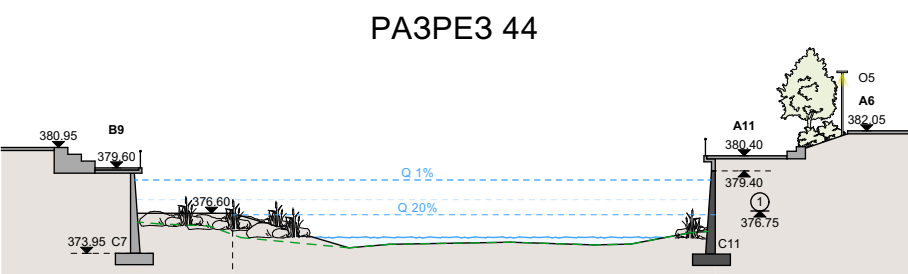

ЛЕГЕНДА РАЗРЕЗИ:

Съществуващ терен

Q 1% - водно ниво 100 години

Q 5% - водно ниво 50 години

Q 20% - водно ниво 20 години

ЗАБЕЛЕЖКА:

- разрезите съответстват на профилите от хидроложия доклад

АРКПРОЕКТ

АРКПРОЕКТ ООД - гр. ГАБРОВО, ул. НИКОЛАЕВСКА №7, тел. 066 805250

ОБЕКТ:
Благоустройство на крайната зона на р. Янтра в участъка между моста на ул. "Д-р Никола Василиади" и моста на ул. "Христо Ботев", гр. Габрово

ВЪЗЛОЖИТЕЛ:
ОБЩИНА ГАБРОВО

ЧАСТ:
АРХИТЕКТУРА

ЧЕРТЕЖ:
ГЕНЕРАЛЕН ПЛАН

ФАЗА: Работен проект МАЩАБ: 1:1000 ЛИСТ №: 01

ПРОЕКТАНТИ: арх. М. Хлебарова, арх. С. Семов

СЪГЛАСУВАЛИ:
Либл л.арх. В. Христов
Геодезия инж. С. Колев
Конструкции инж. Р. Матев
Ел инж. Г. Гичев
ВиК инж. М. Ангелова
Пътна инж. Хр. Колев

ДАТА: 11/2024